

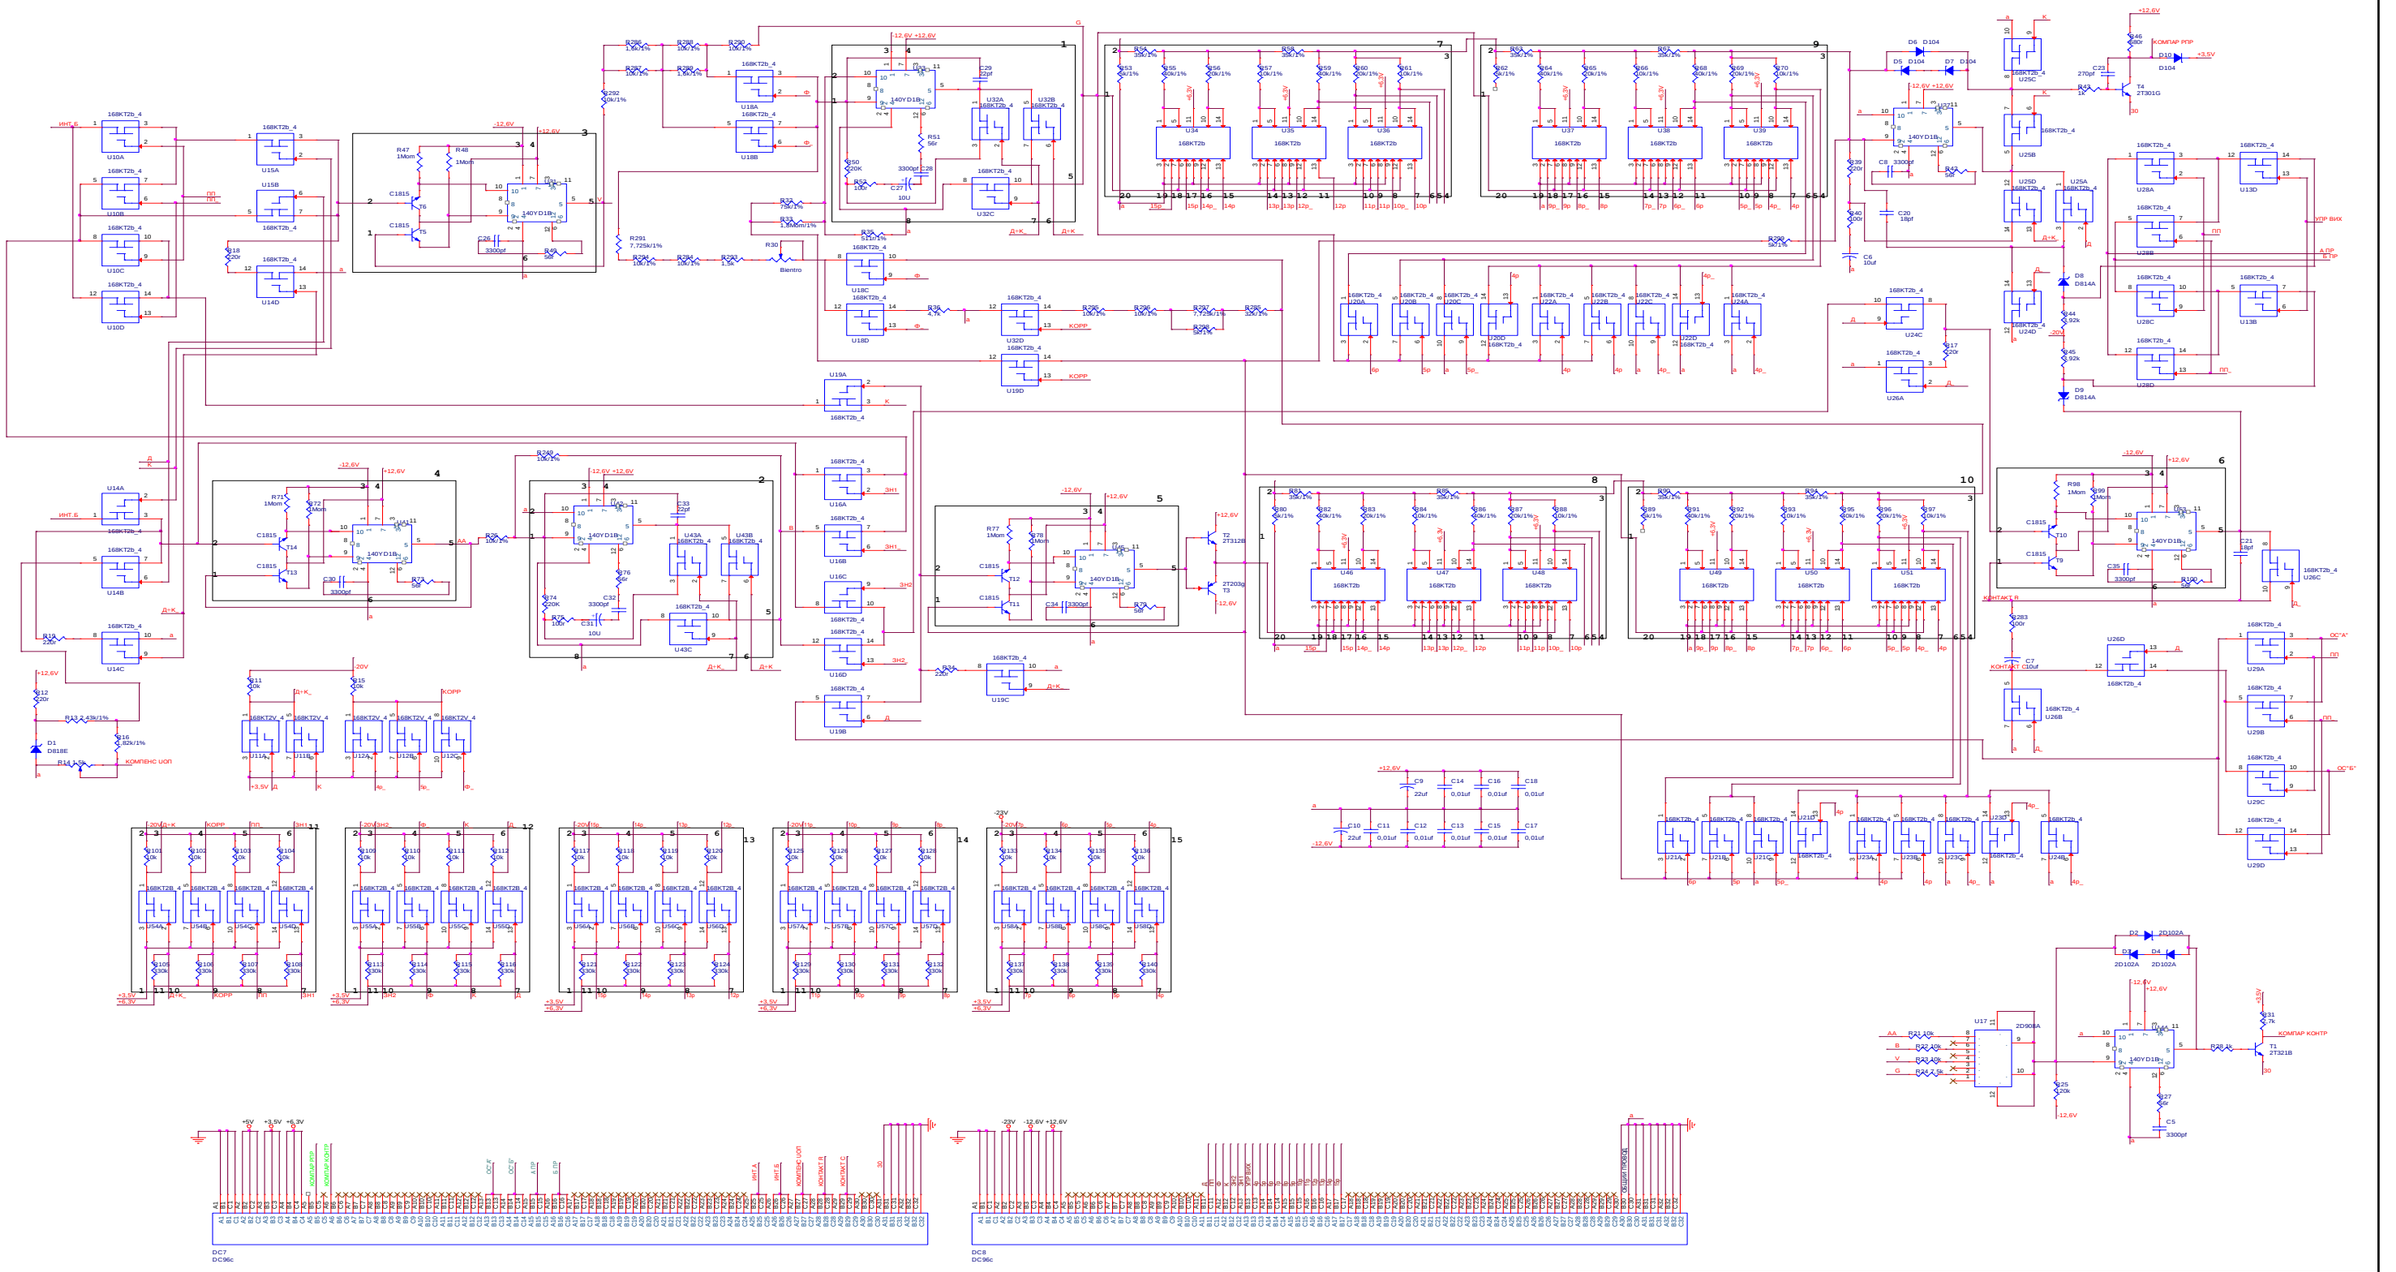


					THIẾT BỊ MÁY TÍNH DẪN ĐƯỜNG A313-V
					SƠ ĐỒ NGUYÊN LÝ CỤM BIẾN ĐỔI
					07MB.A313-V.BV.14
Sđ	*S.lg*	*Số tài liệu*	*Chữ ký*	*Ngày*	*Dấu* / *Khối lượng* / *Tỉ lệ*
T. Phòng		*Ng.Thanh Hùng*			A
Tổ trưởng					*Tờ số: 01* / *Số tờ: 01*
Kiểm tra		*Ng. Văn Biển*			
Thiết kế		*Bùi Cao Ninh*			**VIỆN KỸ THUẬT PK-KQ**
Vẽ		*Bùi Cao Ninh*			
K.T.T.C		*Bùi Cao Ninh*			

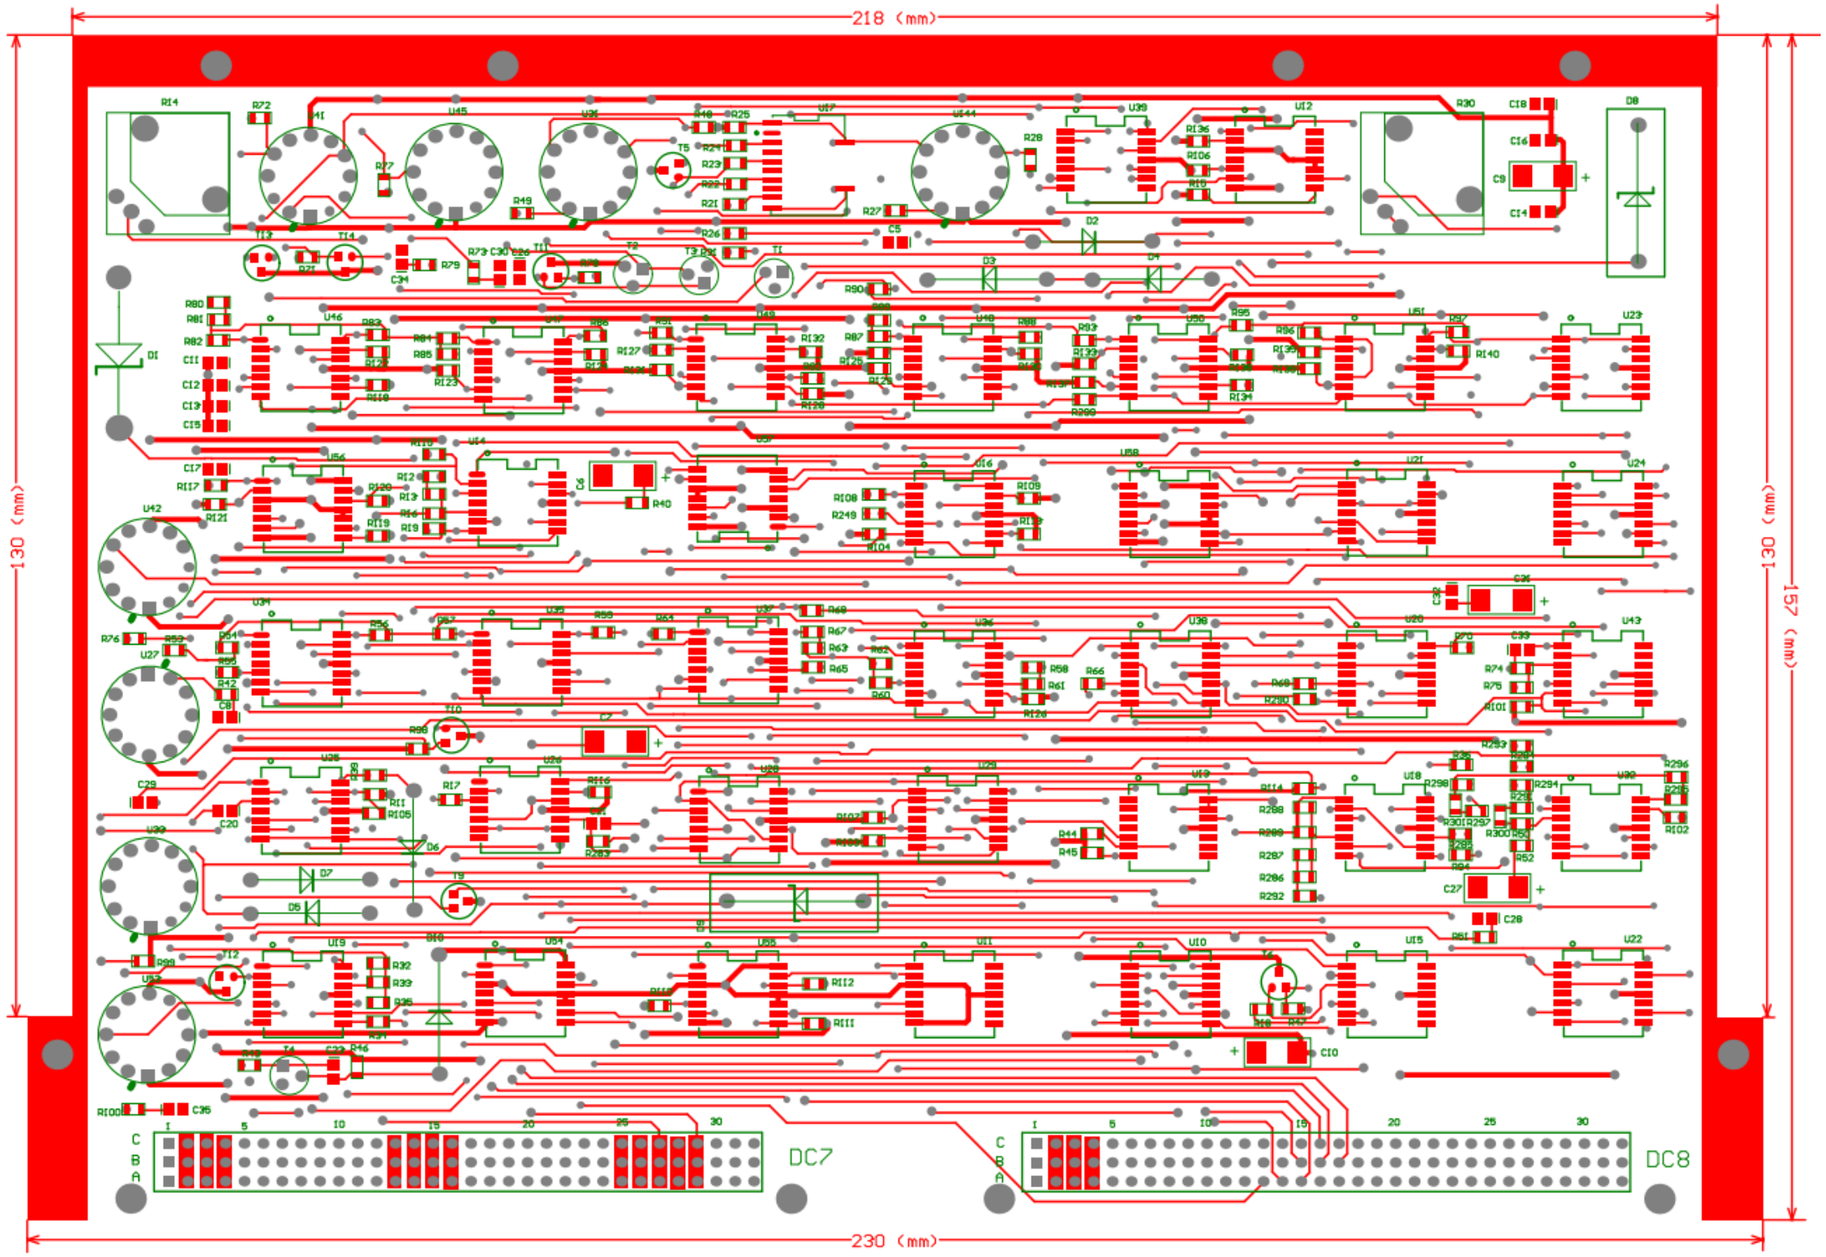

					THIẾT BỊ MÁY TÍNH DẪN ĐƯỜNG A313-V
					SƠ ĐỒ MẠCH IN MẶT TRÊN CỤM BIẾN ĐỔI
					07MB.A313-V.BV.15
Sđ	*S.lg*	*Số tài liệu*	*Chữ ký*	*Ngày*	*Dấu* / *Khối lượng* / *Tỉ lệ*
T. Phòng		*Ng.Thanh Hùng*			A
Tổ trưởng					*Tờ số: 01* / *Số tờ: 01*
Kiểm tra		*Ng. Văn Biển*			**VIỆN KỸ THUẬT PK-KQ**
Thiết kế		*Bùi Cao Ninh*			
Vẽ		*Bùi Cao Ninh*			
K.T.T.C		*Bùi Cao Ninh*			

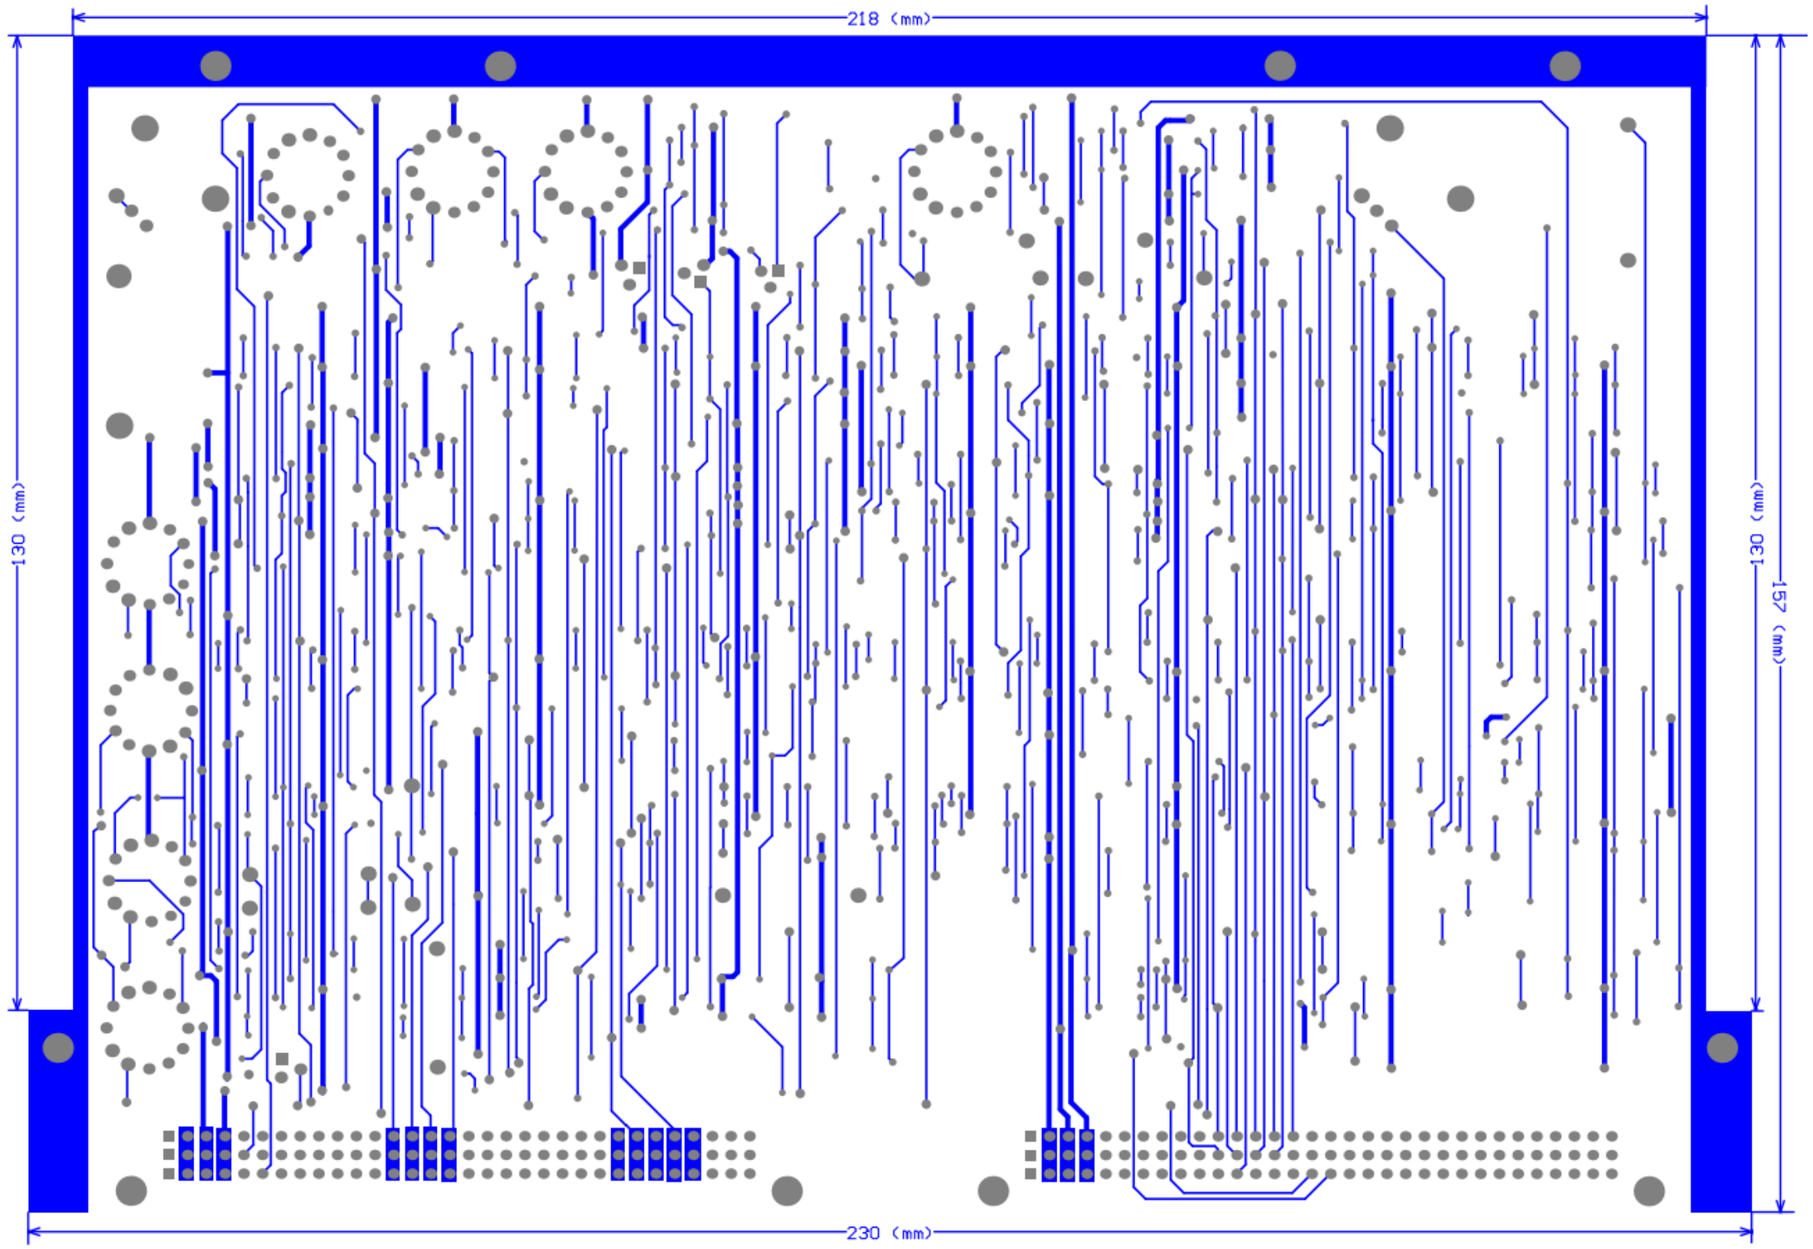

					THIẾT BỊ MÁY TÍNH DẪN ĐƯỜNG A313-V
					SƠ ĐỒ MẠCH IN MẶT DƯỚI CỤM BIẾN ĐỔI
Sđ	S.lg	Số tài liệu	Chữ ký	Ngày	**07MB.A313-V.BV.16**
T. Phòng		Ng.Thanh Hùng			Dấu: A / Khối lượng / Tỉ lệ
Tổ trưởng					
Kiểm tra		Ng. Văn Biển			
Thiết kế		Bùi Cao Ninh			Tờ số: 01 / Số tờ: 01
Vẽ		Bùi Cao Ninh			**VIỆN KỸ THUẬT PK-KQ**
K.T.T.C		Bùi Cao Ninh			