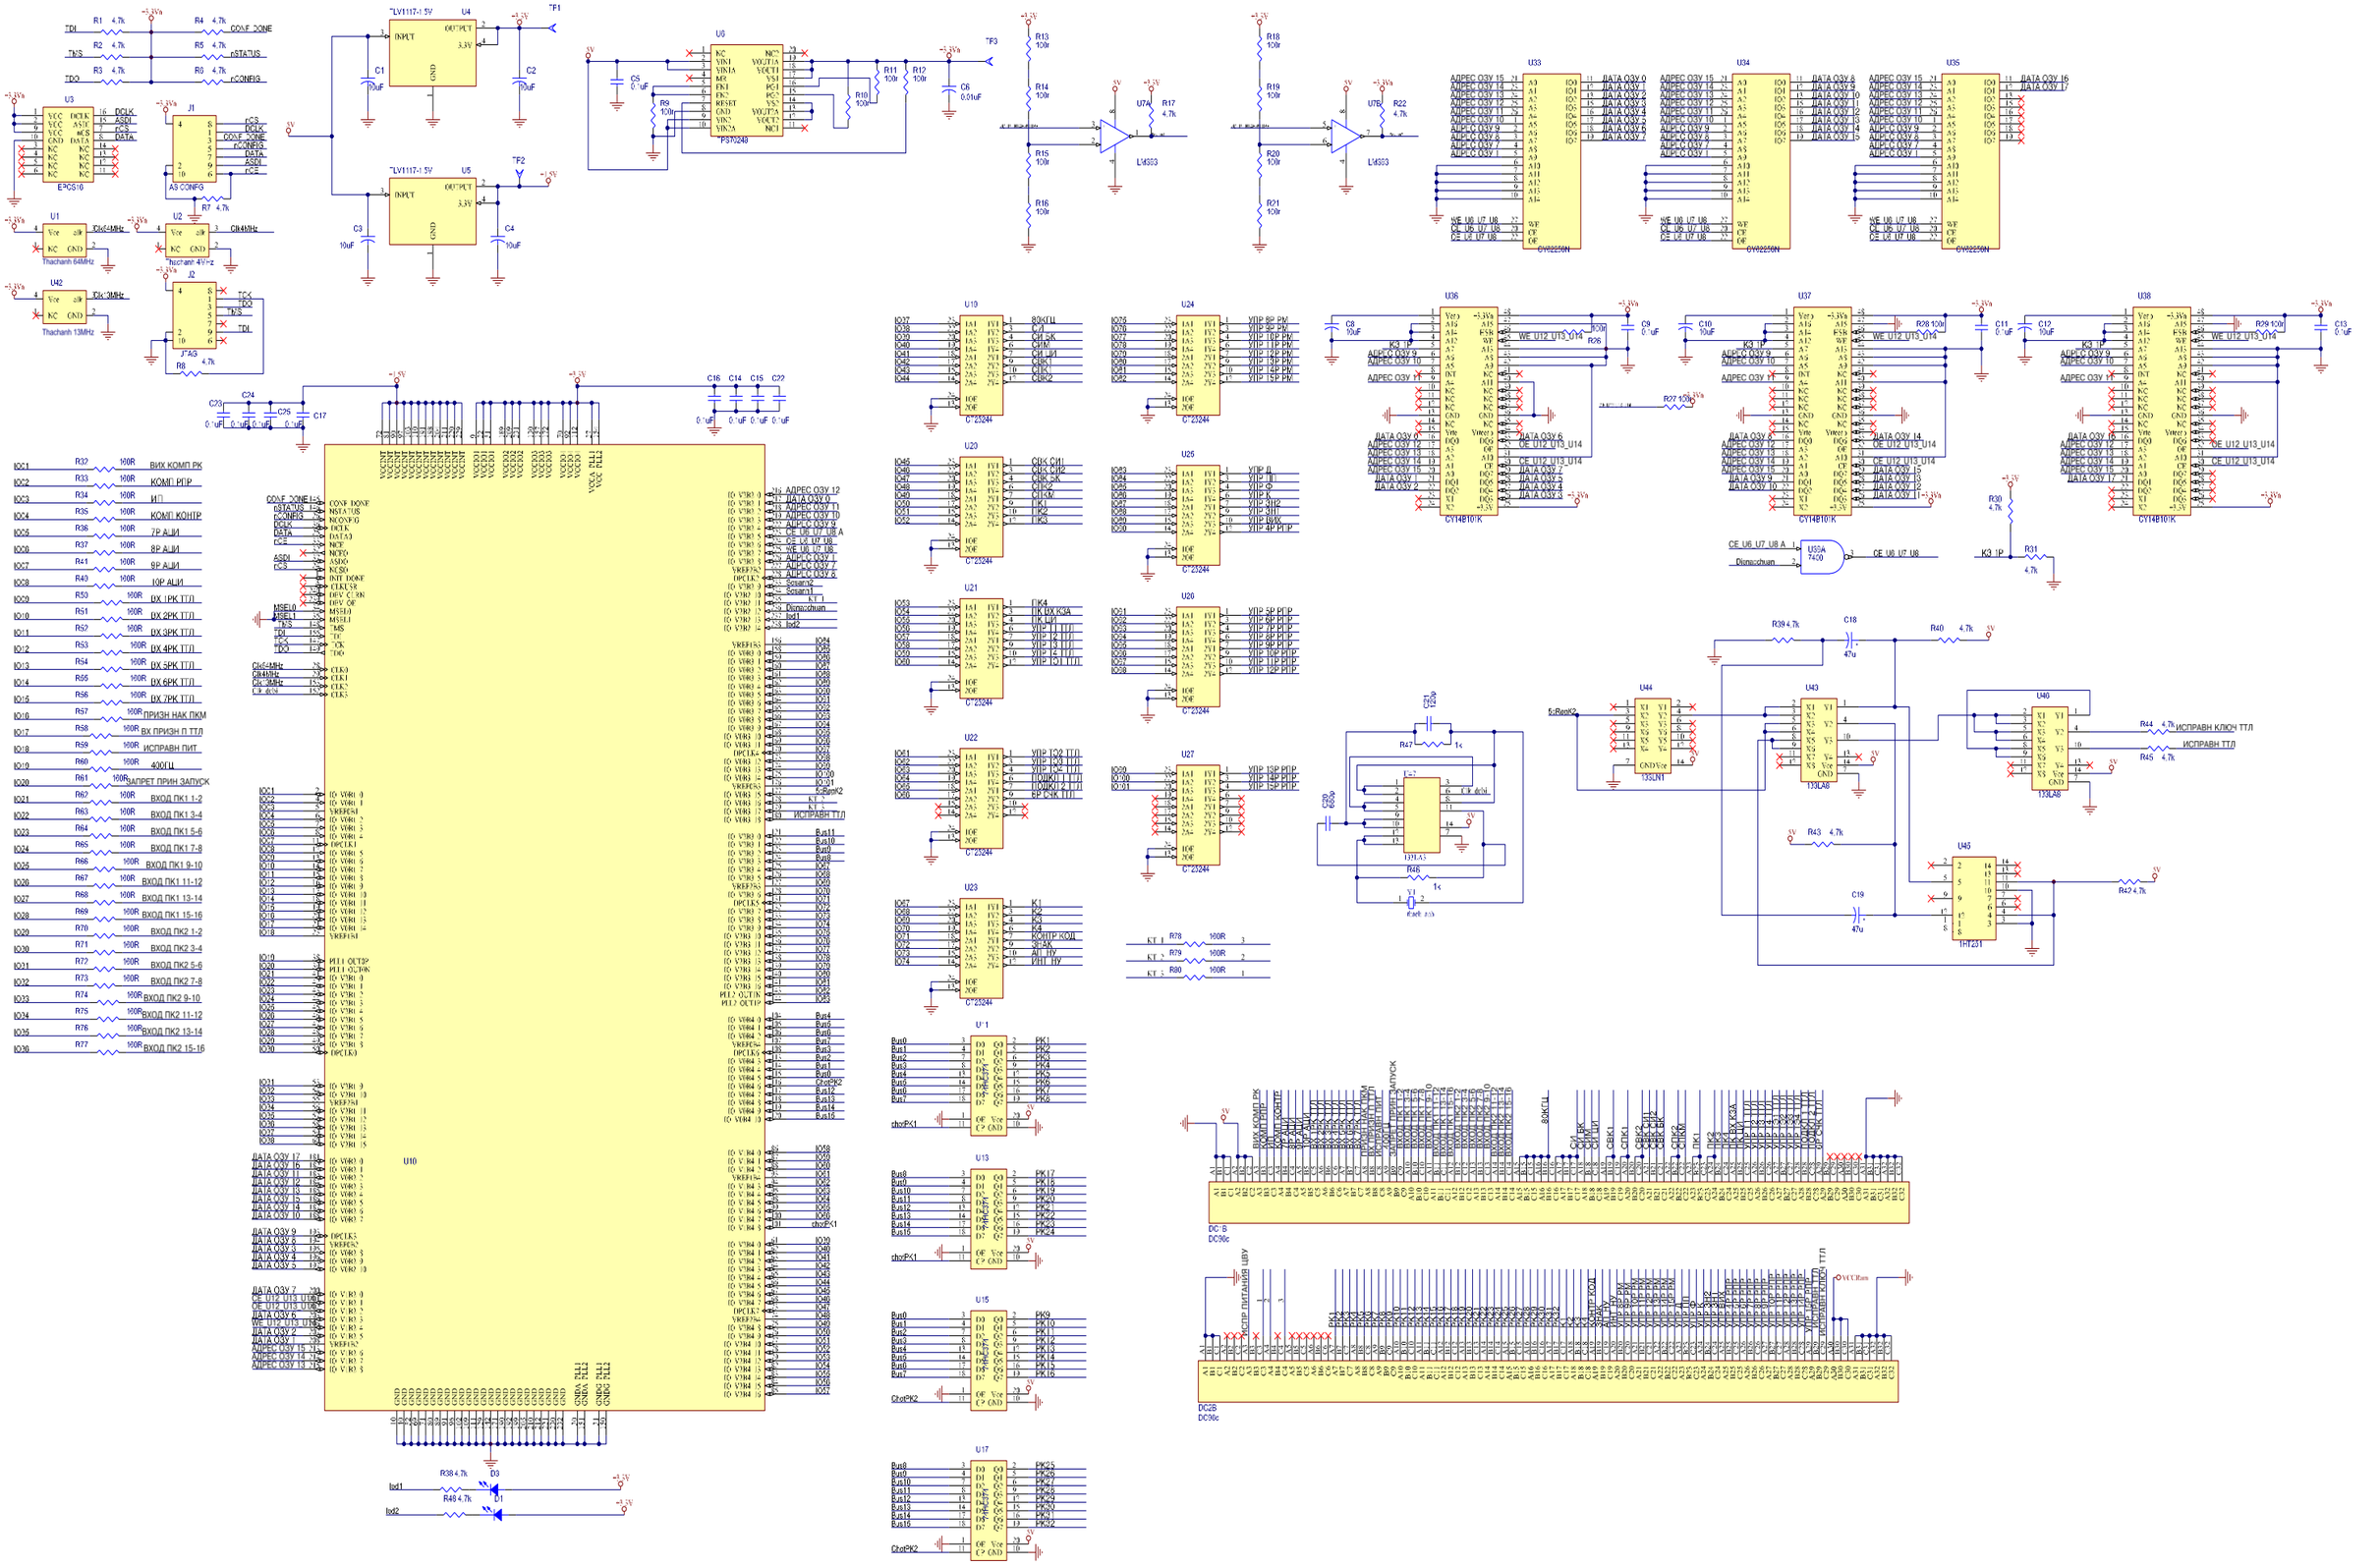
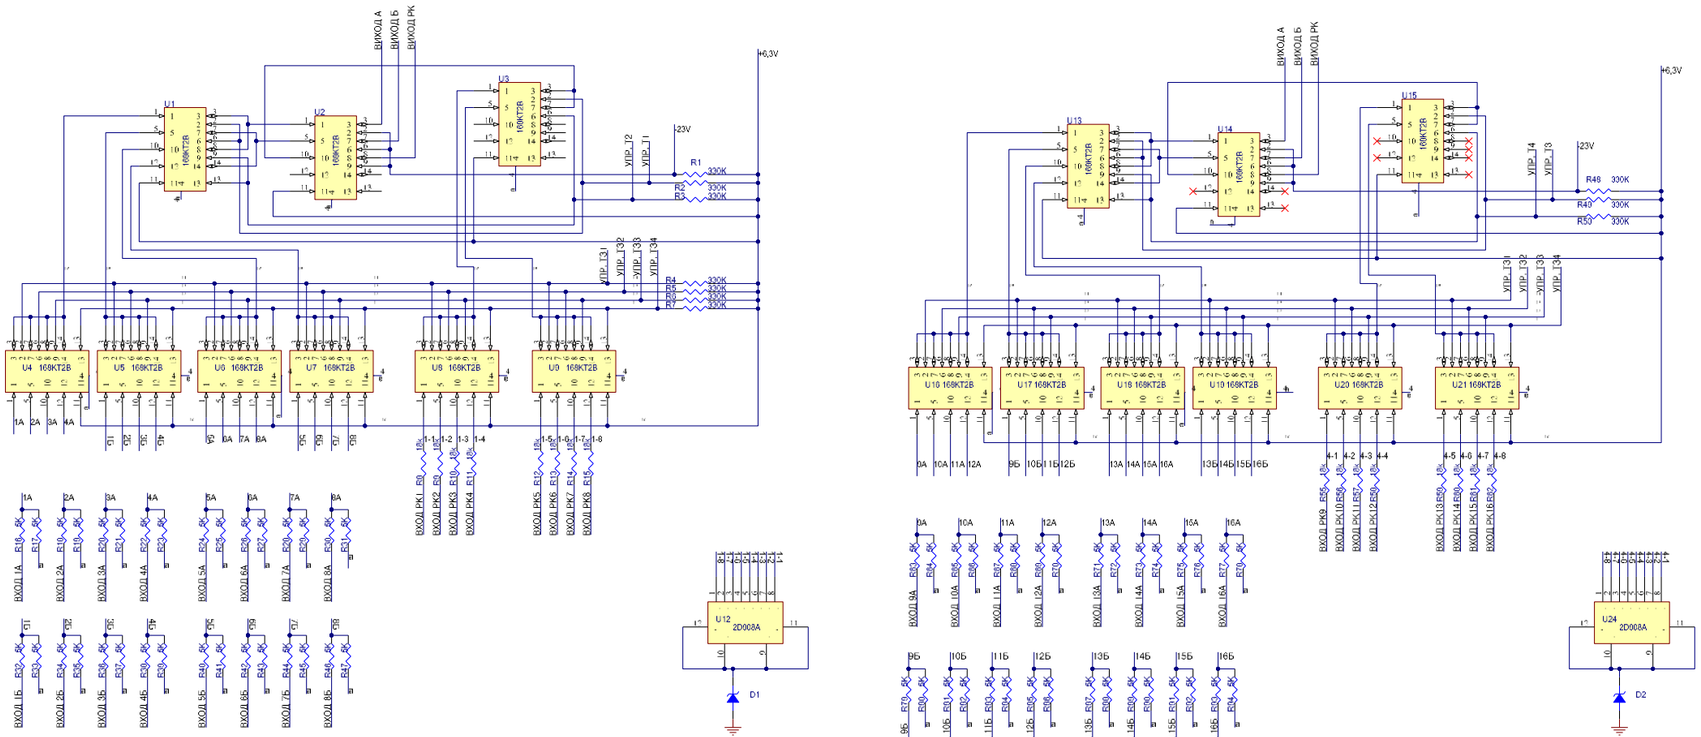
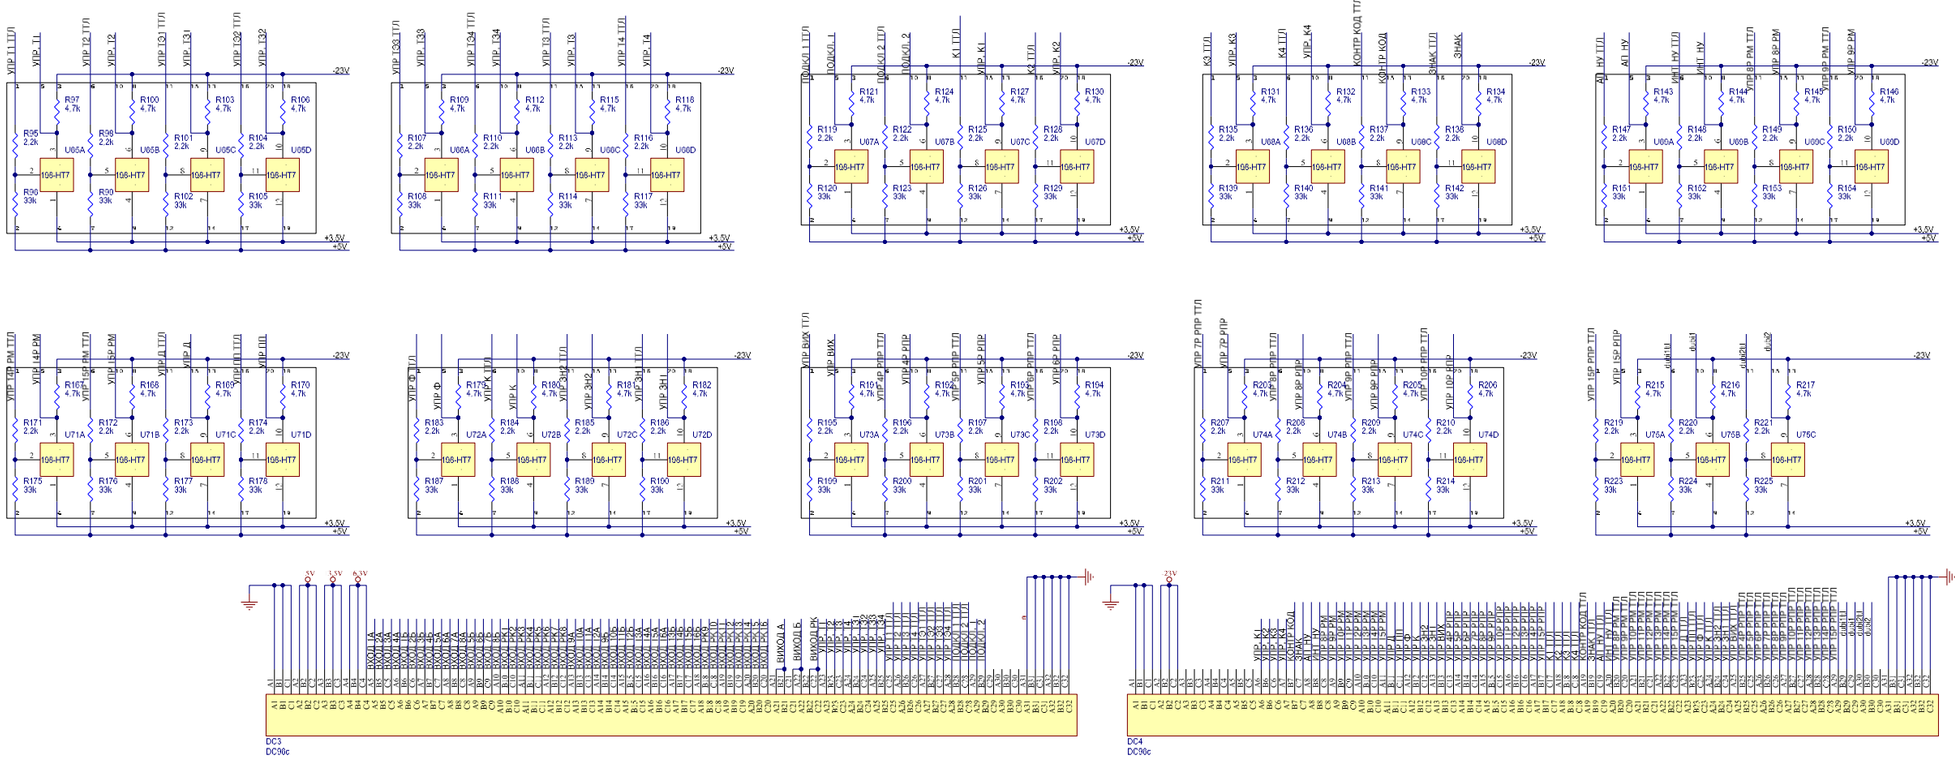


# SƠ ĐỒ NGUYÊN LÝ MẠCH ĐIỆN CỤM ĐIỀU KHIỂN VÀ XỬ LÝ TRUNG TÂM A313_V.01

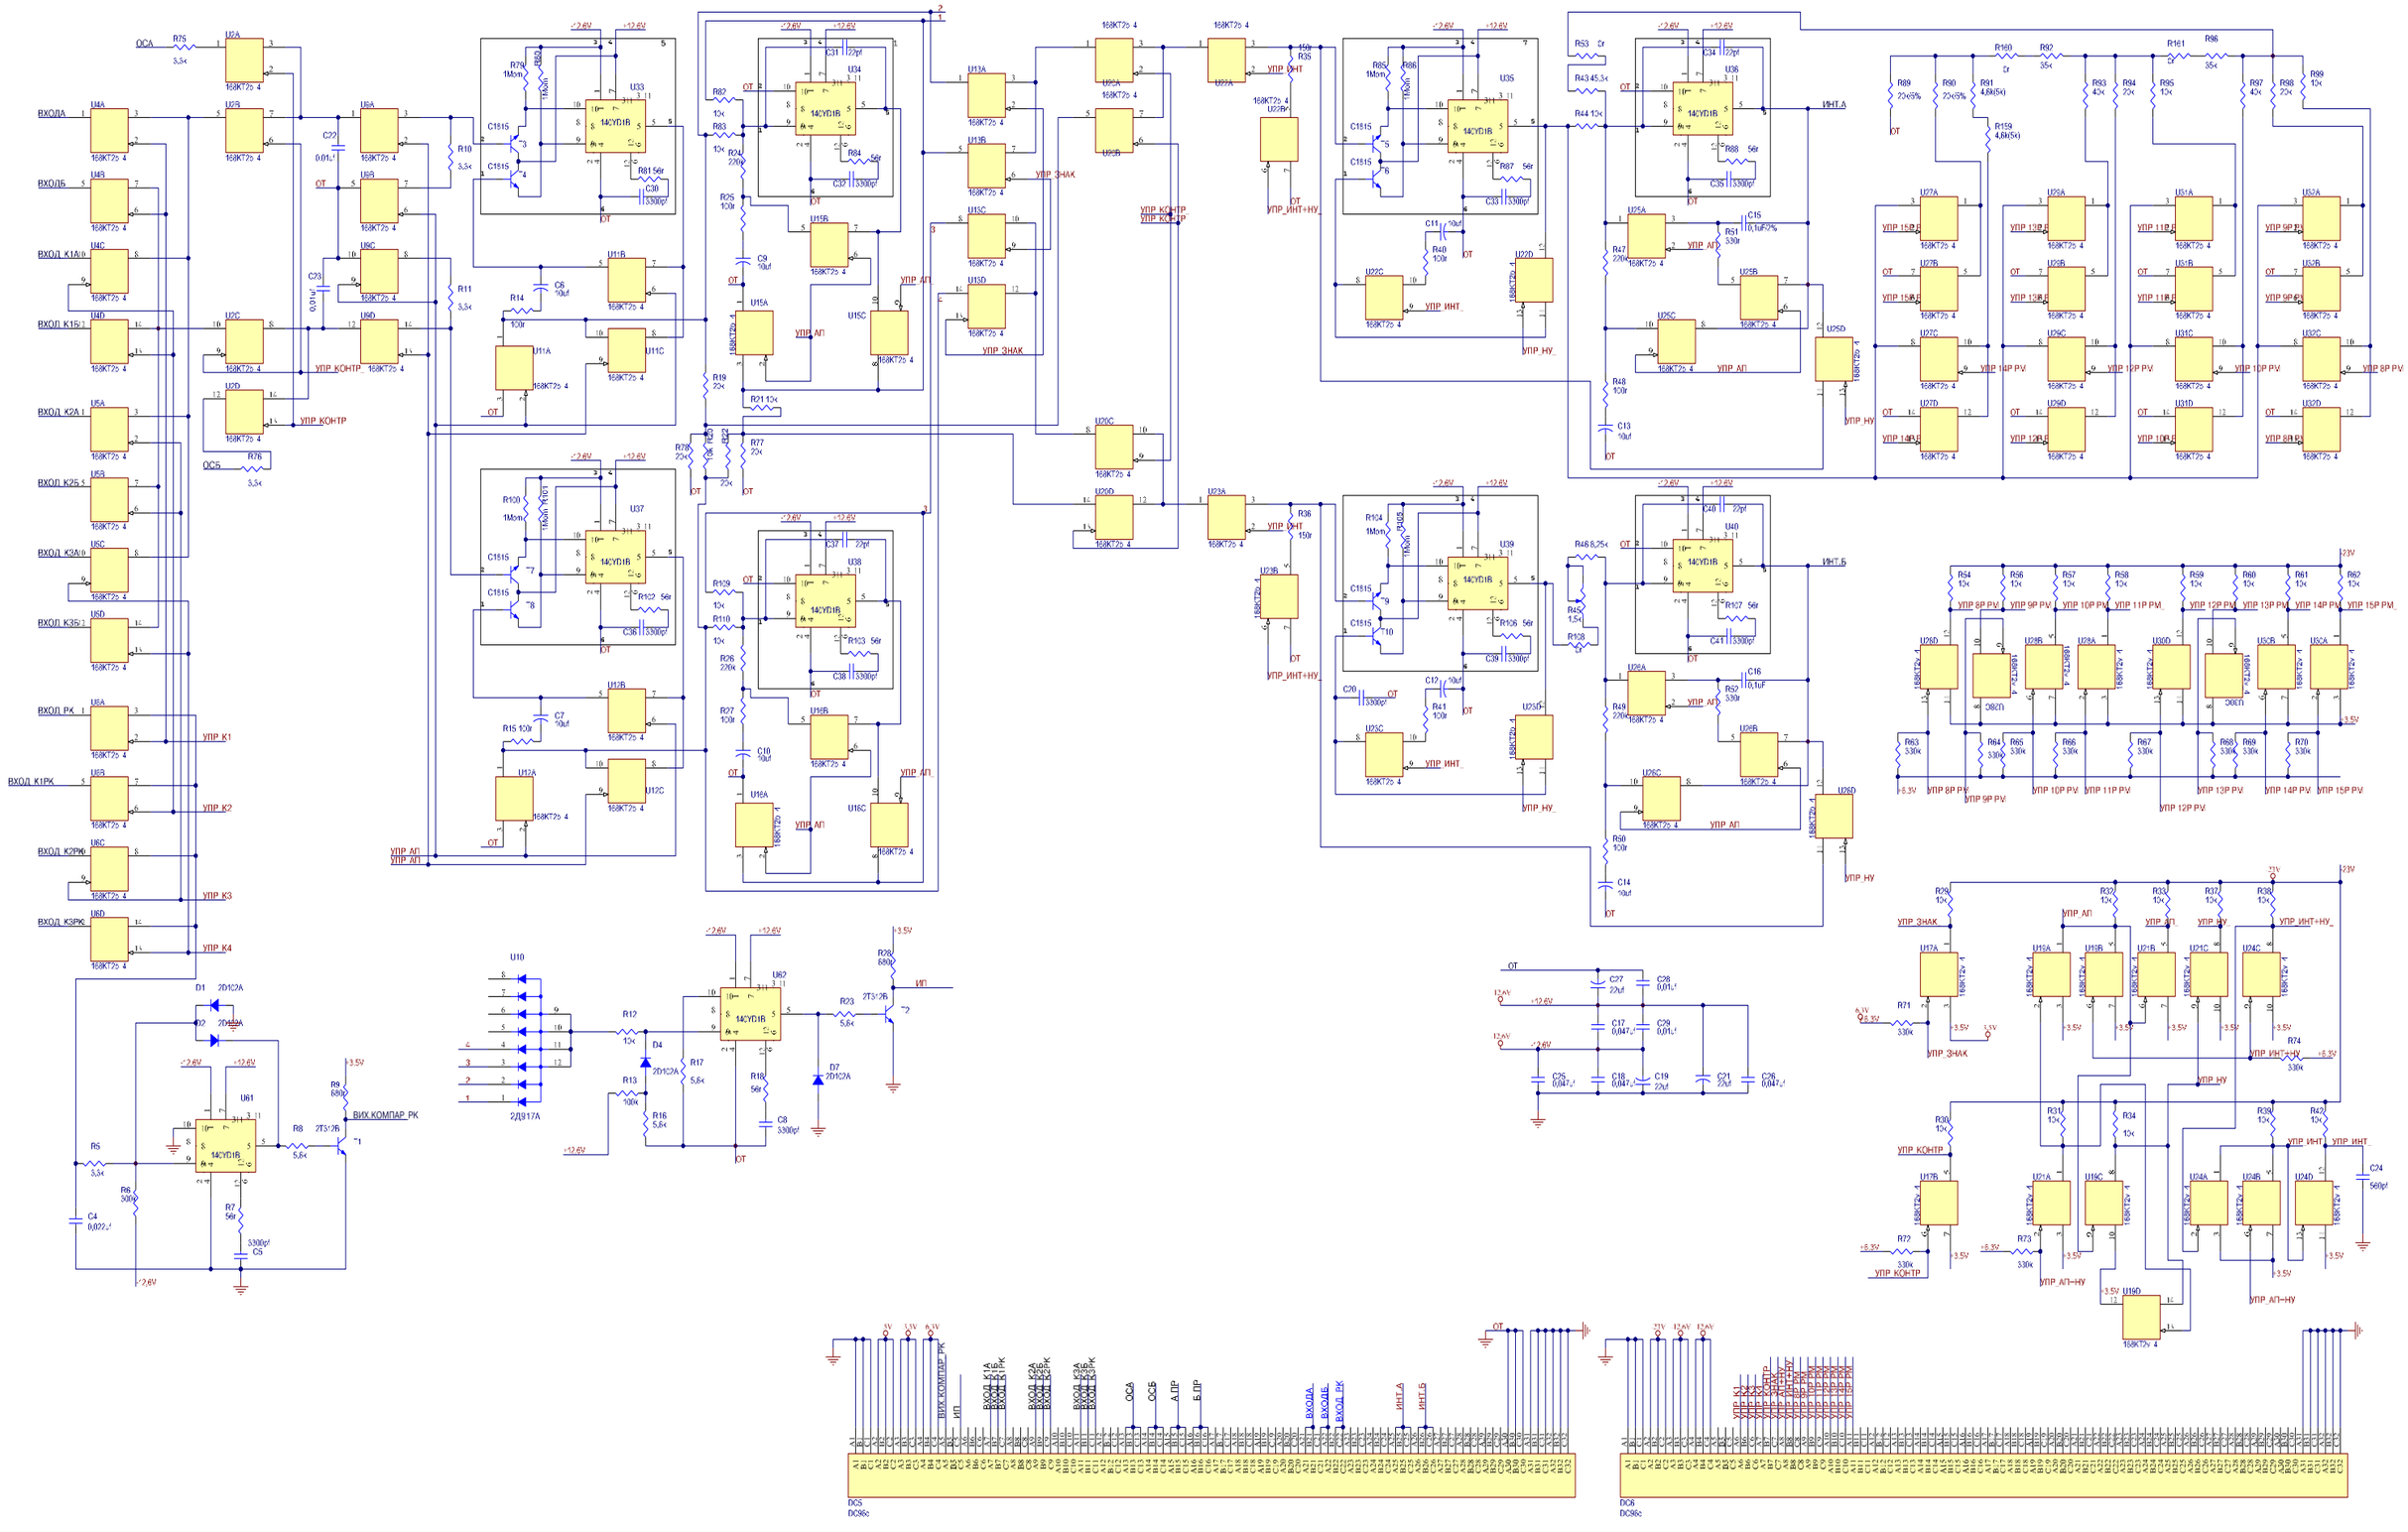


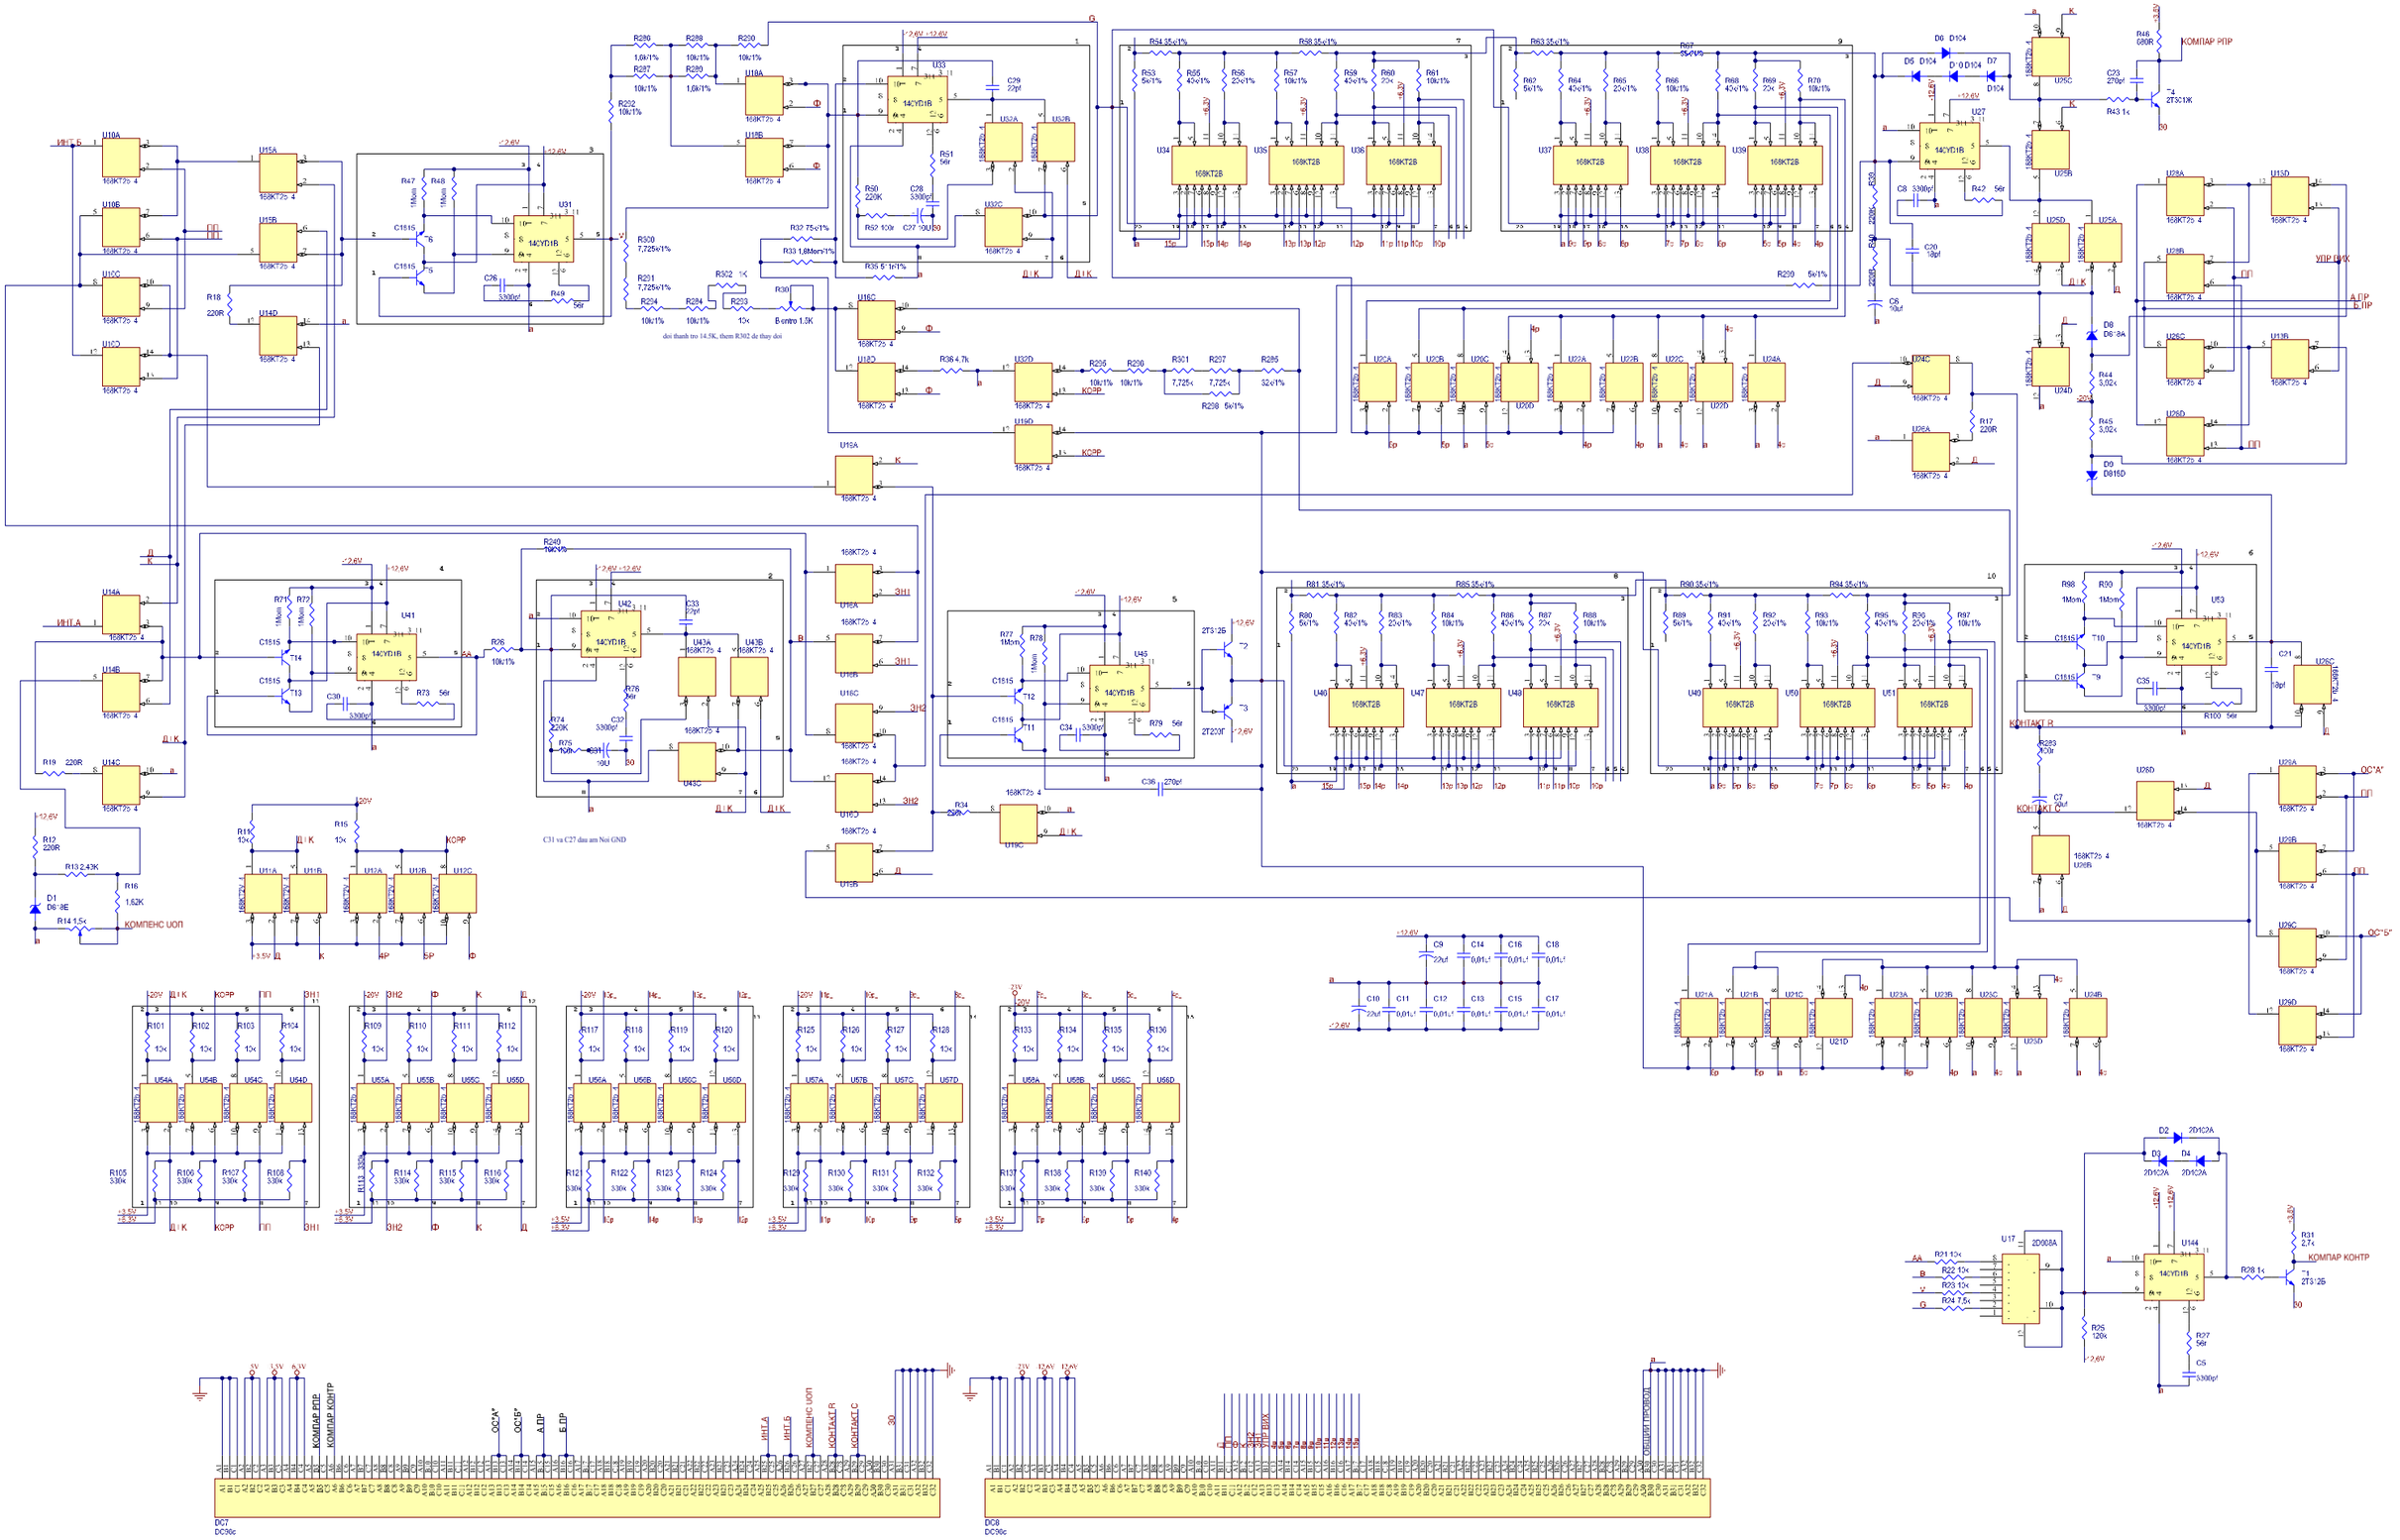




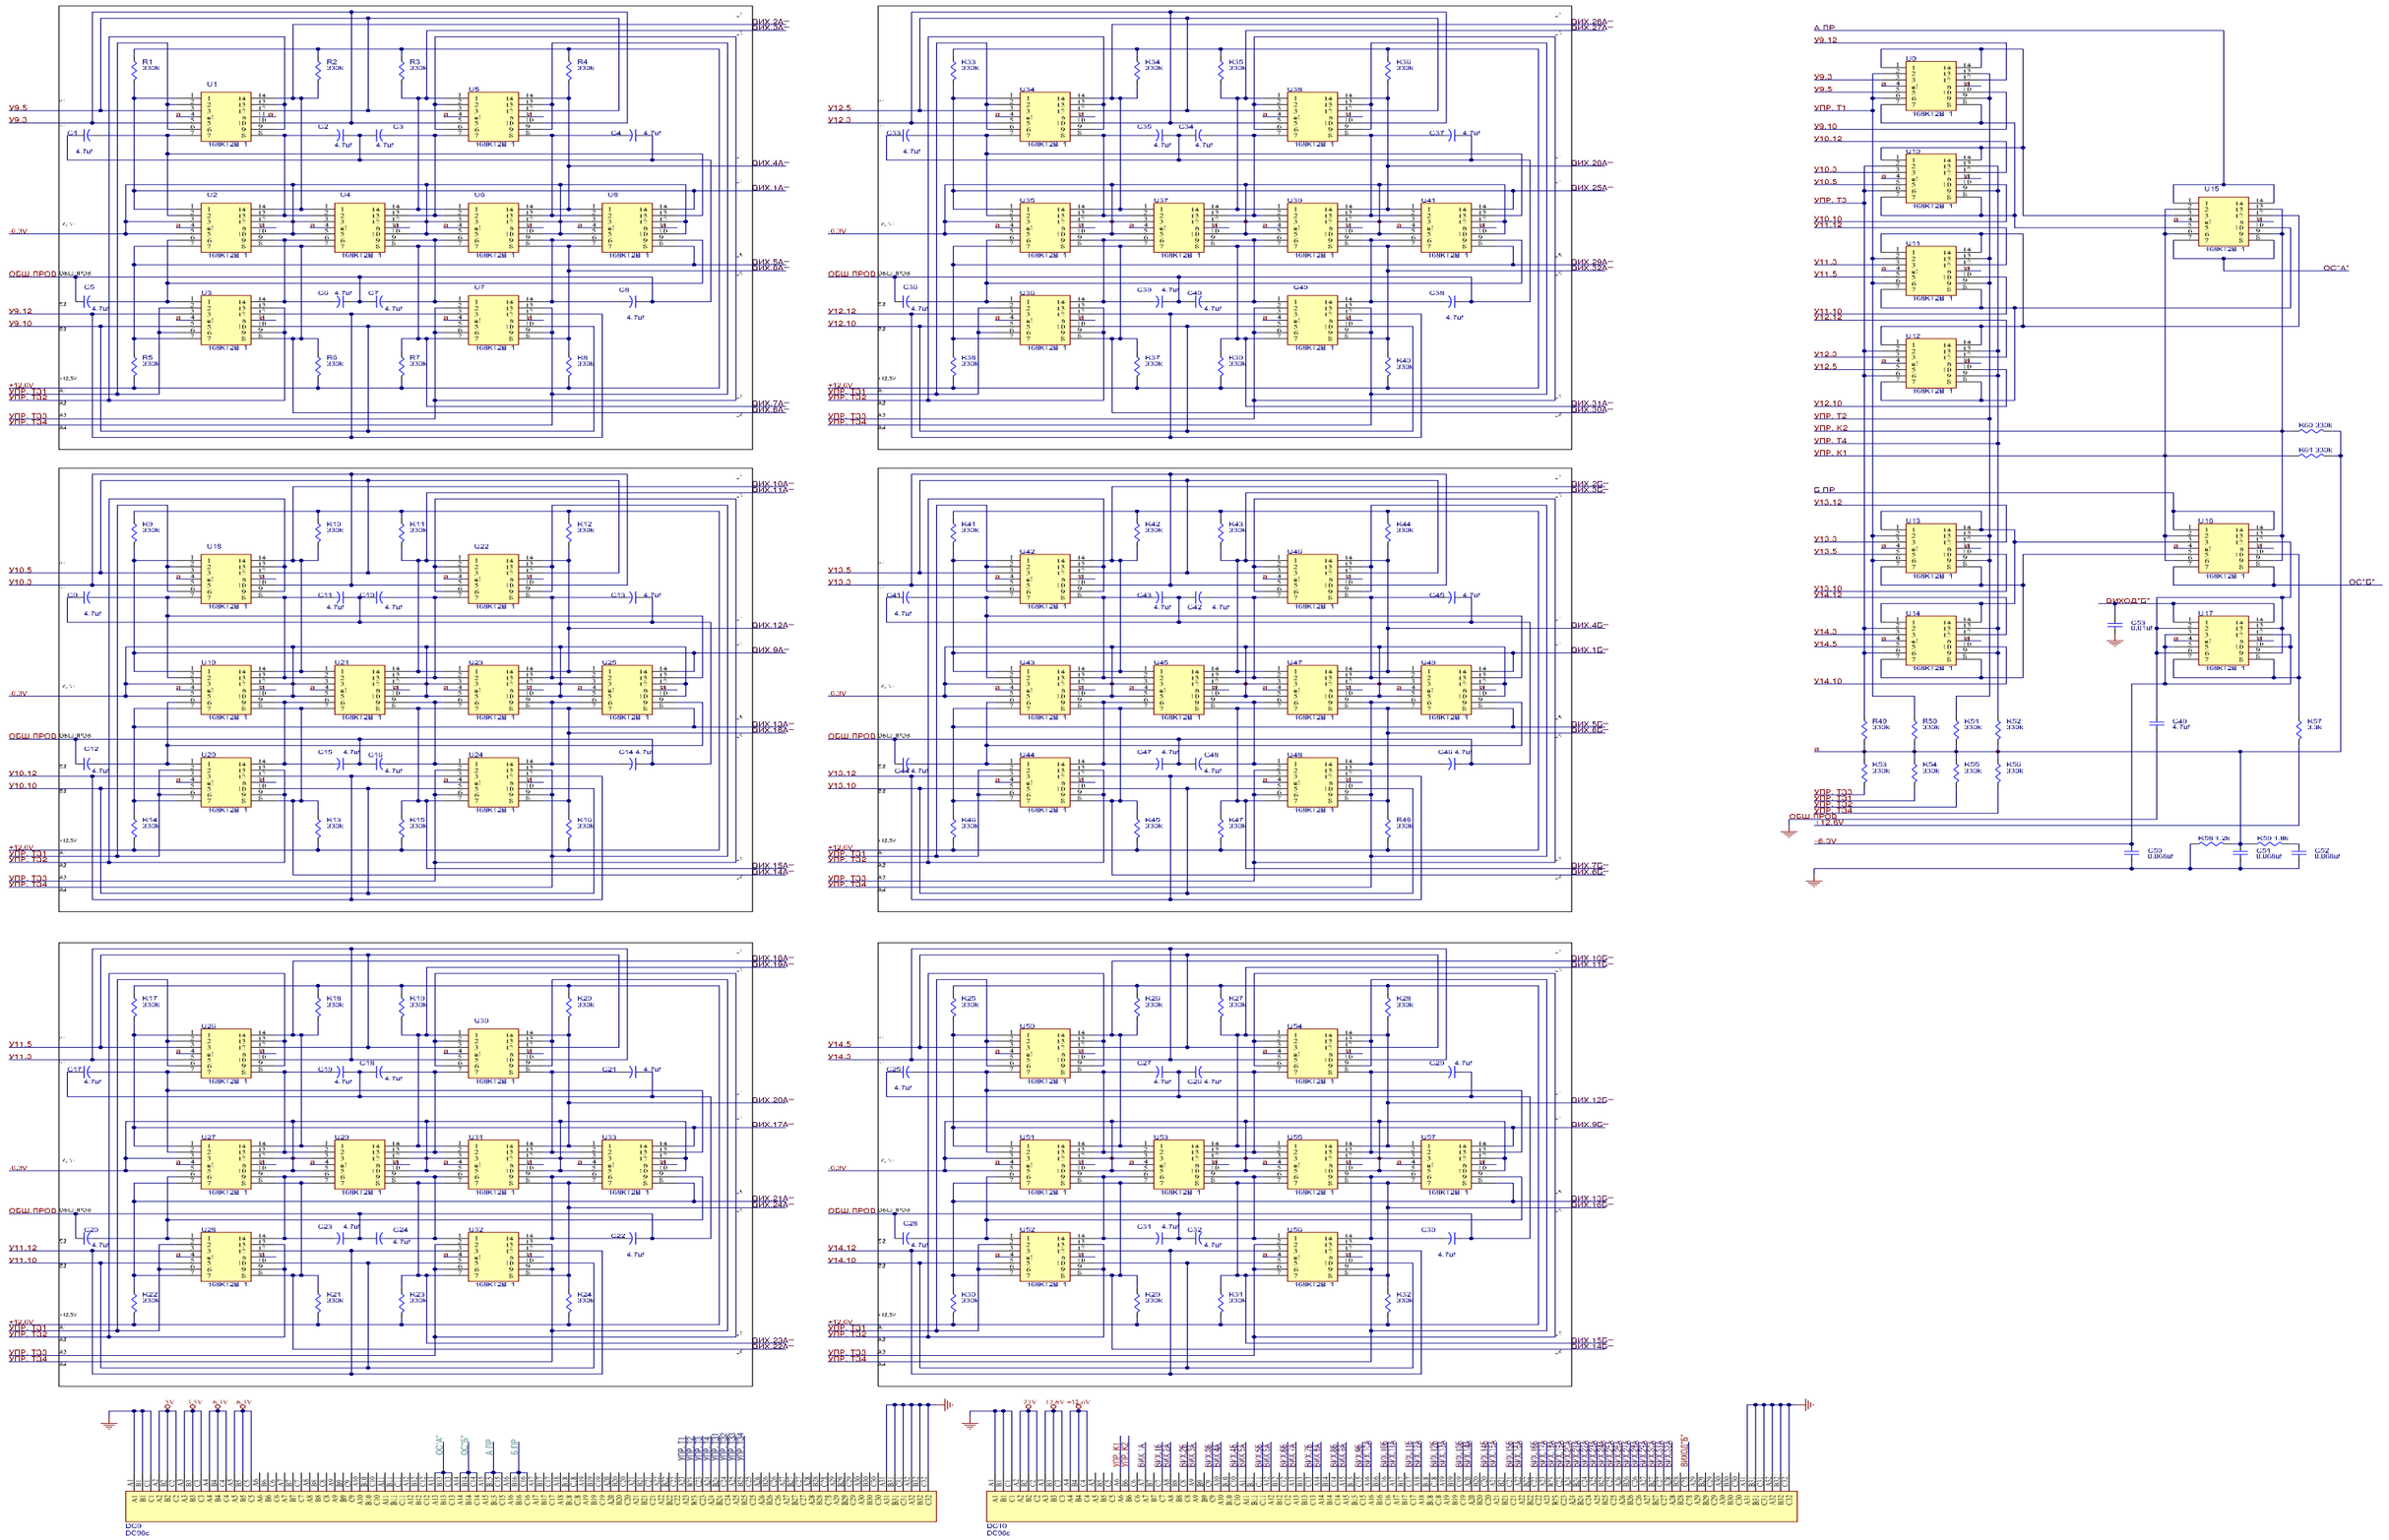
# SƠ ĐỒ NGUYÊN LÝ MẠCH ĐIỆN CỤM CHUYỂN MẠCH TÍN HIỆU VÀO A313_V.02



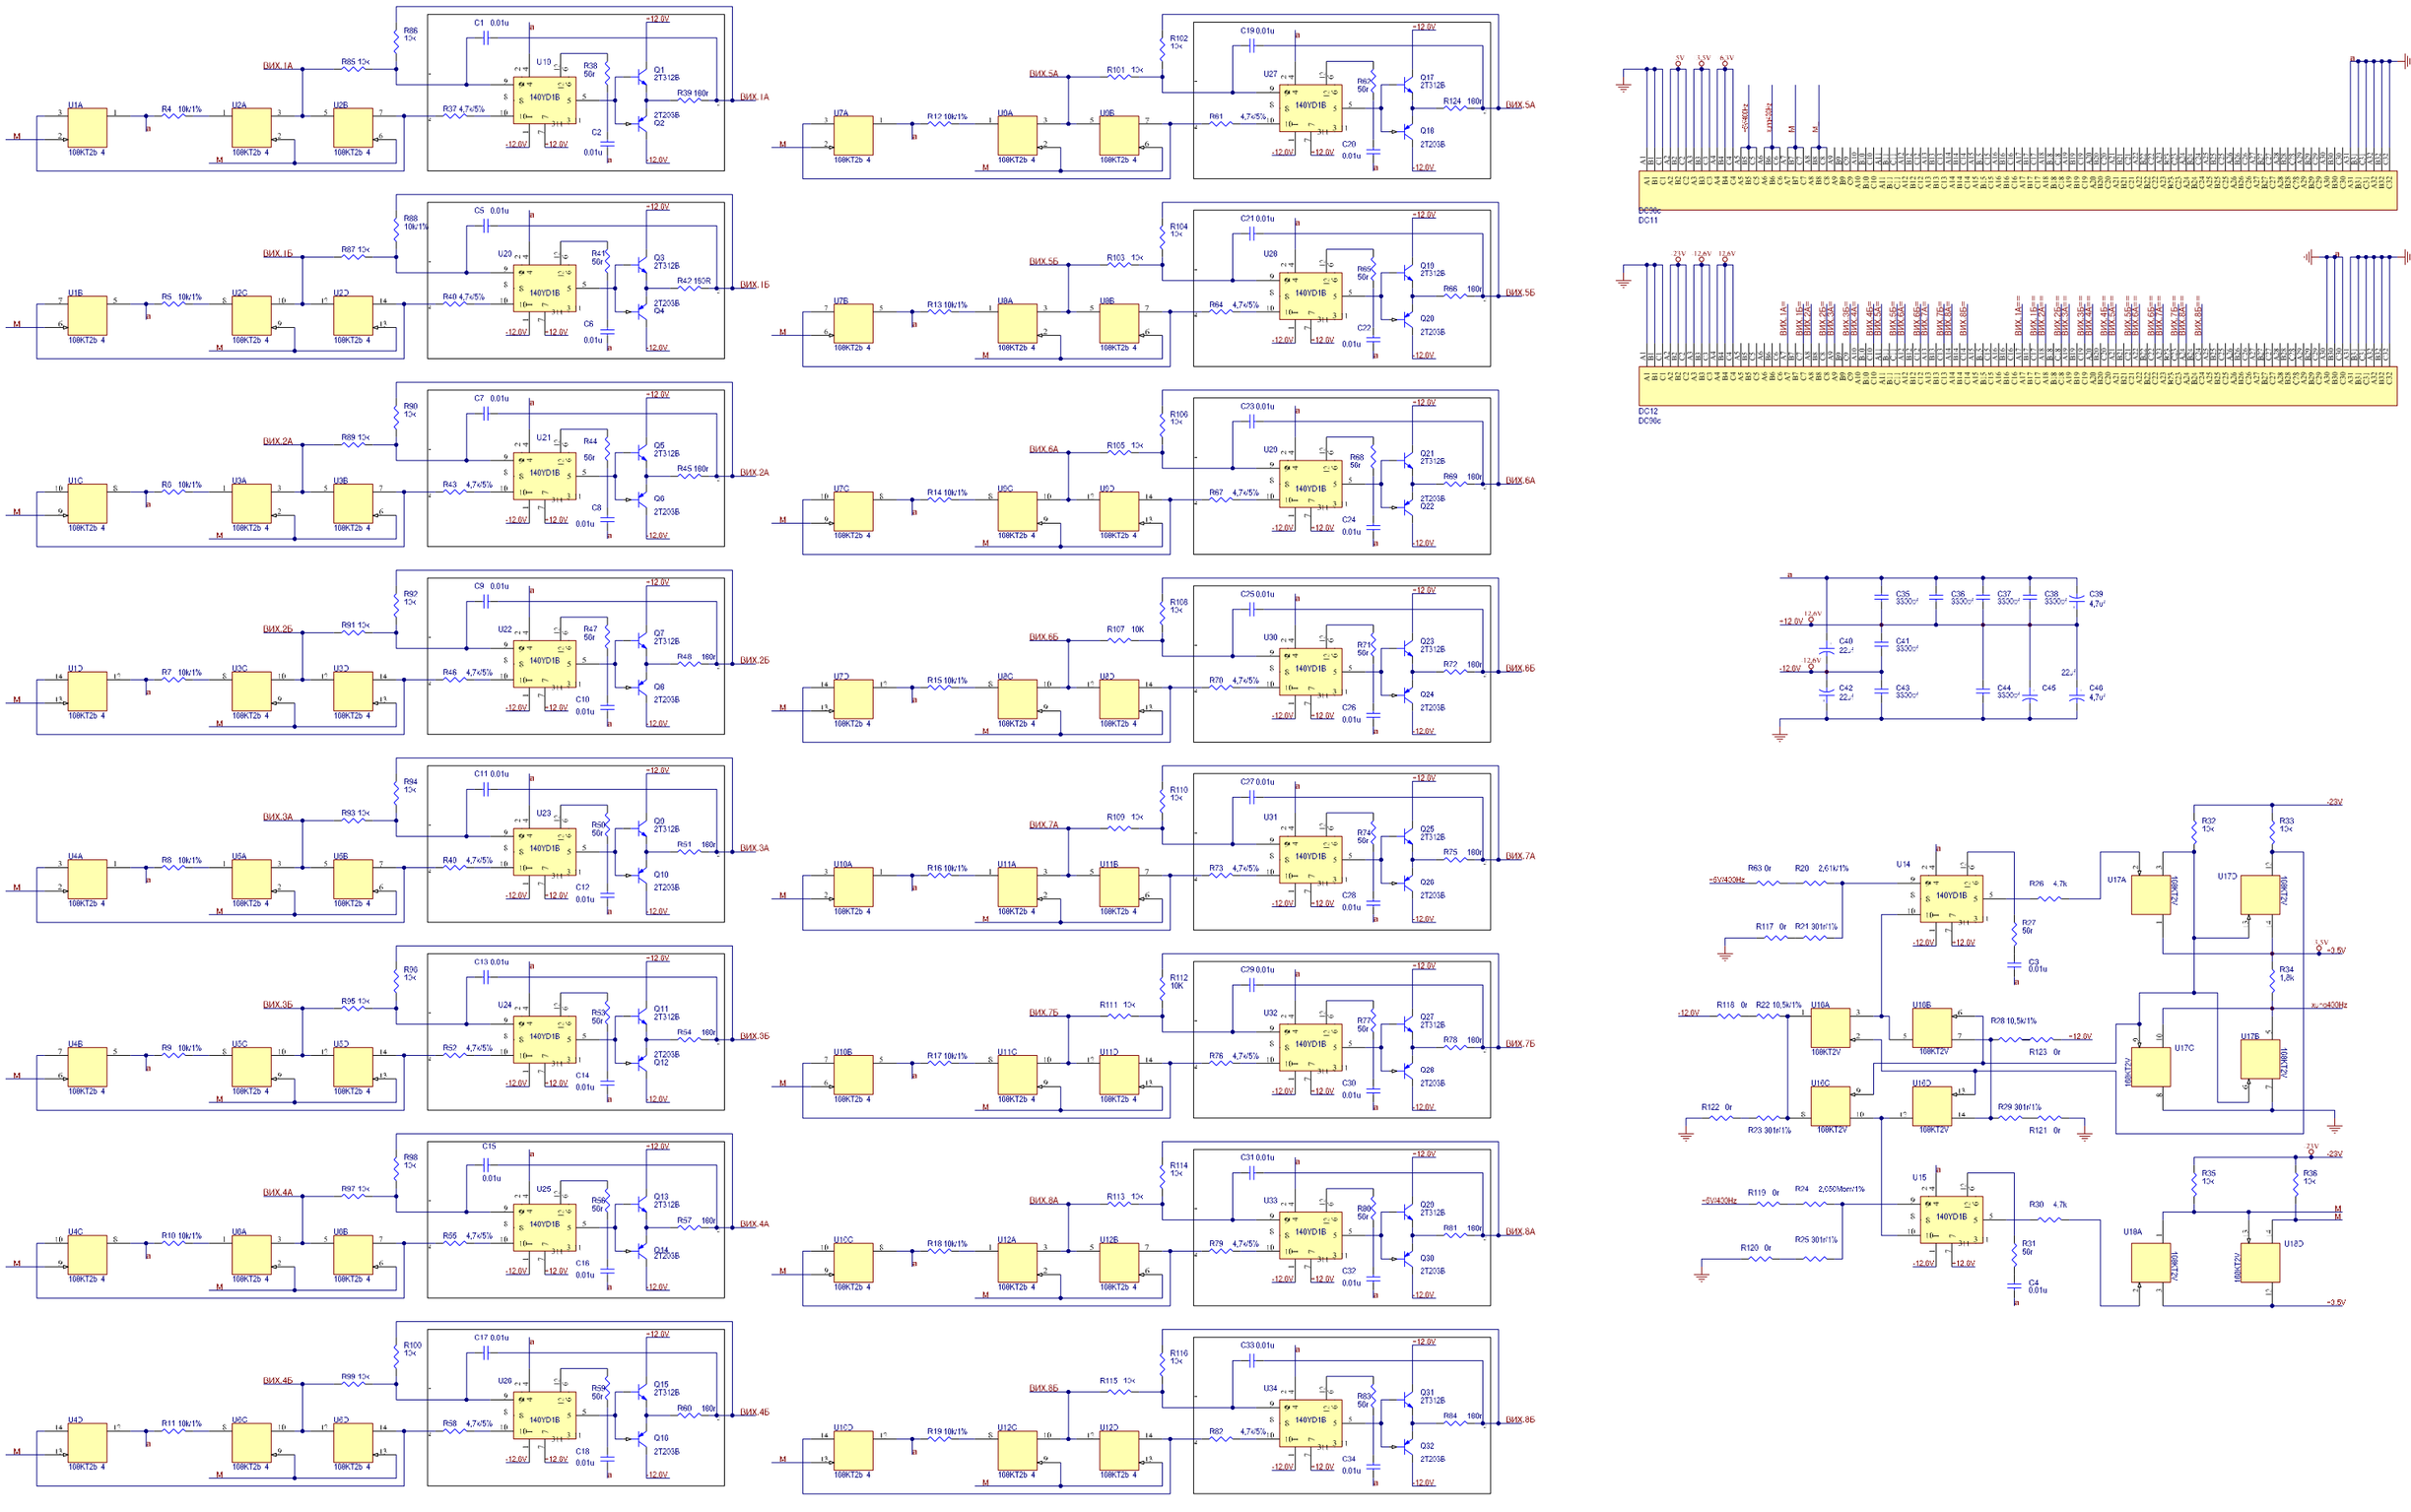

# SƠ ĐỒ NGUYÊN LÝ MẠCH ĐIỆN CỤM TÍCH PHÂN A313_V.03



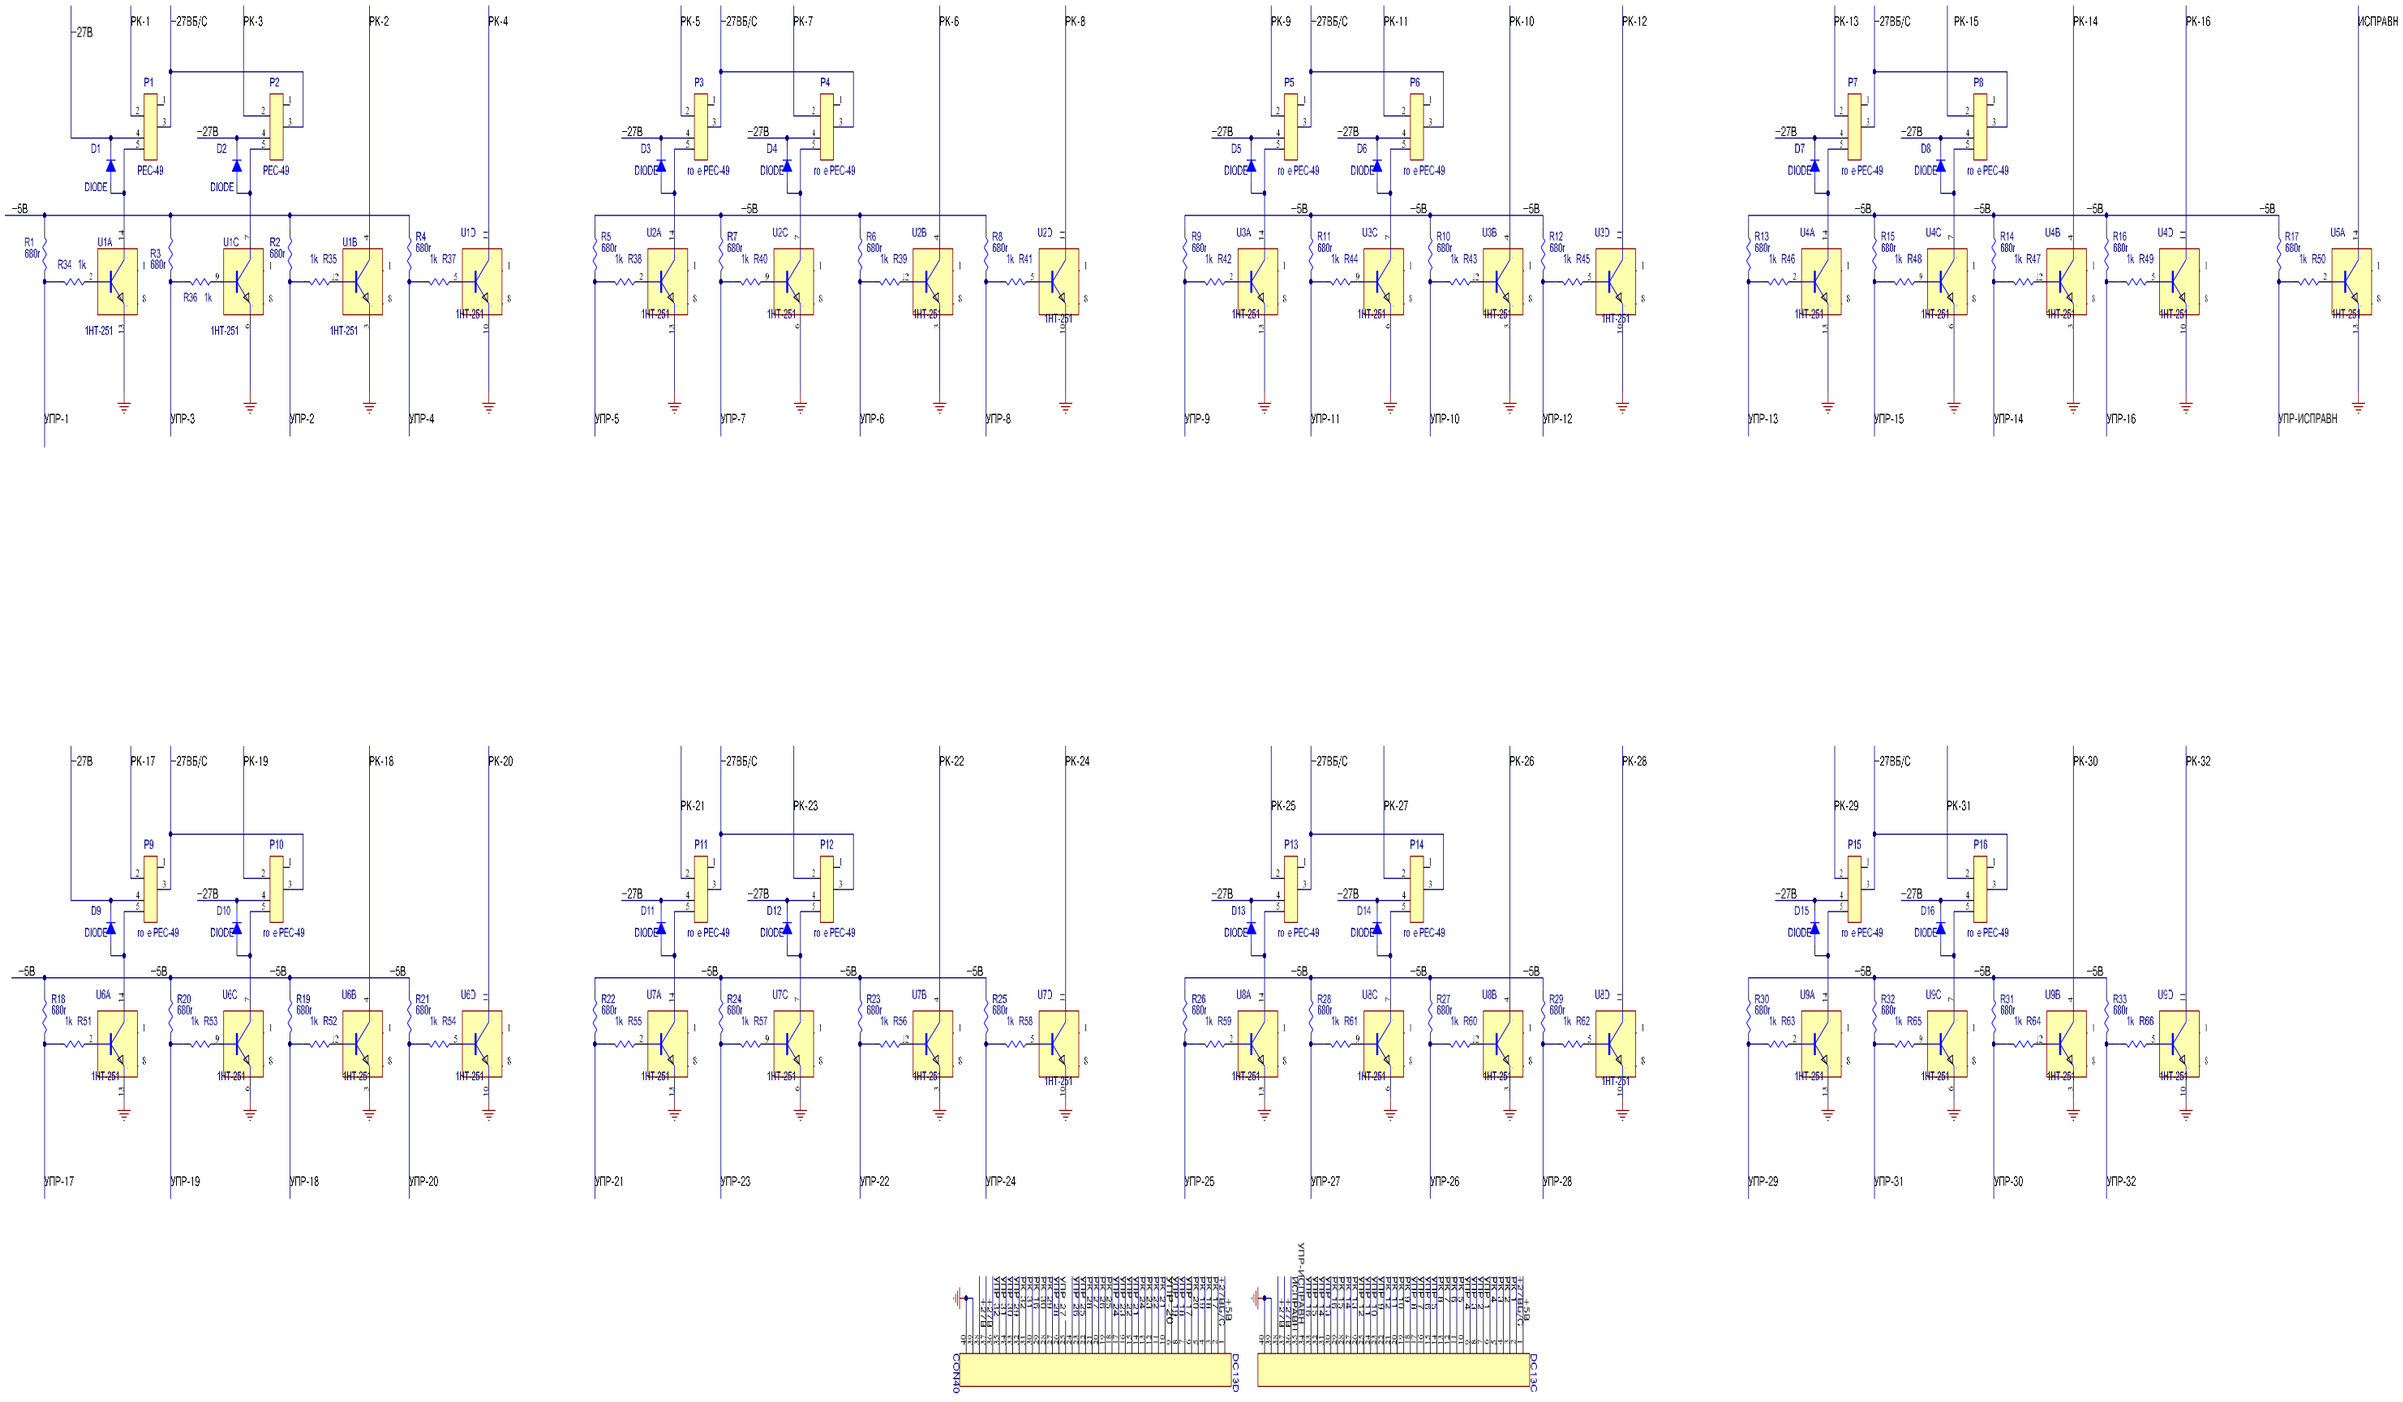

# SƠ ĐỒ NGUYÊN LÝ MẠCH ĐIỆN CỤM BIẾN ĐỔI A313_V.04



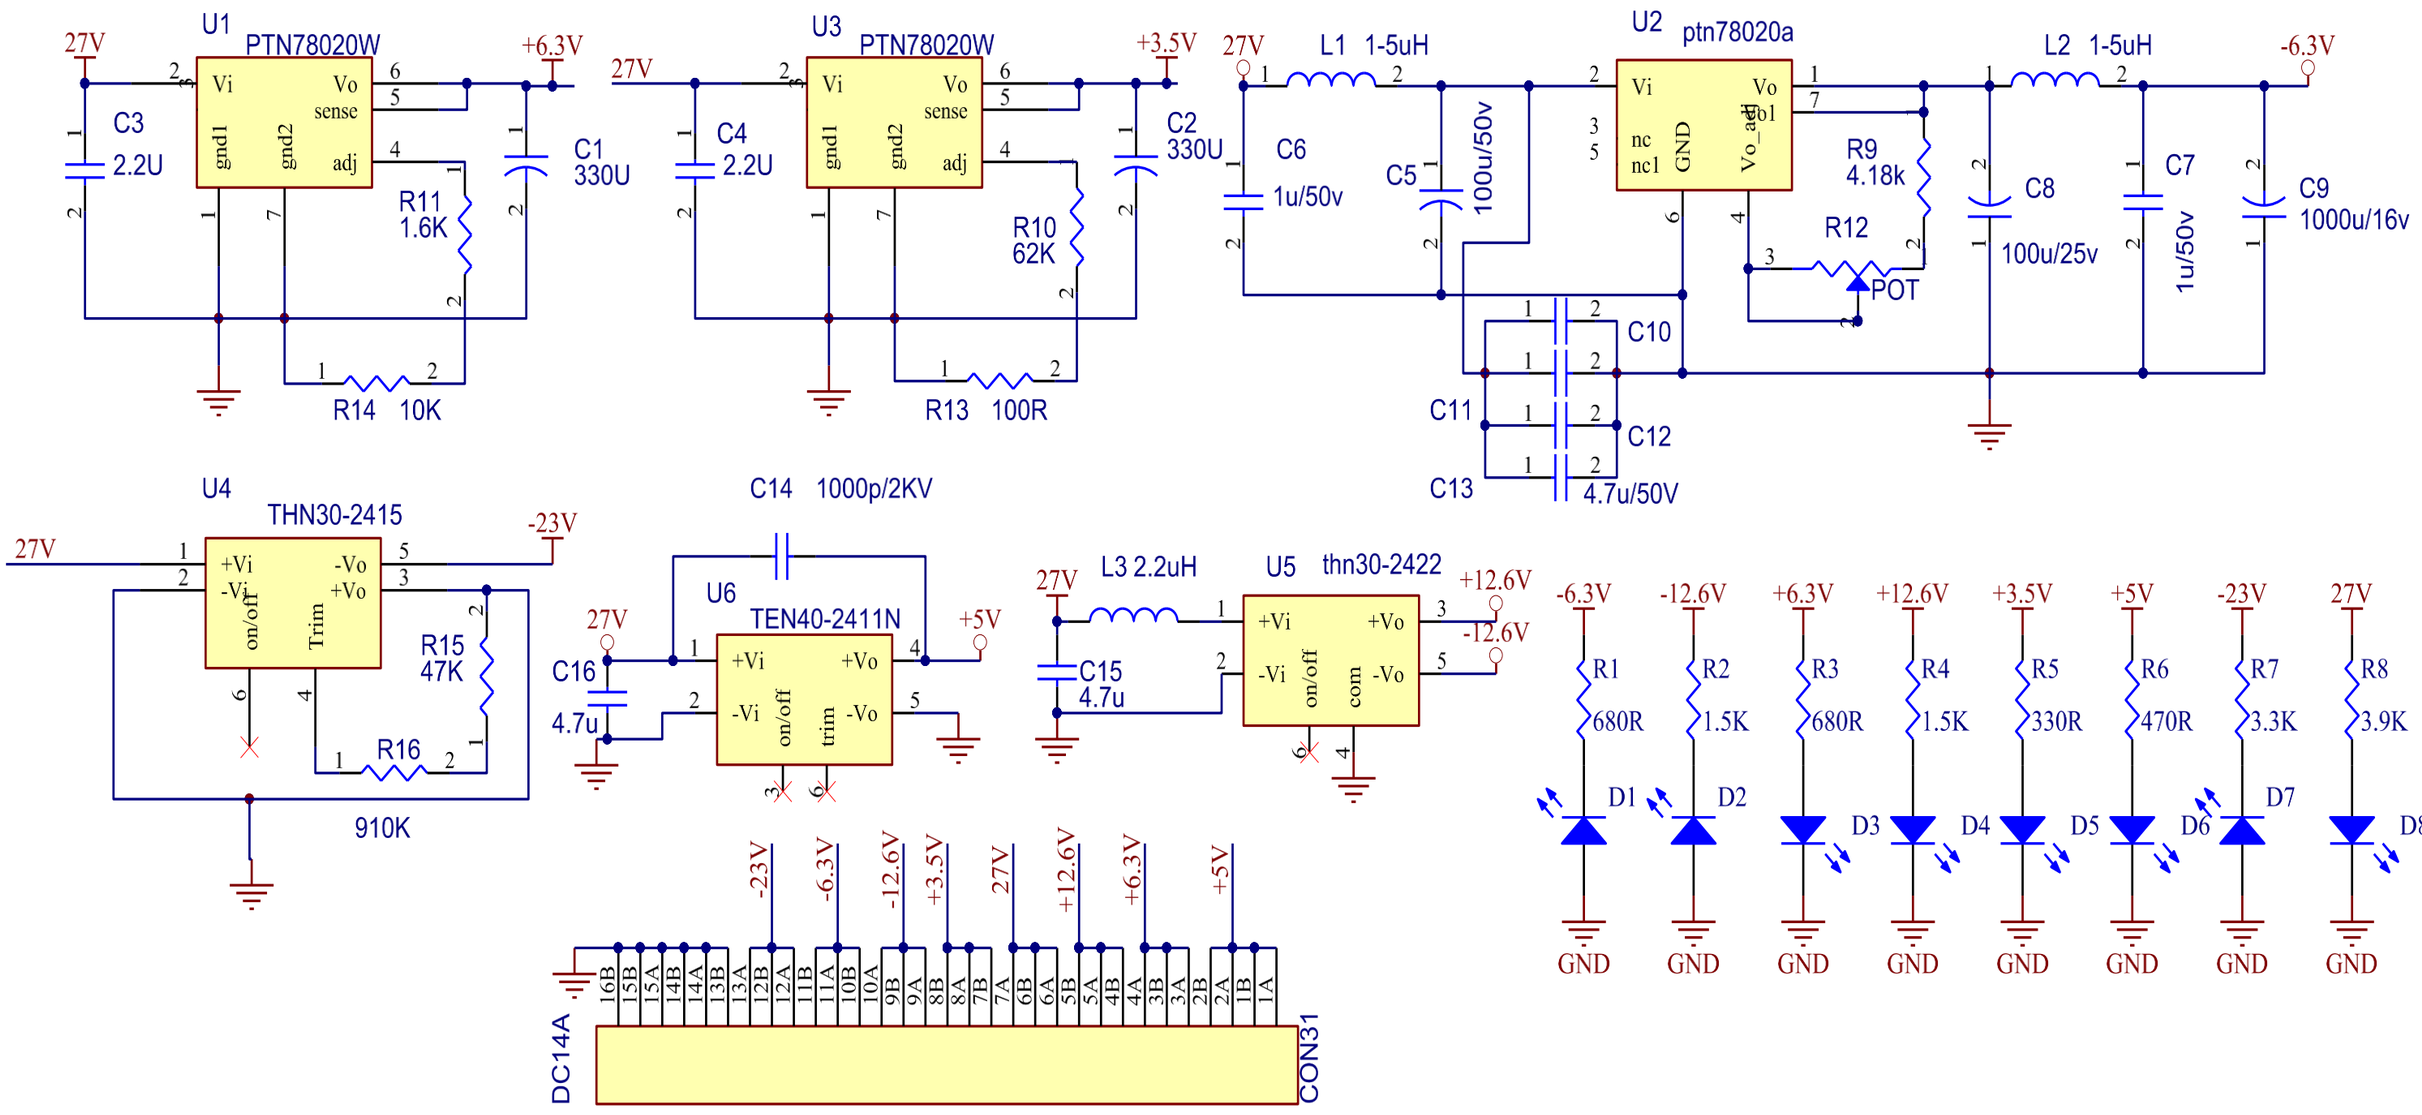

# SƠ ĐỒ NGUYÊN LÝ MẠCH ĐIỆN CỤM CHUYỂN MẠCH TÍN HIỆU RA A313_V.05



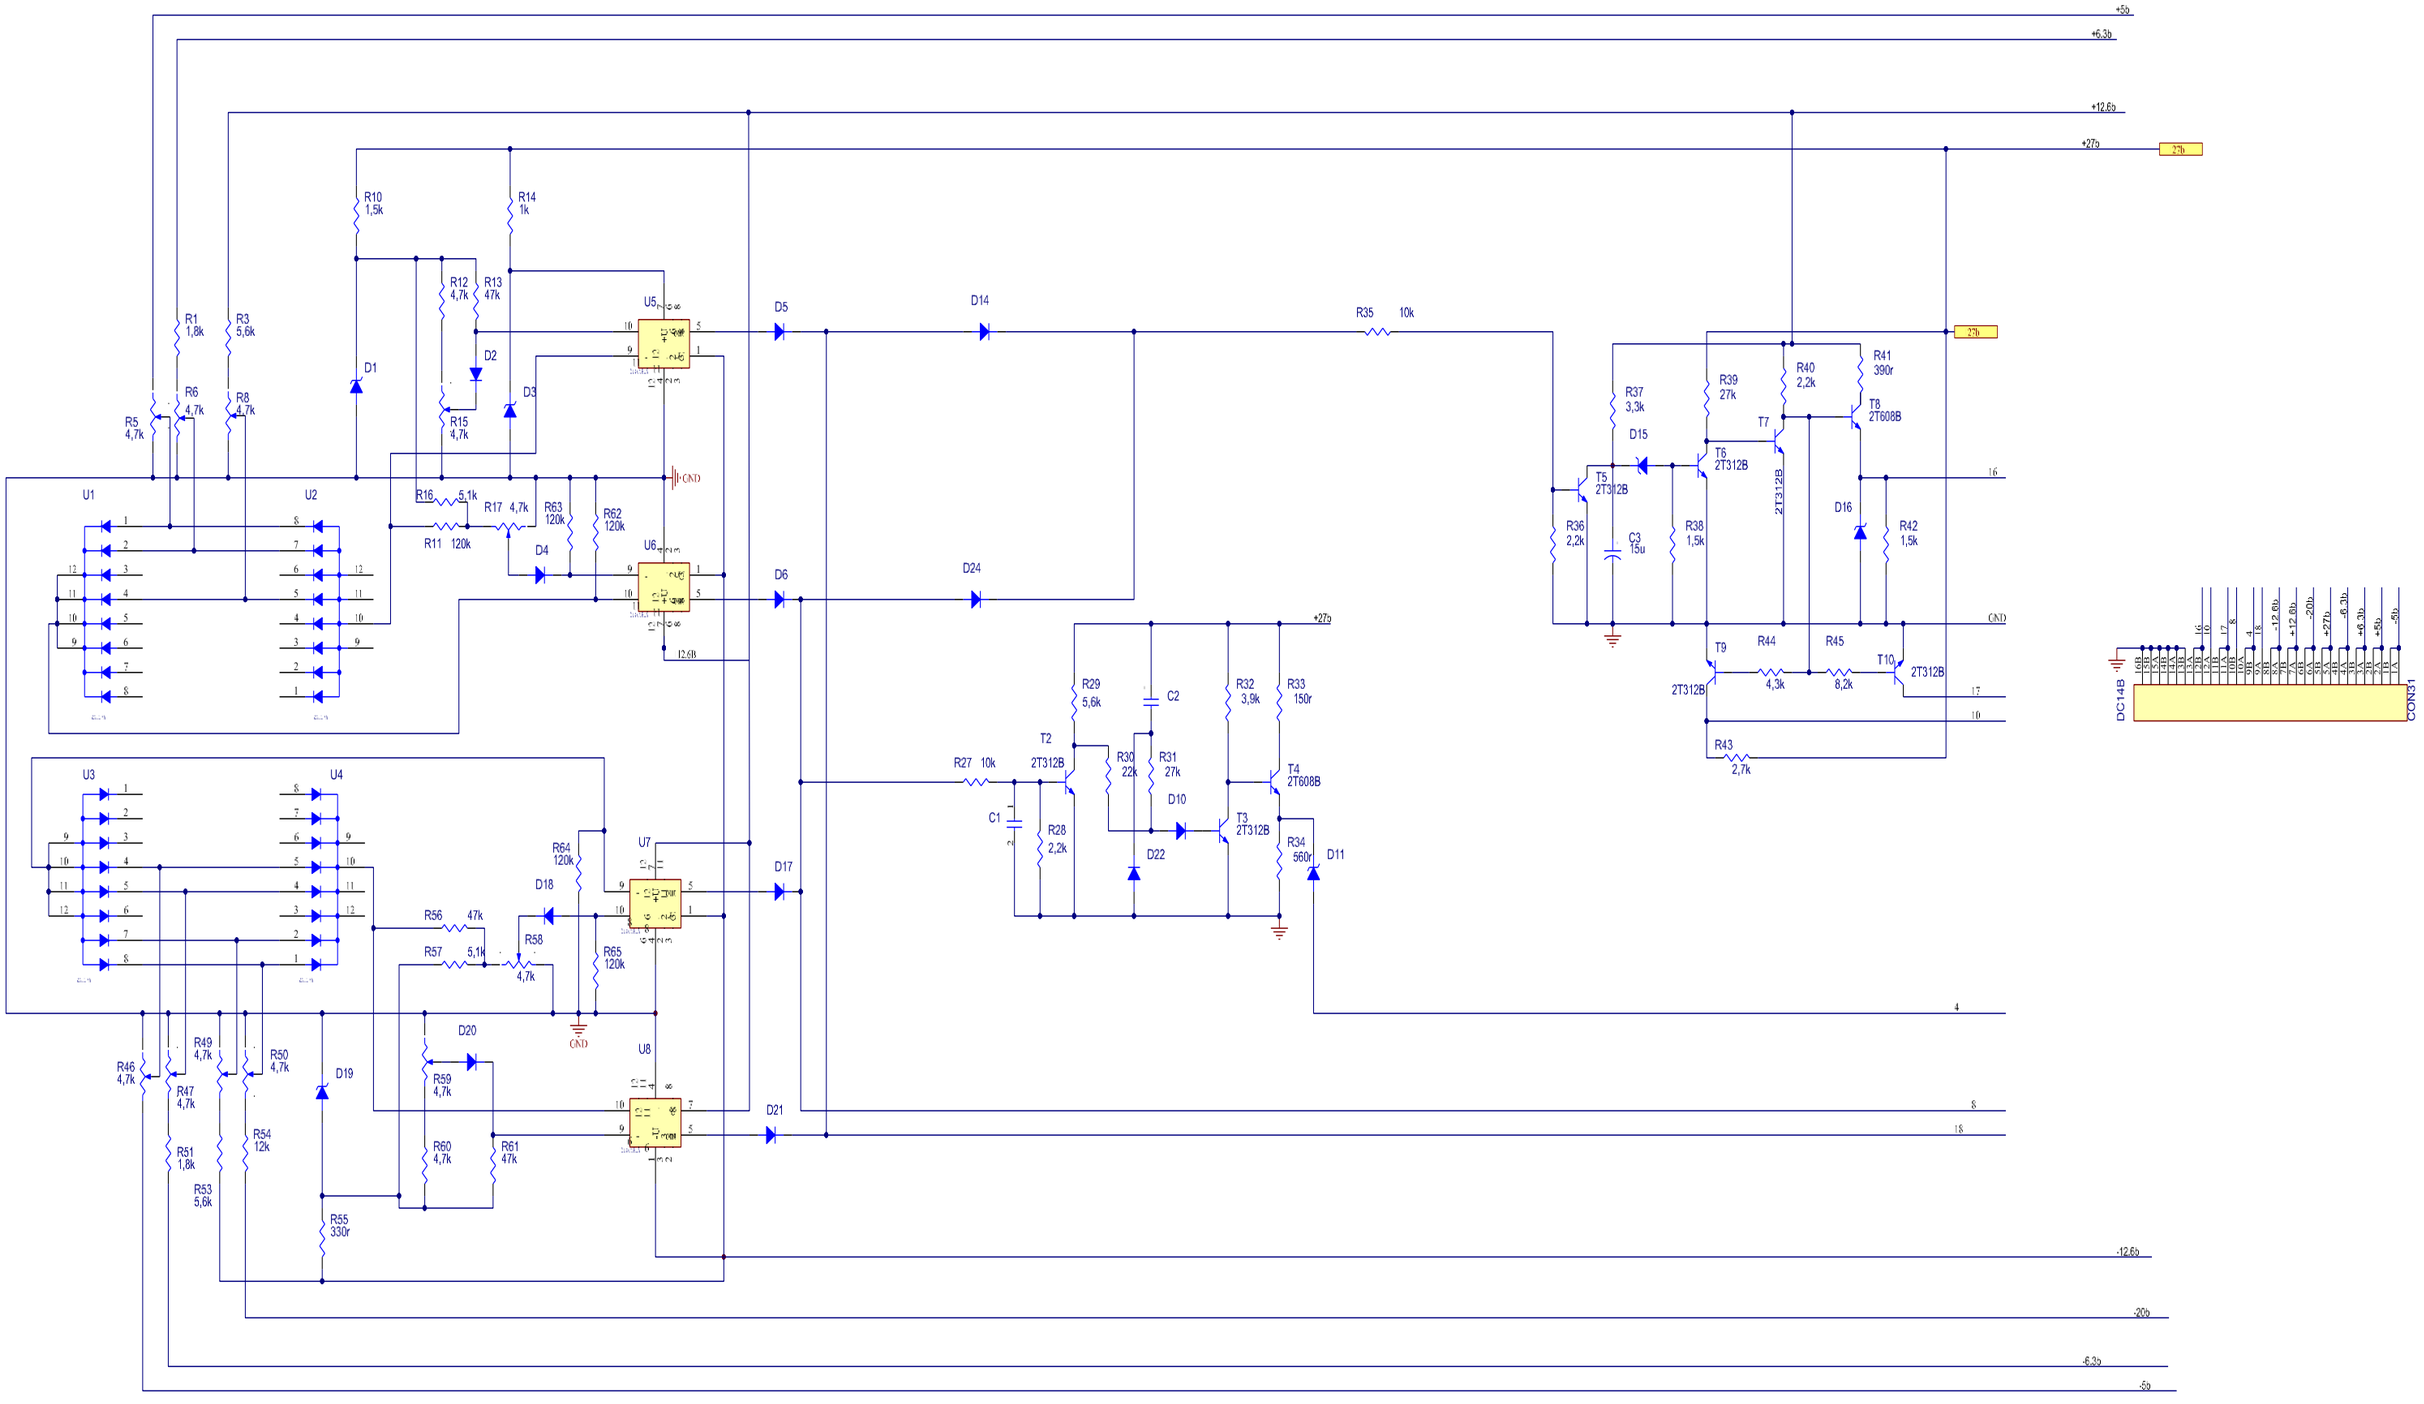

# SƠ ĐỒ NGUYÊN LÝ MẠCH ĐIỆN CỤM KHUẾCH ĐẠI TÍN HIỆU RA A313_V.06



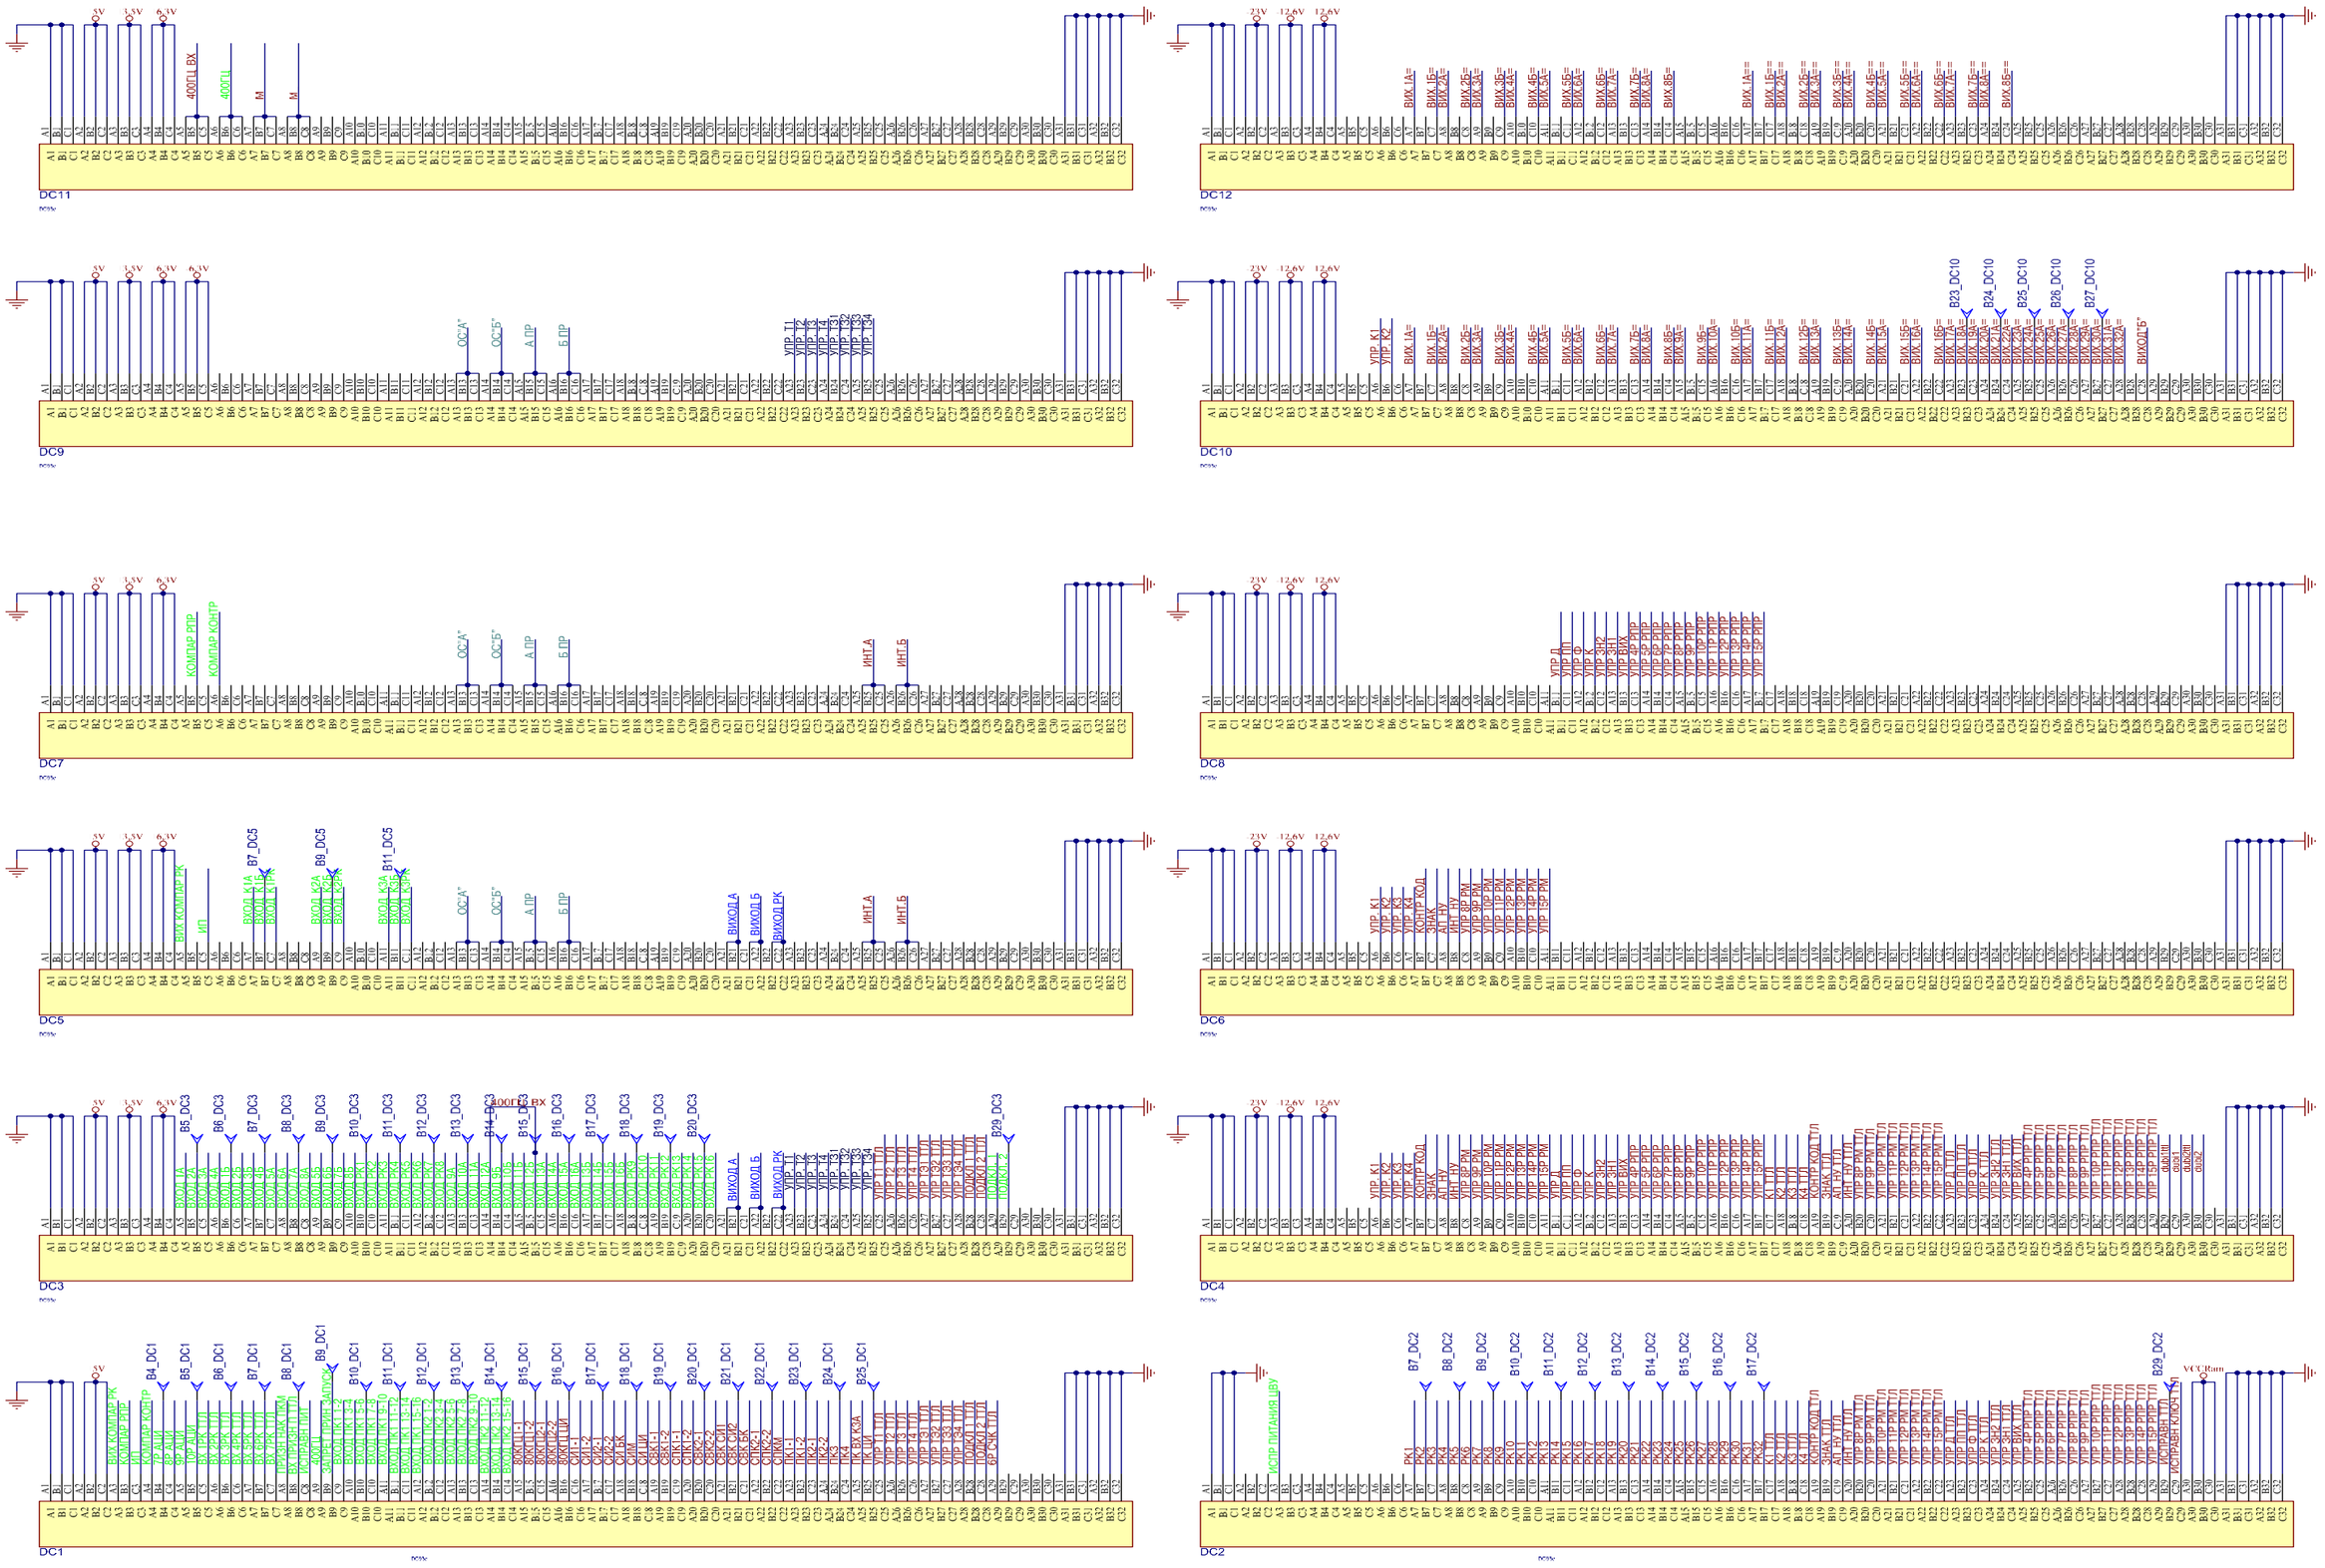

# SƠ ĐỒ NGUYÊN LÝ MẠCH ĐIỆN CỤM CHUYỂN LỆNH ĐƠN RA A313_V.07




**SƠ ĐỒ NGUYÊN LÝ MẠCH ĐIỆN CỤM NGUỒN ĐIỆN A313_V.08.01**




# SƠ ĐỒ NGUYÊN LÝ MẠCH ĐIỆN CỤM KIỂM TRA NGUỒN ĐIỆN A313_V.08.02




# SƠ ĐỒ NGUYÊN LÝ MẠCH ĐIỆN TẤM MẠCH TRUNG GIAN A313_V.09

QUÂN CHỦNG PHÒNG KHÔNG- KHÔNG QUÂN

**VIỆN KỸ THUẬT**

# TẬP SƠ ĐỒ BẢN VẼ

## Thiết bị máy tính dẫn đường A313-V

**Năm 2019**

# SƠ ĐỒ ĐẤU CẮM 31, 96 CHÂN TRÊN THÂN MÁY A313-V

