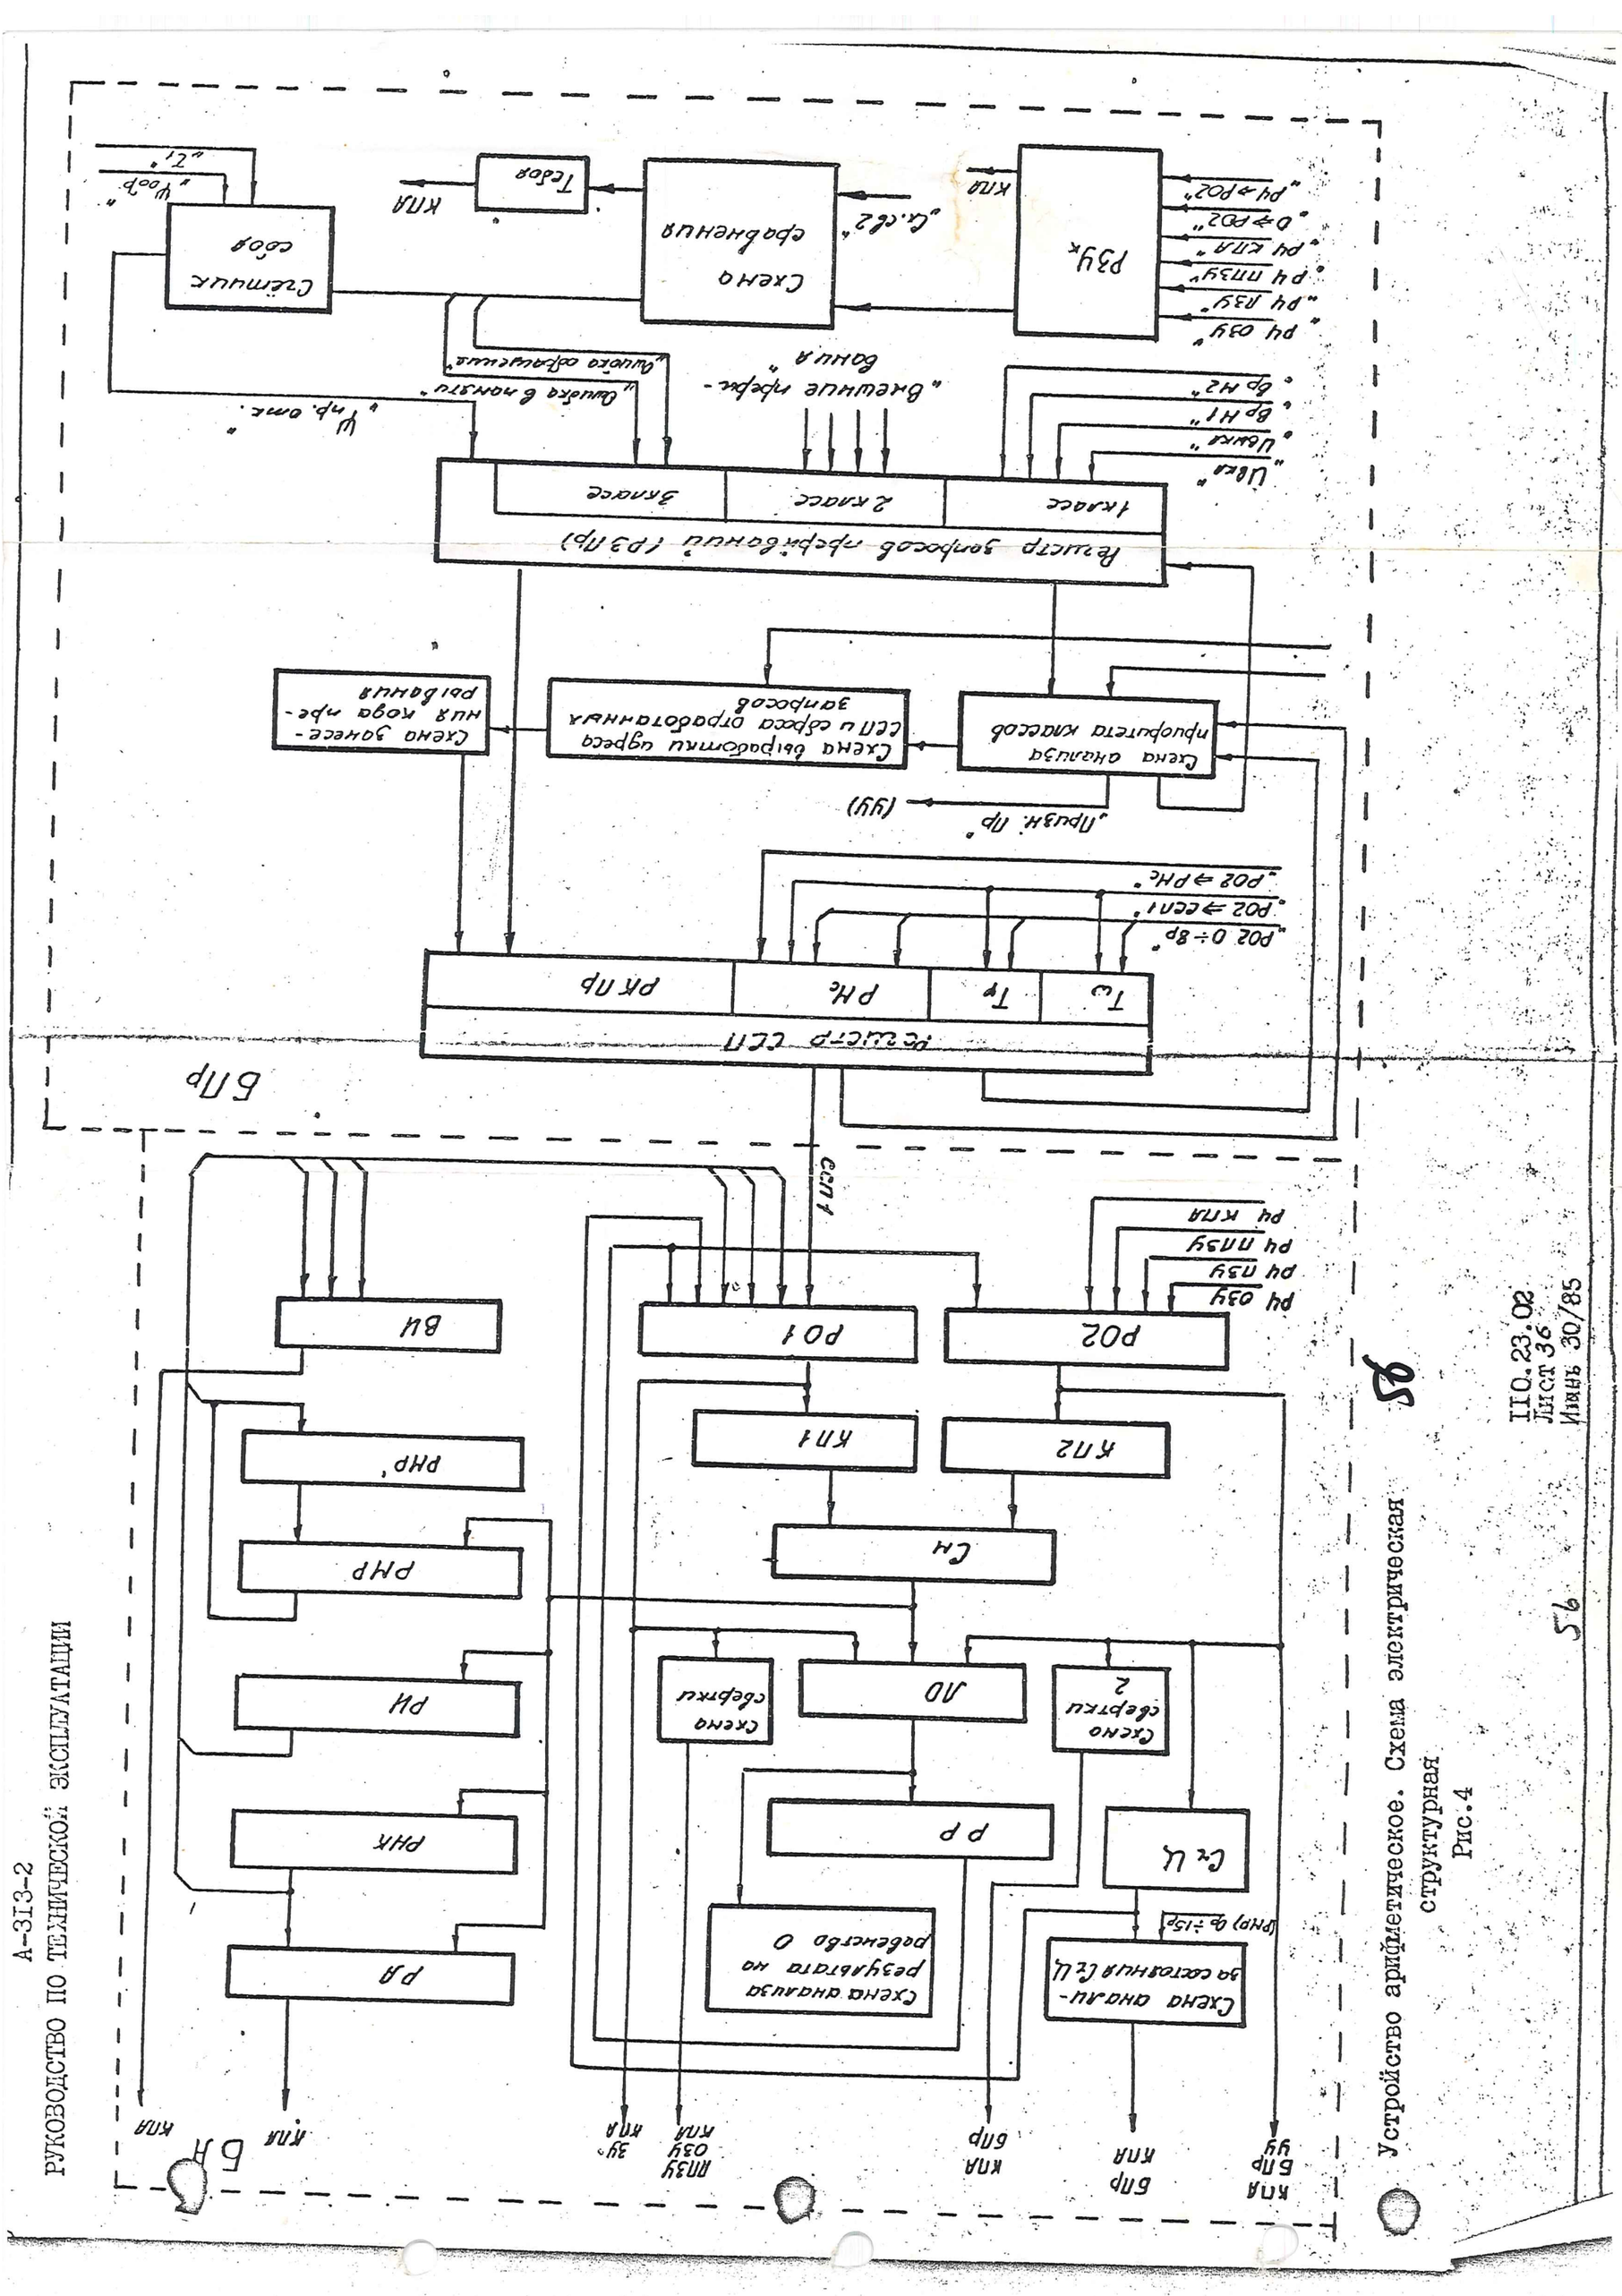


Устройство арифметическое. Схема электрическая структурная

Рис.4