
А-313
РУКОВОДСТВО ПО ТЕХНИЧЕСКОЙ ЭКСПЛУАТАЦИИ


1. Соединительные жгуты изготавливаются машиностроительным заводом по данным настоящей схемы. Марка провода выбирается машиностроительной организацией.
2. Провода скрученные (витая пара 0,2 - 0,35 мм^2, шаг витка 40 - 50 мм). Один из скрученных проводов распаивается с обоих концов к конт. "корпус".

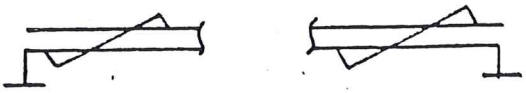

3. Корпуса всех блоков должны быть соединены с корпусом объекта ("металлизированный"). Переходное сопротивление - не более $2 \cdot 10^{-3}$ Ом.
4. Соединение блоков А-313-1, А-313-2, А-313-3 между собой, входящих в состав устройства вычислительного ЕУ3.048.004, осуществляется согласно ЕУ3.049.004 Э4 кабелями ЕУ4.855.904 и ЕУ4.855.905.
5. Габаритные размеры и внешний вид блоков даны в ЕУ1.247.199 ГЧ.
6. Кабельные и блочные части разъемов маркируются согласно настоящей схеме (графа 1 таблицы) заводом-изготовителем аппаратуры при комплектовании системы. Место и способ маркировки по усмотрению завода-изготовителя аппаратуры.
7. Экраны проводов распаивать на конт. "корпус" съемных частей разъемов. Заземление конт. "корпус", показанное на чертеже, осуществлять распаиванием на этот контакт плетенки ПМЛ2х4, которую соединить с корпусом объекта.
8. Подключение бортовых систем к разъему 3Ш3 осуществляется экранированным проводом сечением 0,35. Подключение бортовых систем к разъемам 3Ш4В, 6Ш1 (конт. 13 - 26) осуществляется витой парой (см. п. 2). Подключение систем к разъемам 3Ш3В, 3Ш4 (кроме конт. 36 - 45, 62, подключаемых к системам "витой парой", см. п. 2), осуществляется неэкранированным проводом сечением 0,35.
9. Длина жгута 10 не должна превышать 1 м.
10. Подключение сопряженных систем бортового оборудования производится по схеме, согласованной с предприятием-разработчиком на основании схем связи.
11. Для комплектации ЕУ1.247.199-01 конт. 1 - 14 разъема 8Ш2 подключаются параллельно одноименным контактам разъема 7Ш2 блока А-313-7 конт. 8Ш2/15 блока А-313-7 (сигнал "Подкл.коммут.") подключается к 3Ш3/66 блока А-313-3.
12. А-313-12 (устройство защиты) размещается на раме ЕУ4.138.495.
13. Параметры жгутовой схемы объекта должны обеспечивать падение напряжения от энергоузла до блока А-313-12 не более 0,8 В по бортсети 27 В.

АППАРАТУРА А-313. СХЕМА ЭЛЕКТРИЧЕСКАЯ СОЕДИНЕНИЙ КОМПЛЕКТАЦИЙ ЕУ1.247.199 Э4, ЕУ1.247.199-01 Э4, ЕУ1.247.199-02 Э4, ЕУ1.247.199-08 Э4

Рис. 1 (лист 1 из 2)

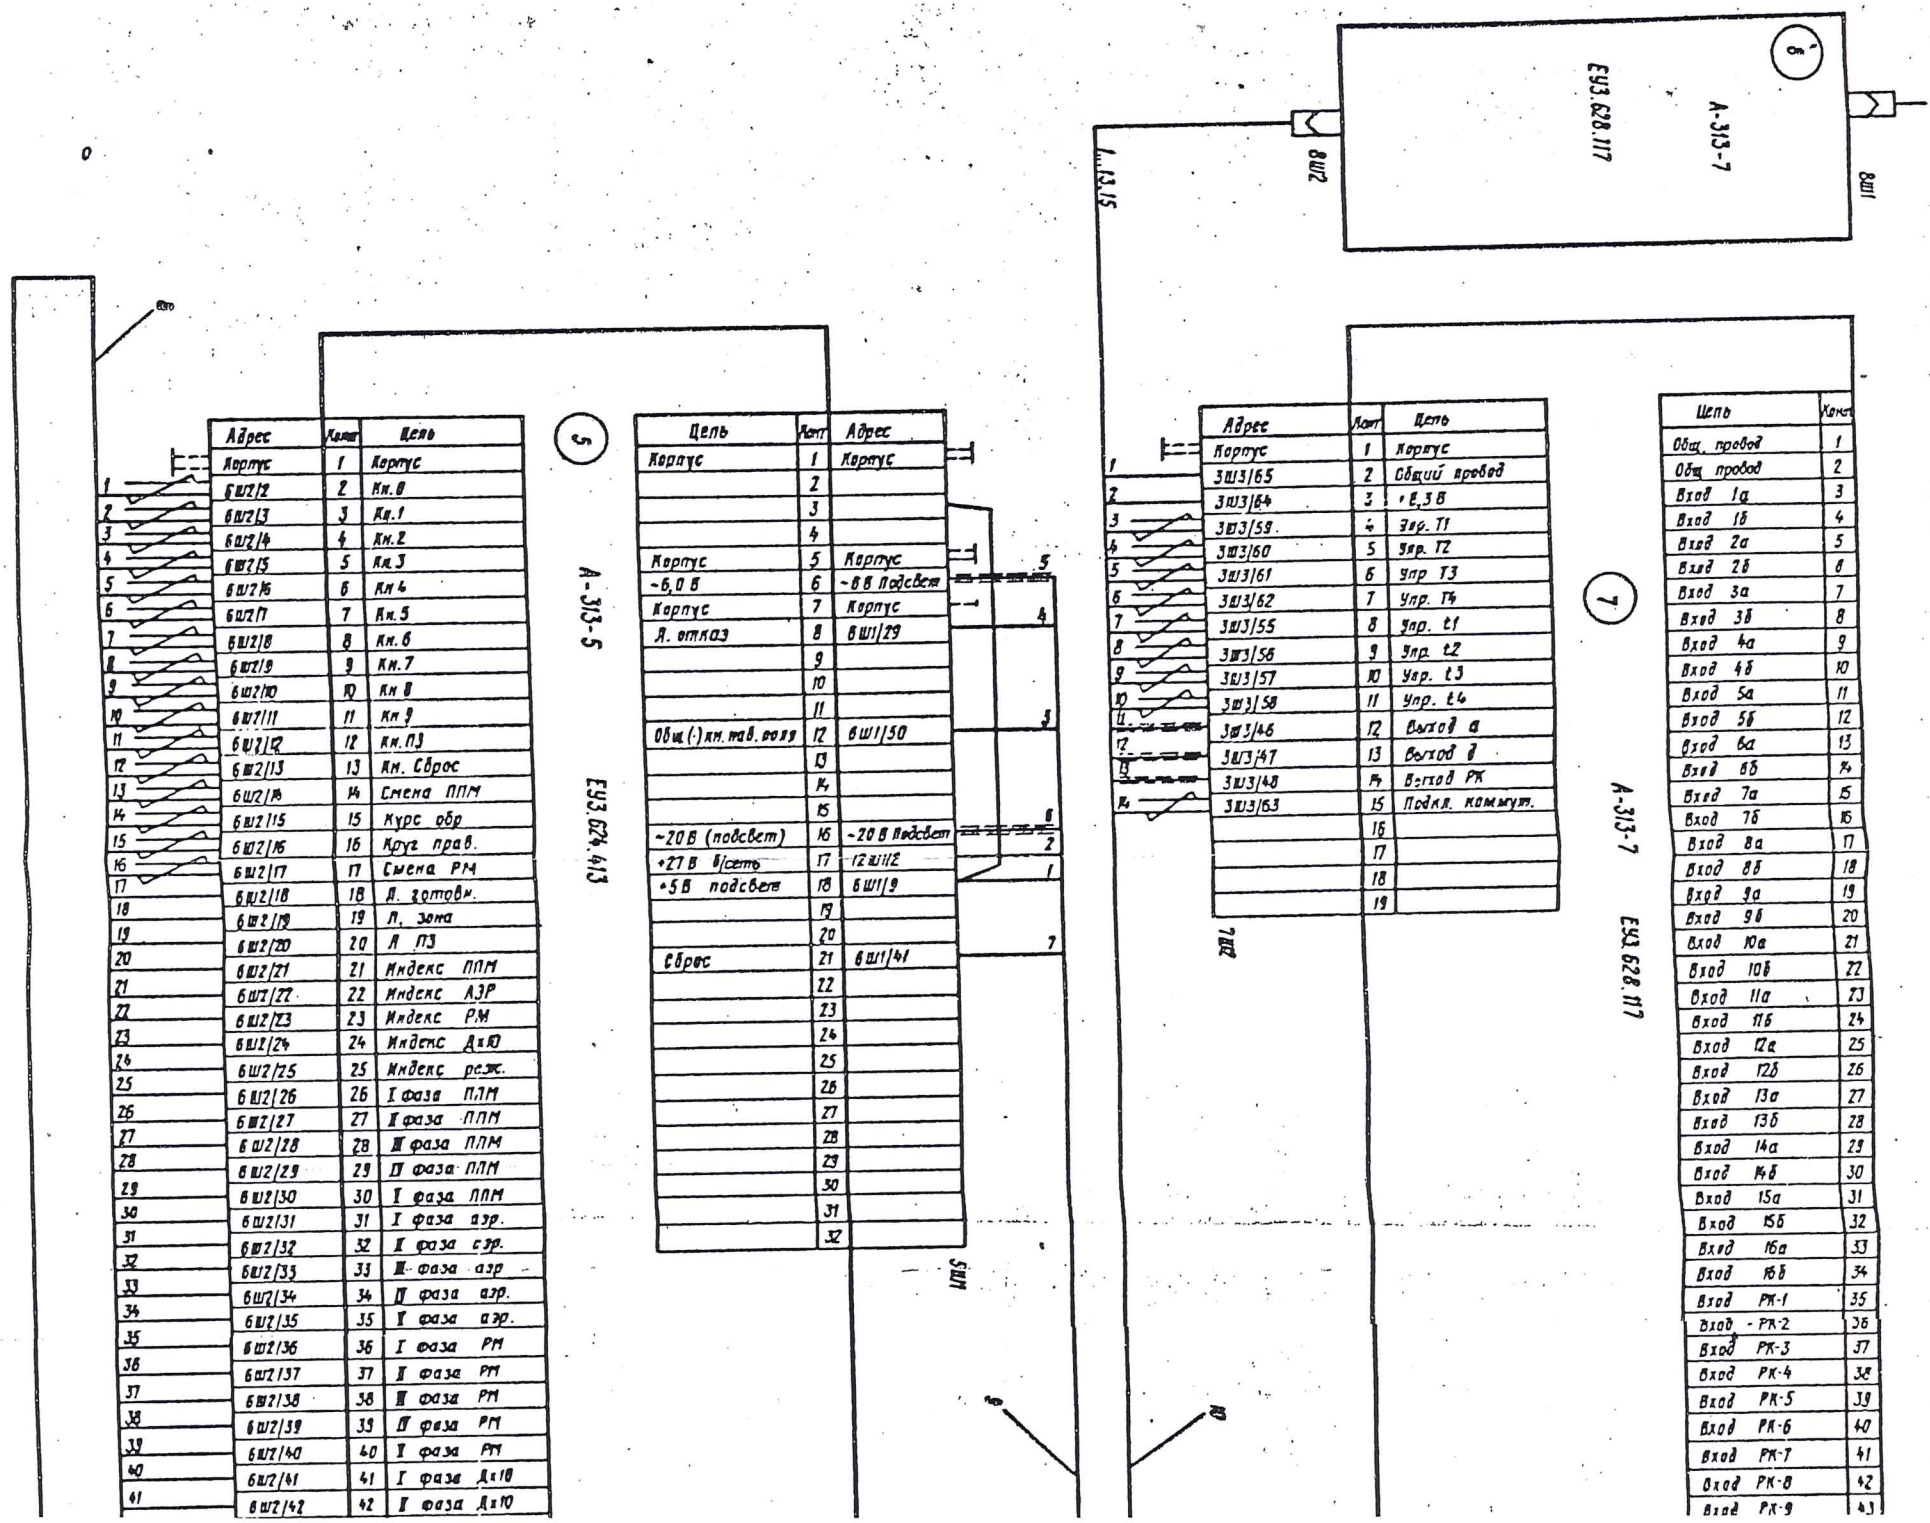
6
А-313-7
ЕУ3.628.117
6Ш2
6Ш1
1...13,15
5
А-313-5
ЕУ3.624.413
7
А-313-7
ЕУ3.628.117
5Ш1
7Ш2
Адрес | Конт | Цепь
Корпус | 1 | Корпус
6Ш2/2 | 2 | Кн.0
6Ш2/3 | 3 | Кн.1
6Ш2/4 | 4 | Кн.2
6Ш2/5 | 5 | Кн.3
6Ш2/6 | 6 | Кн.4
6Ш2/7 | 7 | Кн.5
6Ш2/8 | 8 | Кн.6
6Ш2/9 | 9 | Кн.7
6Ш2/10 | 10 | Кн.8
6Ш2/11 | 11 | Кн.9
6Ш2/12 | 12 | Кн.ПЗ
6Ш2/13 | 13 | Кн. Сброс
6Ш2/14 | 14 | Смена ППМ
6Ш2/15 | 15 | Курс обр
6Ш2/16 | 16 | Круг прав.
6Ш2/17 | 17 | Смена РМ
6Ш2/18 | 18 | Д. готов.
6Ш2/19 | 19 | Л. зона
6Ш2/20 | 20 | А ПЗ
6Ш2/21 | 21 | Индекс ППМ
6Ш2/22 | 22 | Индекс АЗР
6Ш2/23 | 23 | Индекс РМ
6Ш2/24 | 24 | Индекс Дх10
6Ш2/25 | 25 | Индекс реж.
6Ш2/26 | 26 | I фаза ППМ
6Ш2/27 | 27 | II фаза ППМ
6Ш2/28 | 28 | III фаза ППМ
6Ш2/29 | 29 | IV фаза ППМ
6Ш2/30 | 30 | I фаза ППМ
6Ш2/31 | 31 | I фаза азр.
6Ш2/32 | 32 | II фаза азр.
6Ш2/33 | 33 | III фаза азр.
6Ш2/34 | 34 | IV фаза азр.
6Ш2/35 | 35 | V фаза азр.
6Ш2/36 | 36 | I фаза РМ
6Ш2/37 | 37 | II фаза РМ
6Ш2/38 | 38 | III фаза РМ
6Ш2/39 | 39 | IV фаза РМ
6Ш2/40 | 40 | V фаза РМ
6Ш2/41 | 41 | I фаза Дх10
6Ш2/42 | 42 | II фаза Дх10
Цепь | Конт | Адрес
Корпус | 1 | Корпус
Корпус | 5 | Корпус
-6,0 В | 6 | -6 В подсвет
Корпус | 7 | Корпус
А. отказ | 8 | 6Ш1/29
Общ.(-) кн. тав. возд | 12 | 6Ш1/50
-20 В (подсвет) | 16 | -20 В подсвет
+27 В б/сеть | 17 | 12 и 12
+5 В подсвет | 18 | 6Ш1/9
Сброс | 21 | 6Ш1/41
Адрес | Конт | Цепь
Корпус | 1 | Корпус
ЗШ3/65 | 2 | Общий провод
ЗШ3/64 | 3 | +6,3 В
ЗШ3/59 | 4 | Упр. Т1
ЗШ3/60 | 5 | Упр. Т2
ЗШ3/61 | 6 | Упр Т3
ЗШ3/62 | 7 | Упр. Т4
ЗШ3/55 | 8 | Упр. t1
ЗШ3/56 | 9 | Упр. t2
ЗШ3/57 | 10 | Упр. t3
ЗШ3/58 | 11 | Упр. t4
ЗШ3/46 | 12 | Выход а
ЗШ3/47 | 13 | Выход д
ЗШ3/48 | 14 | Выход РК
ЗШ3/63 | 15 | Подкл. комнут.
Цепь | Конт
Общ. провод | 1
Общ. провод | 2
Вход 1а | 3
Вход 1б | 4
Вход 2а | 5
Вход 2б | 6
Вход 3а | 7
Вход 3б | 8
Вход 4а | 9
Вход 4б | 10
Вход 5а | 11
Вход 5б | 12
Вход 6а | 13
Вход 6б | 14
Вход 7а | 15
Вход 7б | 16
Вход 8а | 17
Вход 8б | 18
Вход 9а | 19
Вход 9б | 20
Вход 10а | 21
Вход 10б | 22
Вход 11а | 23
Вход 11б | 24
Вход 12а | 25
Вход 12б | 26
Вход 13а | 27
Вход 13б | 28
Вход 14а | 29
Вход 14б | 30
Вход 15а | 31
Вход 15б | 32
Вход 16а | 33
Вход 16б | 34
Вход РК-1 | 35
Вход РК-2 | 36
Вход РК-3 | 37
Вход РК-4 | 38
Вход РК-5 | 39
Вход РК-6 | 40
Вход РК-7 | 41
Вход РК-8 | 42
Вход РК-9 | 43

Поз. обозначение	Разъем			Место установки разъема		Номер комплектации
	Со стороны блока обозначение	Со стороны кабеля обозначение	Технические условия	Номер блока	Наименование	
1	2	3	4	5	6	7
3Ш3В 3Ш3	Вилка РПКМ3 67/67 Н1-В	Розетка РПКМ3 67/67 Г1-В	АВО.364.040 ТУ	3	А-313-3	ЕУ1.247.199 ЕУ1.247.199-01 ЕУ1.247.199-02 ЕУ1.247.199-08
3Ш4В 3Ш4	Вилка РПКМ3 67/67 Н1-В	Розетка РПКМ3 67/67 Г1-В	АВО.364.040 ТУ	3		
5Ш1	Вилка ОС 2РМДТ33КПН32Ш5В1-В	Розетка ОС 2РМДТ33БПН32Г5В1-В	ГВО.364.127 ТУ 6РО.364.045 ТУ	5	А-313-5	ЕУ1.247.199-01 ЕУ1.247.199-02
5Ш2	Вилка ОС 2РМДТ45КПН50Ш8В1-В	Розетка ОС 2РМДТ45БПН50Г8В1-В	ГВО.364.126 ТУ 6РО.364.045 ТУ	5		
6Ш1	Вилка ОС 2РМДТ45КПН50Ш8В1-В	Розетка ОС 2РМДТ45БПН50Г8В1-В	ГВО.364.126 ТУ 6РО.364.045 ТУ	6	А-313-6	ЕУ1.247.199 ЕУ1.247.199-01 ЕУ1.247.199-02 ЕУ1.247.199-08
6Ш2	Вилка ОС 2РМДТ45КПН50Г8В1-В	Вилка ОС 2РМДТ45БПН50Ш8В1-В	ГВО.364.126 ТУ 6РО.364.045 ТУ	6		
7Ш1	Вилка ОС 2РМДТ45КПН50Ш8В1-В	Розетка ОС 2РМДТ45БПН50Г8В1-В	ГВО.364.126 ТУ 6РО.364.045 ТУ	7	А-313-7	ЕУ1.247.199-01 ЕУ1.247.199-02
7Ш2	Вилка ОС 2РМДТ27КПН19Ш5В1-В	Розетка ОС 2РМДТ27БПН19Г5В1-В	ГВО.364.126 ТУ 6РО.364.045 ТУ	7		
8Ш1	Вилка ОС 2РМДТ45КПН50Ш8В1-В	Розетка ОС 2РМДТ45БПН50Г8В1-В	ГВО.364.126 ТУ 6РО.364.045 ТУ	8	А-313-7	ЕУ1.247.199-01
8Ш2	Вилка ОС 2РМДТ27КПН19Ш5В1-В	Розетка ОС 2РМДТ27БПН19Г5В1-В	ГВО.364.126 ТУ 6РО.364.045 ТУ	8		
12Ш1	Вилка ОС 2РМДТ27КПН19Ш5В1-В	Розетка ОС 2РМДТ27БПН19Г5В1-В	ГВО.364.126 ТУ 6РО.364.045 ТУ	12	А-313-12	ЕУ1.247.199 ЕУ1.247.199-01 ЕУ1.247.199-02 ЕУ1.247.199-08

Наименование	Шифр	Обозначение	Количество			
			ЕУ1.247.199	ЕУ1.247.199-01	ЕУ1.247.199-02	ЕУ1.247.199-08
			Др-15	ВТ-15	РБ-15	ДР-15-01
1. Полупостоянное запоминающее устройство	А-313-1	ЕУ1.061.057	1	1	1	1
2. Цифровое вычислительное устройство	А-313-2	Е13.031.009	1	1	1	1
3. Устройство ввода-вывода и питания	А-313-3	ЕУ3.048.002	1	1	1	1
4. Пульт управления	А-313-5	ЕУ3.628.413	-	1	1	-
5. Пульт оператора	А-313-6	ЕУ3.624.414	1	1	1	1
6. Блок входного коммутатора	А-313-7	ЕУ3.628.117	-	2	1	-
7. Устройство защиты	А-313-12	ЕУ3.229.063	1	1	1	1
8. Кабель	4.855.908	ЕУ4.855.908	1	1	1	1
9. Кабель	4.855.905	ЕУ4.855.905	1	1	1	1

Условные обозначения проводов


- 0,35


- 0,35 (экранированный)


- плоский ПМЛ2х4


- витая пара (см. п. 2)

1340/2