/176

А-313
РУКОВОДСТВО ПО ТЕХНИЧЕСКОЙ ЭКСПЛУАТАЦИИ

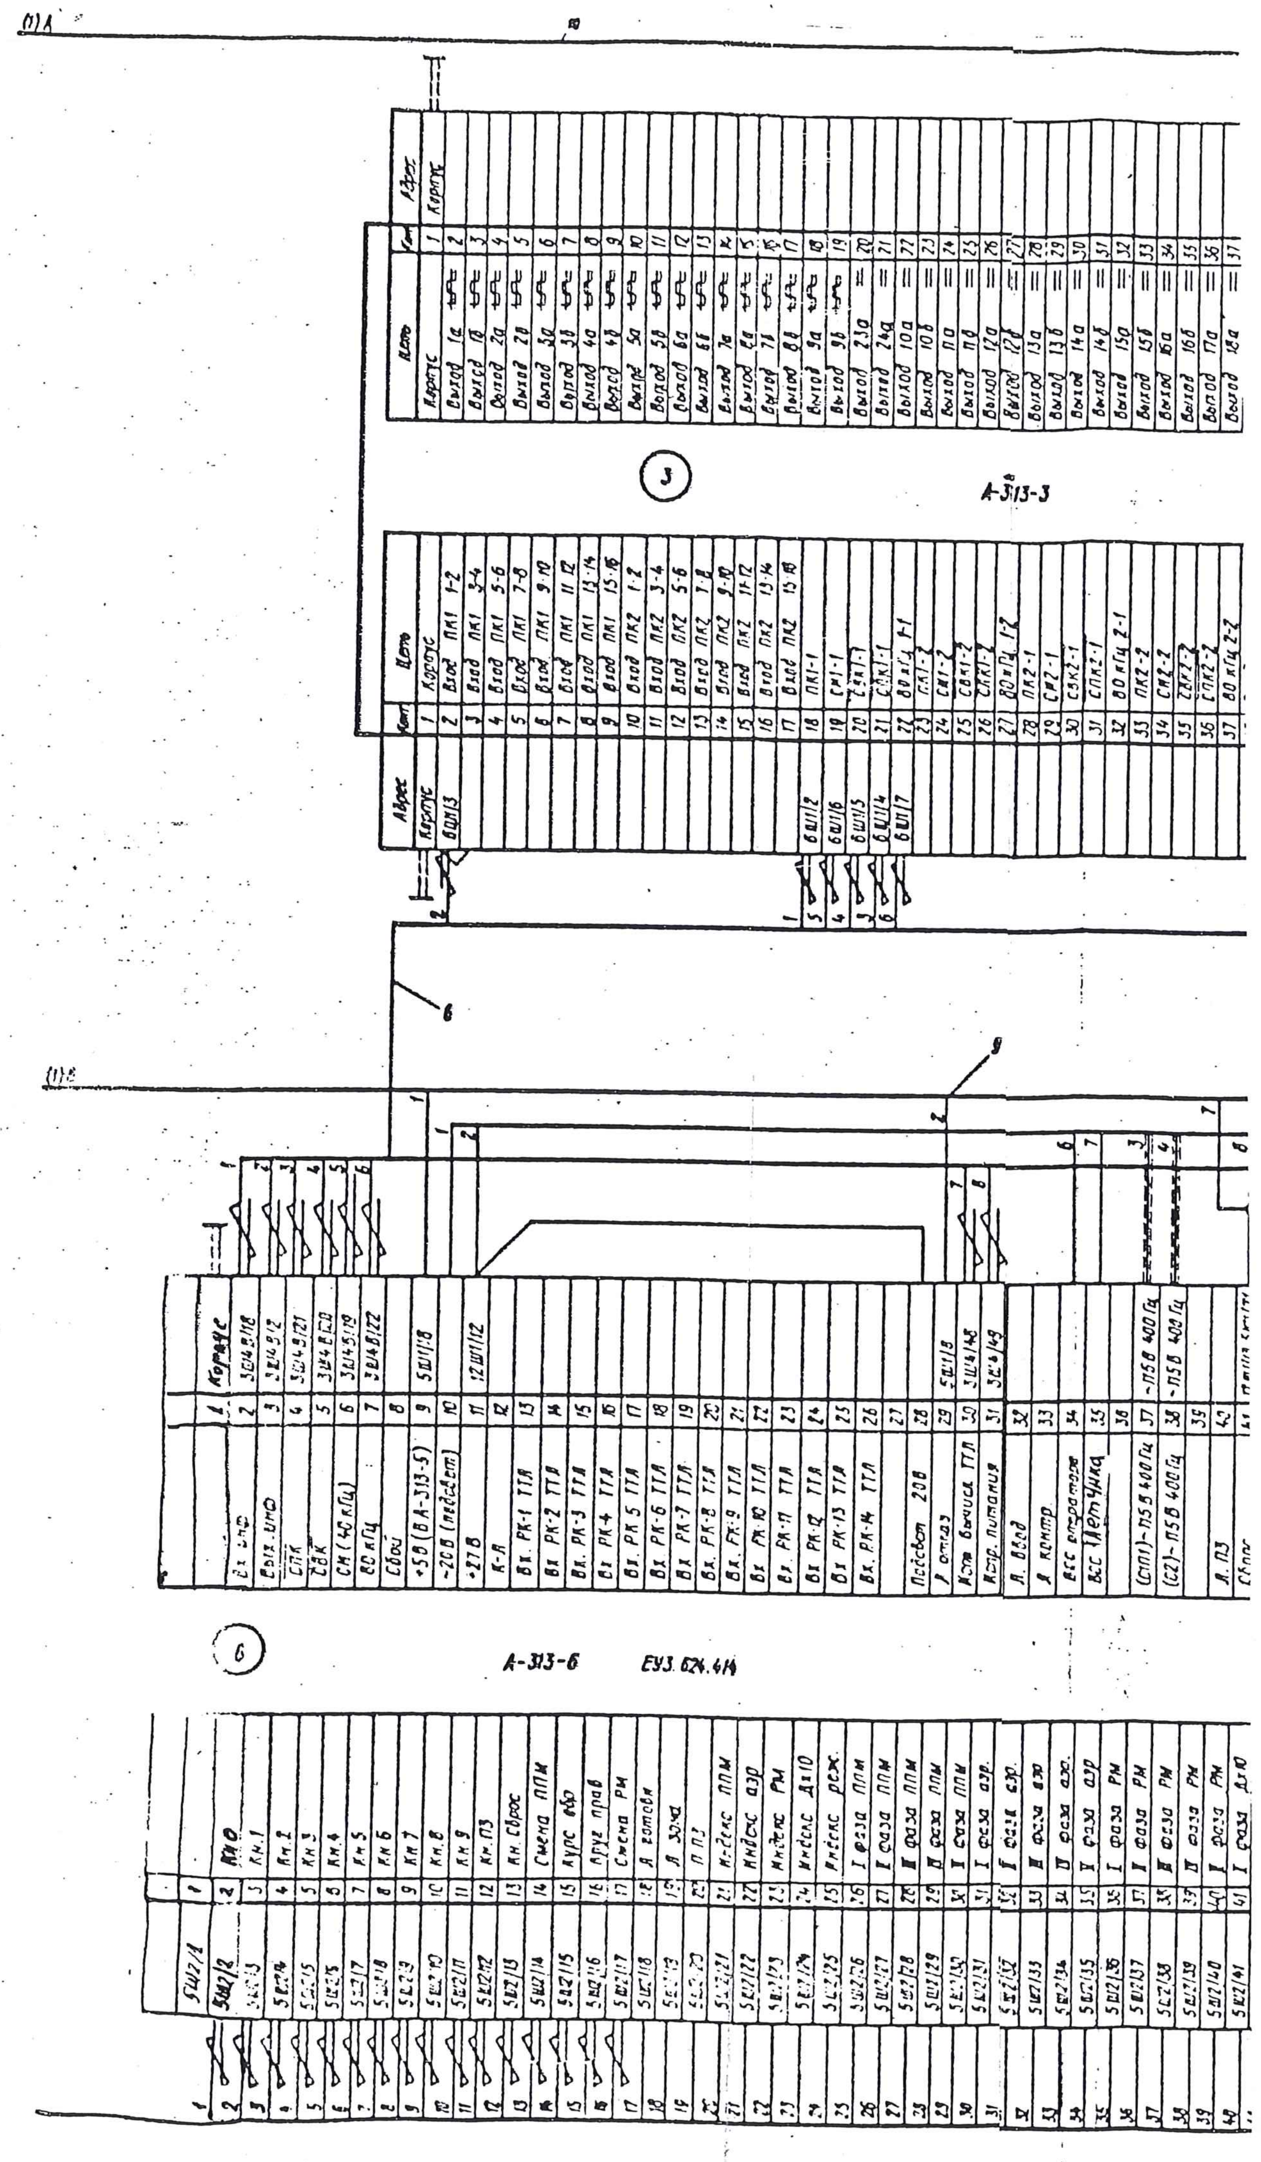

АППАРАТУРА А-313. СХЕМА ЭЛЕКТРИЧЕСКАЯ СОЕДИНЕНИЙ КОМПЛЕКТАЦИЙ ЕУ1.247.199 ЭЗ, ЕУ1.247.199-01 ЭЗ, ЕУ1.247.199-02 ЭЗ, ЕУ1.247.199-08 ЭЗ

Рис. 1 (лист 2 из 2)

131

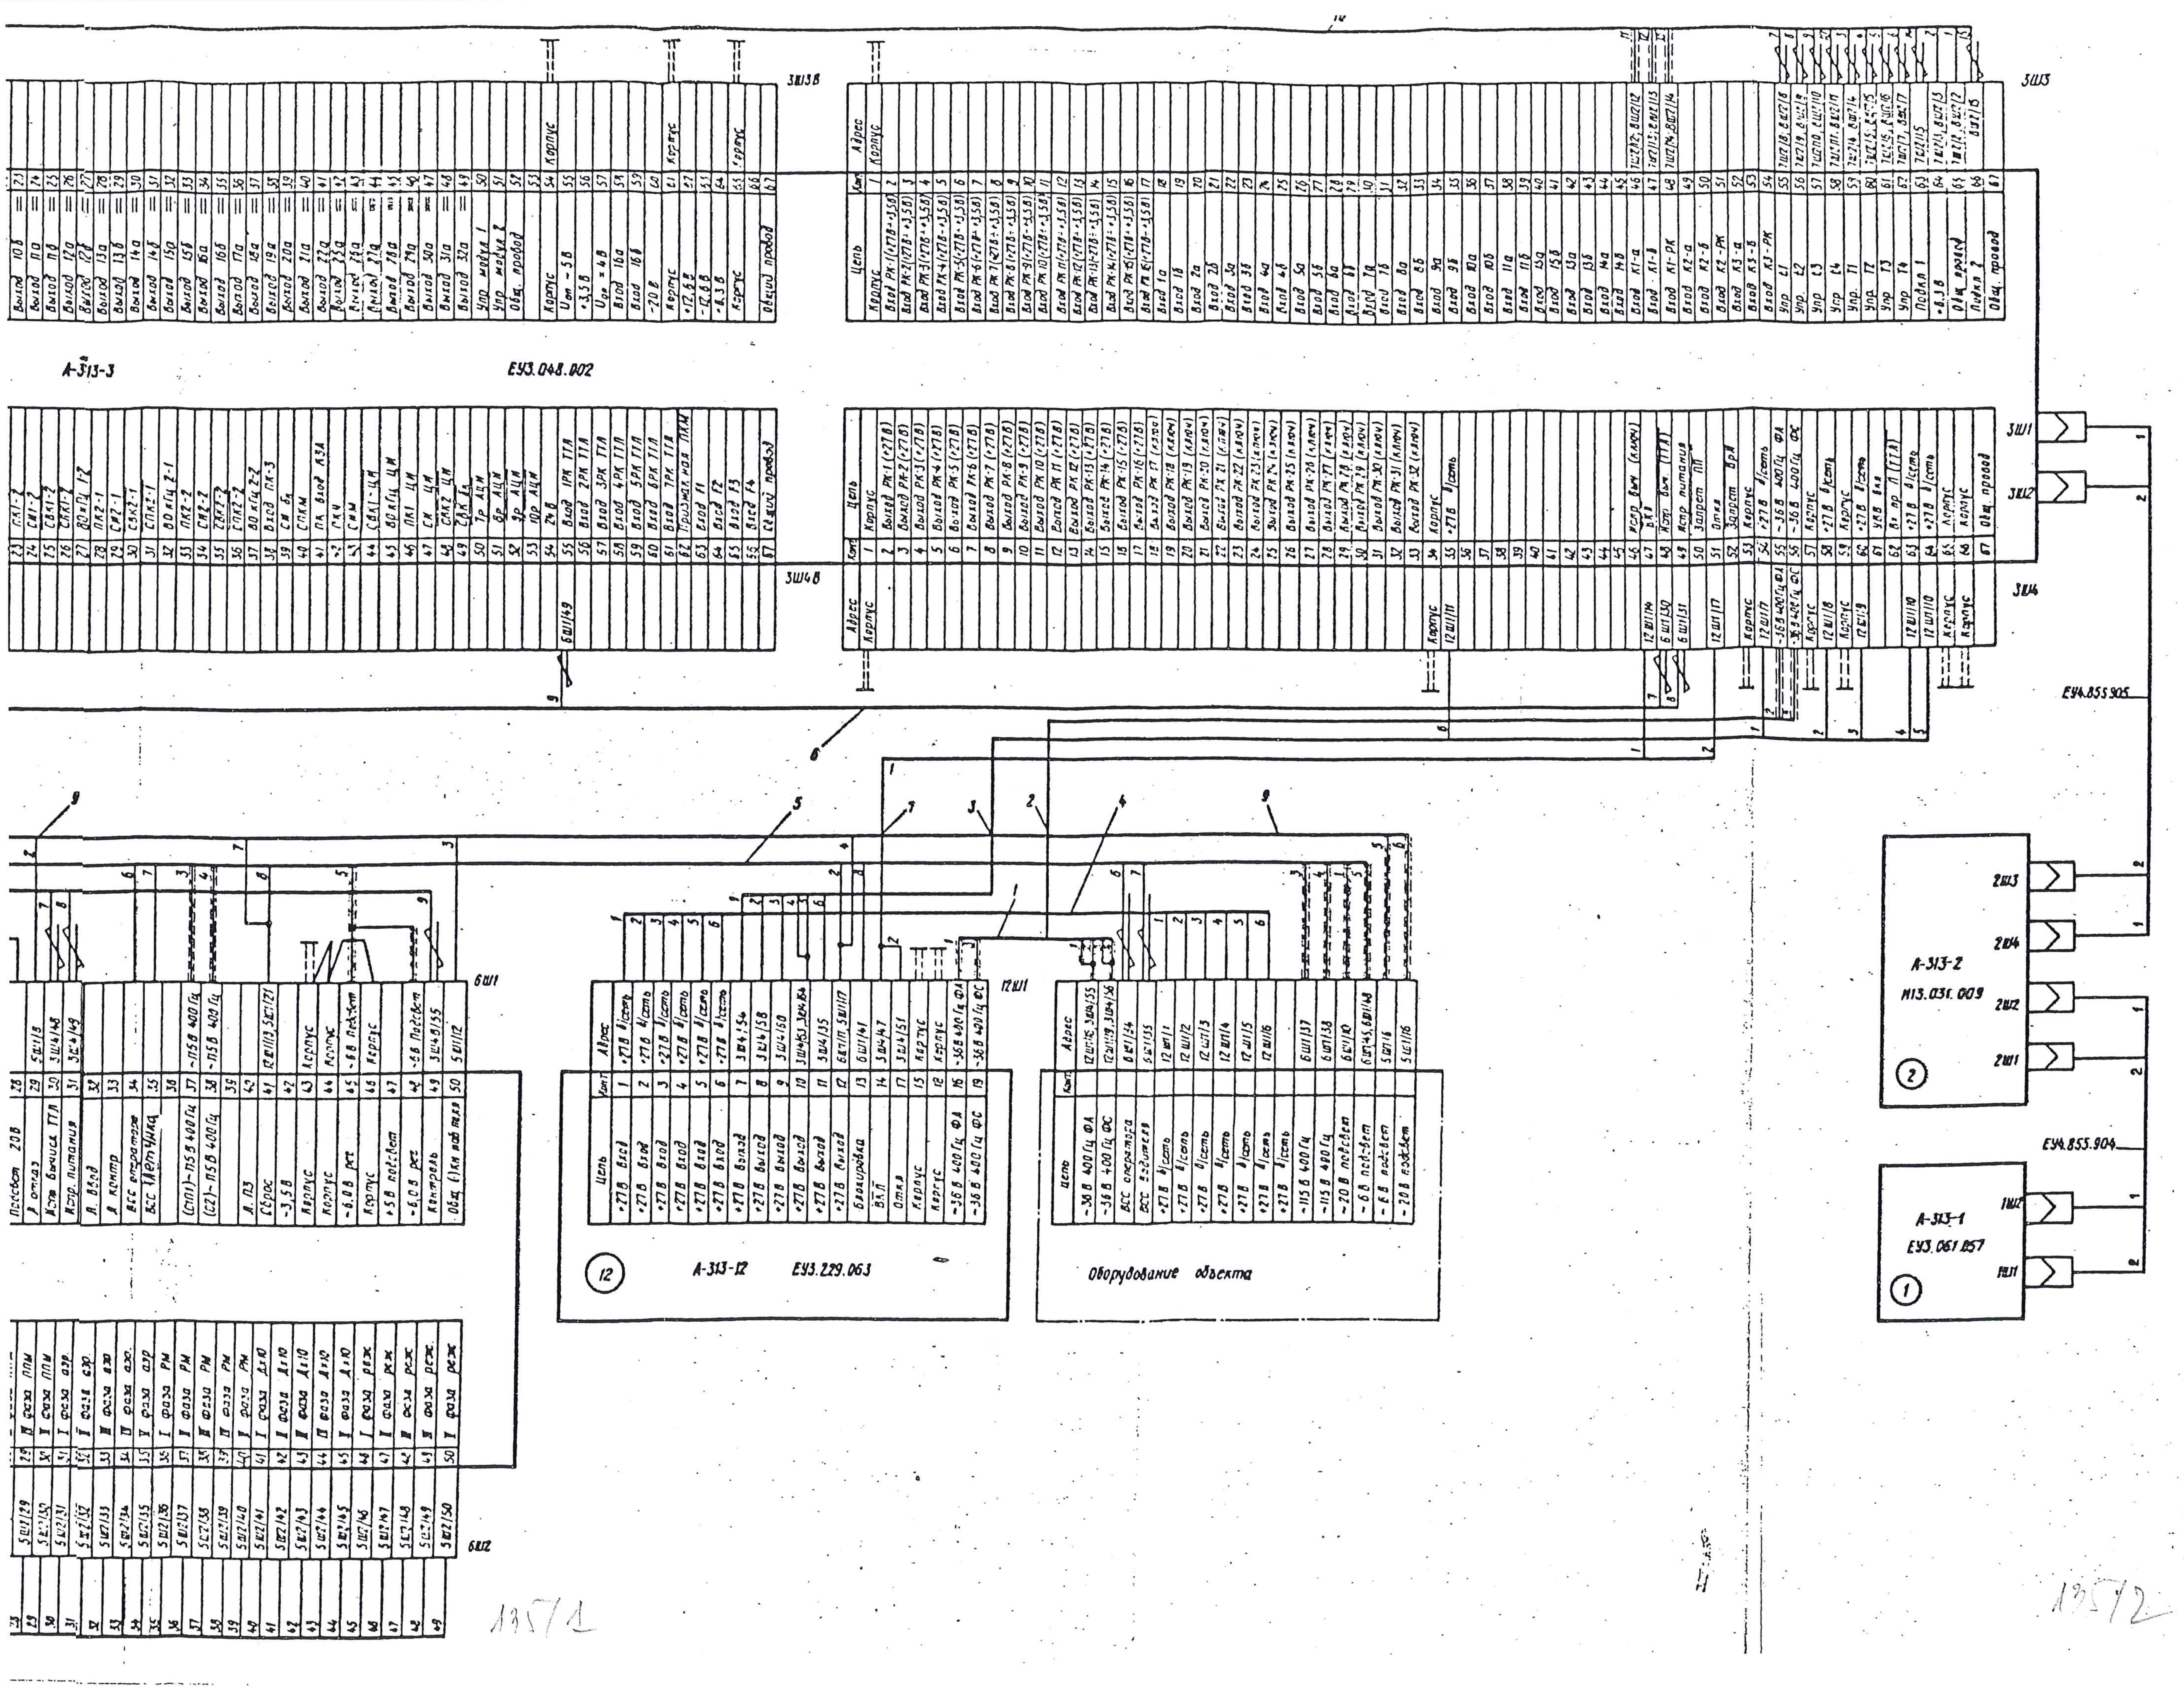
А-313-3
ЕУ3.048.002
3Ш3В
3Ш3
3Ш4В
3Ш4
3Ш1
3Ш2
ЕУ4.855.905
6Ш1
6Ш2
12Ш1
12
А-313-12
ЕУ3.229.063
Оборудование объекта
А-313-2
М13.031.009
2
2Ш3
2Ш4
2Ш2
2Ш1
ЕУ4.855.904
А-313-1
ЕУ3.061.257
1
1Ш2
1Ш1
Цепь
Конт
Адрес
Корпус

1357/1

1357/2