А-313

РУКОВОДСТВО ПО ТЕХНИЧЕСКОЙ ЭКСПЛУАТАЦИИ

АППАРАТУРА А-313. СХЕМА ЭЛЕКТРИЧЕСКАЯ СОЕДИНЕНИЙ
КОМПЛЕКТАЦИЙ ЕУ1.247.199-03 34, ЕУ1.247.199-04 34,
ЕУ1.247.199-04.01 34, ЕУ1.247.199-05 34
Рис. 2 (лист 2 из 2)

110.23.00

Приложение 1
Стр. 9/10
Янв 20/89

137

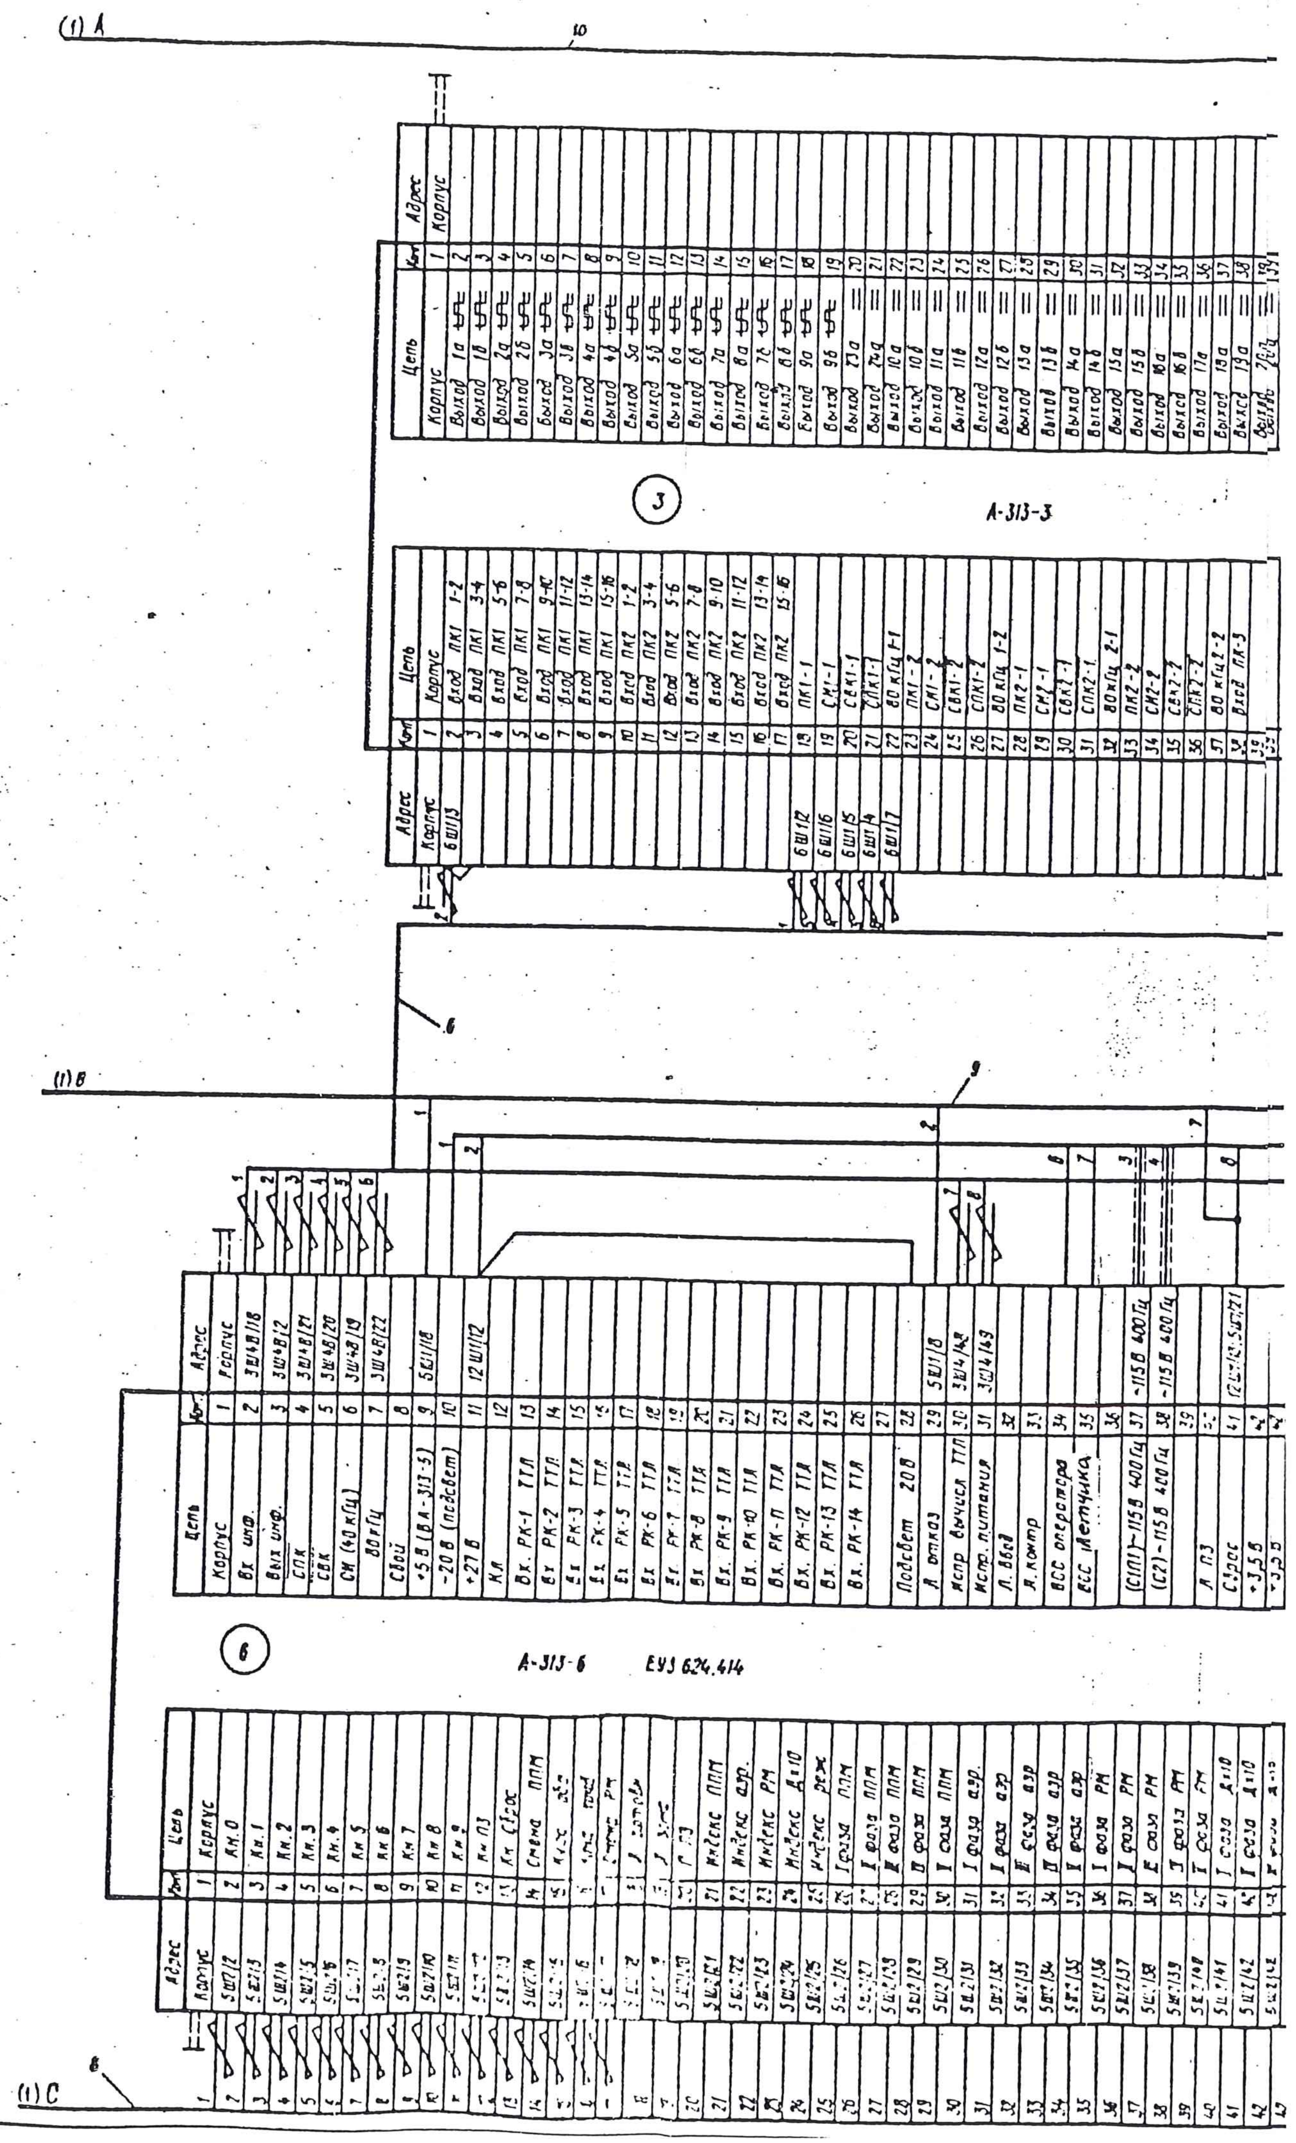

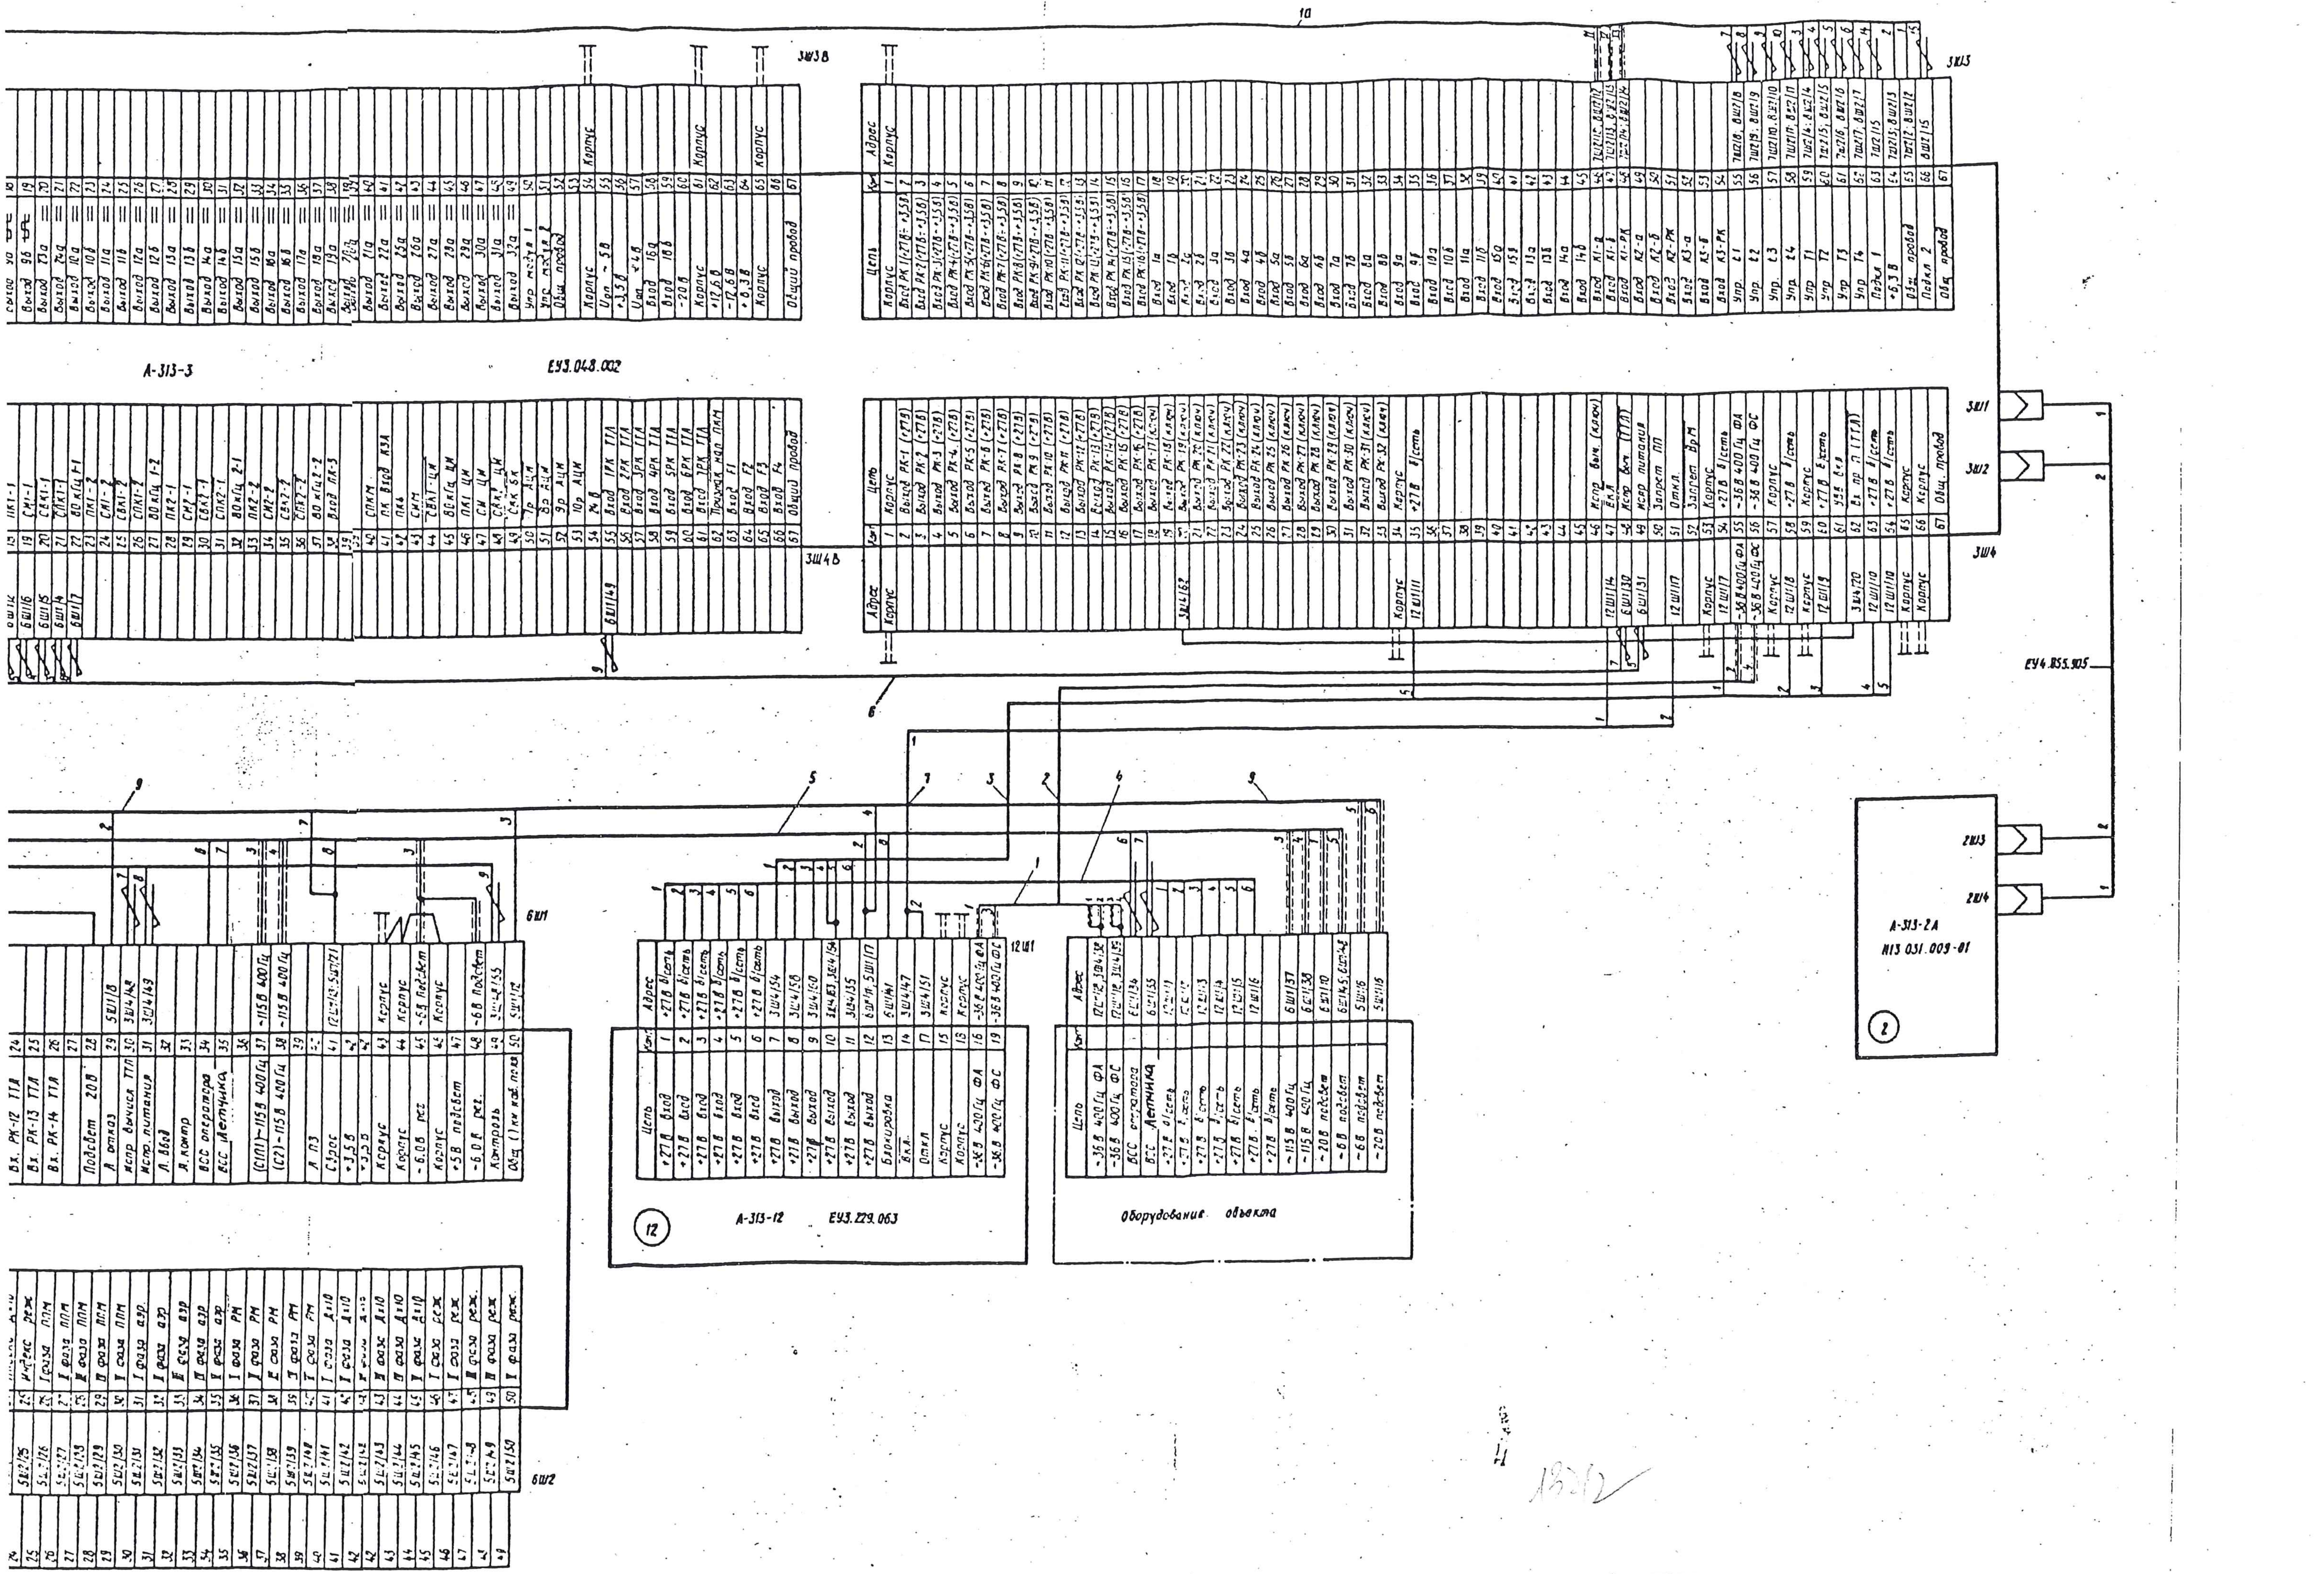
10
3Ш3В
3Ш3
А-313-3
ЕУЗ.048.002
3Ш4В
3Ш1
3Ш2
3Ш4
ЕУ4.855.905
6
9
5
1
3
2
4
6Ш1
12Ш1
2Ш3
2Ш4
А-313-2А
И13 031.009-01
2
12
А-313-12
ЕУЗ.229.063
Оборудование объекта
6Ш2