АТАЦИИ

Примечание

МГТФ

Примечание

МГТФ

ЕУ3.048.004-04

-

1

м объекта

ЕНИЙ

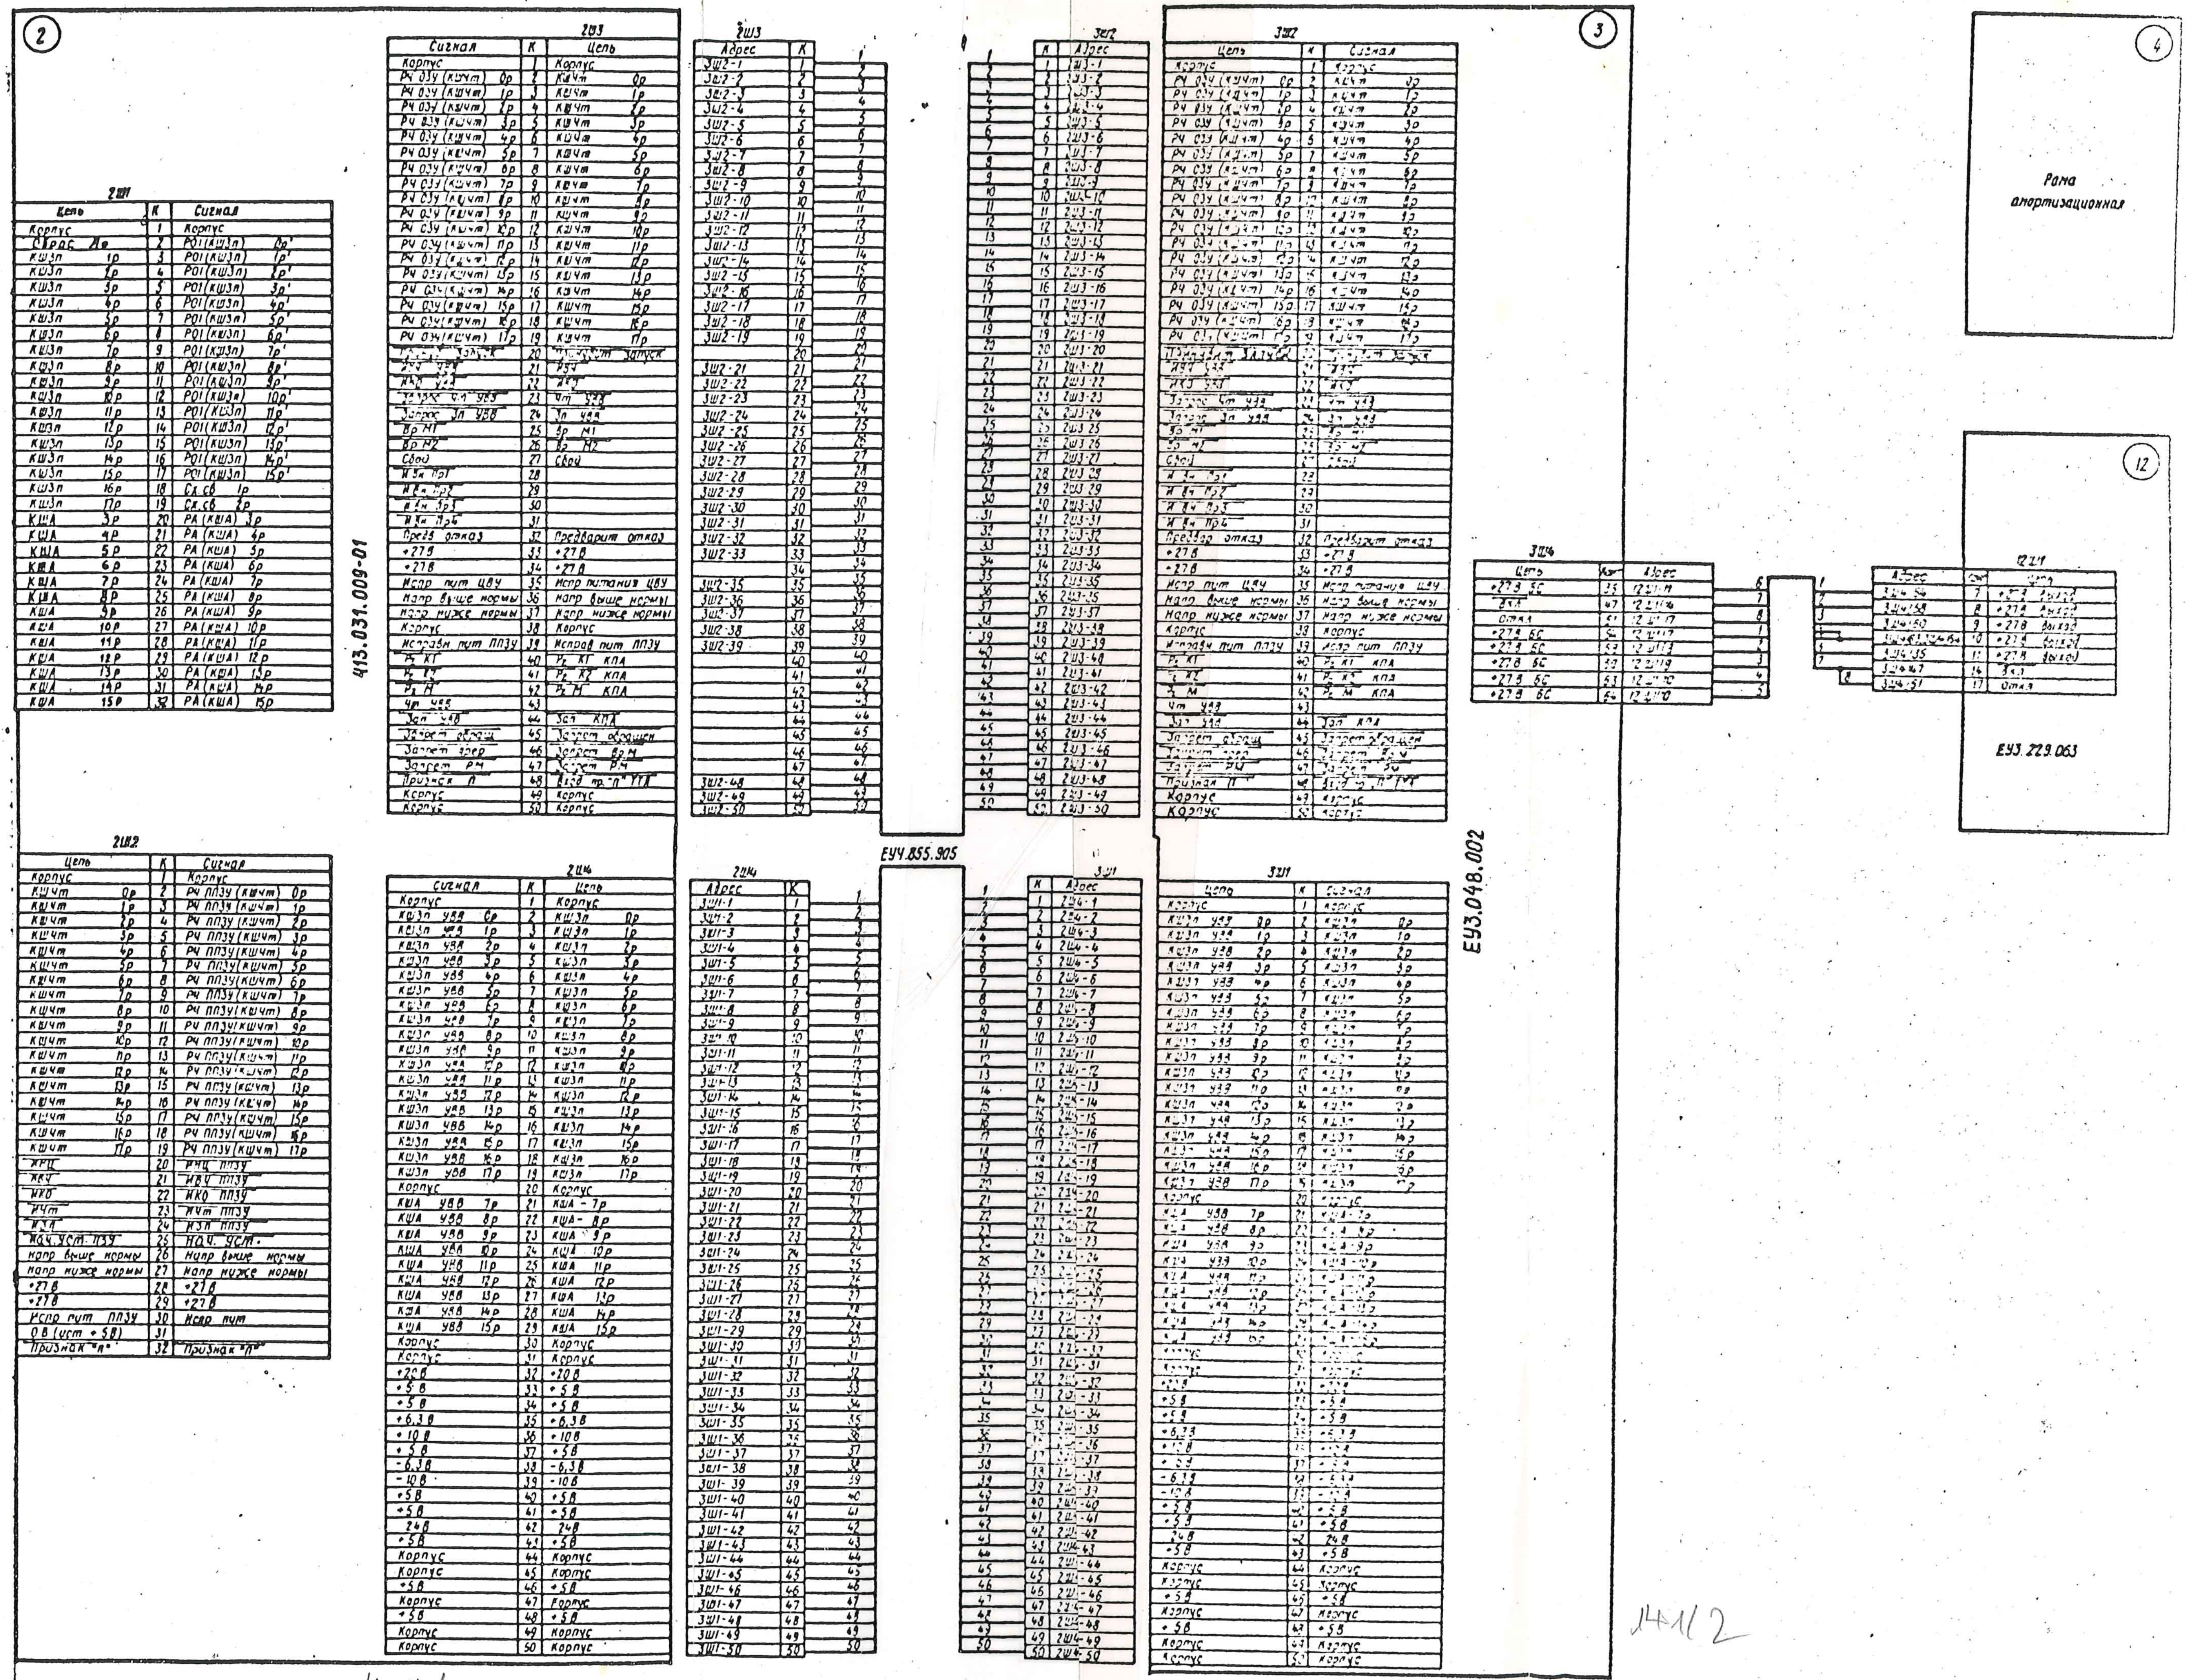

2Ш1

Цепь	К	Сигнал
Корпус	1	Корпус
Сброс Ао	2	РО1(КШ3п) 0р'
КШ3п 1р	3	РО1(КШ3п) 1р'
КШ3п 2р	4	РО1(КШ3п) 2р'
КШ3п 3р	5	РО1(КШ3п) 3р'
КШ3п 4р	6	РО1(КШ3п) 4р'
КШ3п 5р	7	РО1(КШ3п) 5р'
КШ3п 6р	8	РО1(КШ3п) 6р'
КШ3п 7р	9	РО1(КШ3п) 7р'
КШ3п 8р	10	РО1(КШ3п) 8р'
КШ3п 9р	11	РО1(КШ3п) 9р'
КШ3п 10р	12	РО1(КШ3п) 10р'
КШ3п 11р	13	РО1(КШ3п) 11р'
КШ3п 12р	14	РО1(КШ3п) 12р'
КШ3п 13р	15	РО1(КШ3п) 13р'
КШ3п 14р	16	РО1(КШ3п) 14р'
КШ3п 15р	17	РО1(КШ3п) 15р'
КШ3п 16р	18	Сх.сб 1р
КШ3п 17р	19	Сх.сб 2р
КША 3р	20	РА (КША) 3р
КША 4р	21	РА (КША) 4р
КША 5р	22	РА (КША) 5р
КША 6р	23	РА (КША) 6р
КША 7р	24	РА (КША) 7р
КША 8р	25	РА (КША) 8р
КША 9р	26	РА (КША) 9р
КША 10р	27	РА (КША) 10р
КША 11р	28	РА (КША) 11р
КША 12р	29	РА (КША) 12р
КША 13р	30	РА (КША) 13р
КША 14р	31	РА (КША) 14р
КША 15р	32	РА (КША) 15р

2Ш2

Цепь	К	Сигнал
Корпус	1	Корпус
КШЧт 0р	2	РЧ ППЗУ (КШЧт) 0р
КШЧт 1р	3	РЧ ППЗУ (КШЧт) 1р
КШЧт 2р	4	РЧ ППЗУ (КШЧт) 2р
КШЧт 3р	5	РЧ ППЗУ (КШЧт) 3р
КШЧт 4р	6	РЧ ППЗУ (КШЧт) 4р
КШЧт 5р	7	РЧ ППЗУ (КШЧт) 5р
КШЧт 6р	8	РЧ ППЗУ (КШЧт) 6р
КШЧт 7р	9	РЧ ППЗУ (КШЧт) 7р
КШЧт 8р	10	РЧ ППЗУ (КШЧт) 8р
КШЧт 9р	11	РЧ ППЗУ (КШЧт) 9р
КШЧт 10р	12	РЧ ППЗУ (КШЧт) 10р
КШЧт 11р	13	РЧ ППЗУ (КШЧт) 11р
КШЧт 12р	14	РЧ ППЗУ (КШЧт) 12р
КШЧт 13р	15	РЧ ППЗУ (КШЧт) 13р
КШЧт 14р	16	РЧ ППЗУ (КШЧт) 14р
КШЧт 15р	17	РЧ ППЗУ (КШЧт) 15р
КШЧт 16р	18	РЧ ППЗУ (КШЧт) 16р
КШЧт 17р	19	РЧ ППЗУ (КШЧт) 17р
РНЦ	20	РНЦ ППЗУ
ИБЧ	21	ИБЧ ППЗУ
ИКО	22	ИКО ППЗУ
ИЧт	23	ИЧт ППЗУ
ИЗП	24	ИЗП ППЗУ
Нач. уст. ППЗУ	25	Нач. уст.
Напр выше нормы	26	Напр выше нормы
Напр ниже нормы	27	Напр ниже нормы
+27В	28	+27В
+27В	29	+27В
Испр пит ППЗУ	30	Испр пит
0В (уст +5В)	31	
Признак "П"	32	Признак "П"

2Ш3

Сигнал	К	Цепь
Корпус	1	Корпус
РЧ ОЗУ (КШЧт) 0р	2	КШЧт 0р
РЧ ОЗУ (КШЧт) 1р	3	КШЧт 1р
РЧ ОЗУ (КШЧт) 2р	4	КШЧт 2р
РЧ ОЗУ (КШЧт) 3р	5	КШЧт 3р
РЧ ОЗУ (КШЧт) 4р	6	КШЧт 4р
РЧ ОЗУ (КШЧт) 5р	7	КШЧт 5р
РЧ ОЗУ (КШЧт) 6р	8	КШЧт 6р
РЧ ОЗУ (КШЧт) 7р	9	КШЧт 7р
РЧ ОЗУ (КШЧт) 8р	10	КШЧт 8р
РЧ ОЗУ (КШЧт) 9р	11	КШЧт 9р
РЧ ОЗУ (КШЧт) 10р	12	КШЧт 10р
РЧ ОЗУ (КШЧт) 11р	13	КШЧт 11р
РЧ ОЗУ (КШЧт) 12р	14	КШЧт 12р
РЧ ОЗУ (КШЧт) 13р	15	КШЧт 13р
РЧ ОЗУ (КШЧт) 14р	16	КШЧт 14р
РЧ ОЗУ (КШЧт) 15р	17	КШЧт 15р
РЧ ОЗУ (КШЧт) 16р	18	КШЧт 16р
РЧ ОЗУ (КШЧт) 17р	19	КШЧт 17р
Признак запуск	20	[illegible] запуск
ИБЧ УВВ	21	ИБЧ
ИКО УВВ	22	ИКО
Запрос Чт УВВ	23	Чт УВВ
Запрос Зп УВВ	24	Зп УВВ
Вр М1	25	Вр М1
Вр М2	26	Вр М2
Сбой	27	Сбой
И Вн Пр1	28	
И Вн Пр2	29	
И Вн Пр3	30	
И Вн Пр4	31	
Предв отказ	32	Предварит отказ
+27В	33	+27В
+27В	34	+27В
Испр пит ЦВУ	35	Испр питания ЦВУ
Напр выше нормы	36	Напр выше нормы
Напр ниже нормы	37	Напр ниже нормы
Корпус	38	Корпус
Исправн пит ППЗУ	39	Исправ пит ППЗУ
$Р_2$ К1	40	$Р_2$ К1 КПА
$Р_2$ К2	41	$Р_2$ К2 КПА
$Р_2$ М	42	$Р_2$ М КПА
Чт УВВ	43	
Зп УВВ	44	Зп КПА
Запрет обращ	45	Запрет обращен
Запрет Врер	46	Запрет Вр.М
Запрет РМ	47	Запрет РМ
Признак П	48	Вход пр."П" УТЛ
Корпус	49	Корпус
Корпус	50	Корпус

2Ш3

Адрес	К
3Ш2-1	1
3Ш2-2	2
3Ш2-3	3
3Ш2-4	4
3Ш2-5	5
3Ш2-6	6
3Ш2-7	7
3Ш2-8	8
3Ш2-9	9
3Ш2-10	10
3Ш2-11	11
3Ш2-12	12
3Ш2-13	13
3Ш2-14	14
3Ш2-15	15
3Ш2-16	16
3Ш2-17	17
3Ш2-18	18
3Ш2-19	19
	20
3Ш2-21	21
3Ш2-22	22
3Ш2-23	23
3Ш2-24	24
3Ш2-25	25
3Ш2-26	26
3Ш2-27	27
3Ш2-28	28
3Ш2-29	29
3Ш2-30	30
3Ш2-31	31
3Ш2-32	32
3Ш2-33	33
	34
3Ш2-35	35
3Ш2-36	36
3Ш2-37	37
3Ш2-38	38
3Ш2-39	39
	40
	41
	42
	43
	44
	45
	46
	47
3Ш2-48	48
3Ш2-49	49
3Ш2-50	50

3Ш2

К	Адрес
1	2Ш3-1
2	2Ш3-2
3	2Ш3-3
4	2Ш3-4
5	2Ш3-5
6	2Ш3-6
7	2Ш3-7
8	2Ш3-8
9	2Ш3-9
10	2Ш3-10
11	2Ш3-11
12	2Ш3-12
13	2Ш3-13
14	2Ш3-14
15	2Ш3-15
16	2Ш3-16
17	2Ш3-17
18	2Ш3-18
19	2Ш3-19
20	2Ш3-20
21	2Ш3-21
22	2Ш3-22
23	2Ш3-23
24	2Ш3-24
25	2Ш3-25
26	2Ш3-26
27	2Ш3-27
28	2Ш3-28
29	2Ш3-29
30	2Ш3-30
31	2Ш3-31
32	2Ш3-32
33	2Ш3-33
34	2Ш3-34
35	2Ш3-35
36	2Ш3-35
37	2Ш3-37
38	2Ш3-38
39	2Ш3-39
40	2Ш3-40
41	2Ш3-41
42	2Ш3-42
43	2Ш3-43
44	2Ш3-44
45	2Ш3-45
46	2Ш3-46
47	2Ш3-47
48	2Ш3-48
49	2Ш3-49
50	2Ш3-50

3Ш2

Цепь	К	Сигнал
Корпус	1	Корпус
РЧ ОЗУ (КШЧт) 0р	2	КШЧт 0р
РЧ ОЗУ (КШЧт) 1р	3	КШЧт 1р
РЧ ОЗУ (КШЧт) 2р	4	КШЧт 2р
РЧ ОЗУ (КШЧт) 3р	5	КШЧт 3р
РЧ ОЗУ (КШЧт) 4р	6	КШЧт 4р
РЧ ОЗУ (КШЧт) 5р	7	КШЧт 5р
РЧ ОЗУ (КШЧт) 6р	8	КШЧт 6р
РЧ ОЗУ (КШЧт) 7р	9	КШЧт 7р
РЧ ОЗУ (КШЧт) 8р	10	КШЧт 8р
РЧ ОЗУ (КШЧт) 9р	11	КШЧт 9р
РЧ ОЗУ (КШЧт) 10р	12	КШЧт 10р
РЧ ОЗУ (КШЧт) 11р	13	КШЧт 11р
РЧ ОЗУ (КШЧт) 12р	14	КШЧт 12р
РЧ ОЗУ (КШЧт) 13р	15	КШЧт 13р
РЧ ОЗУ (КШЧт) 14р	16	КШЧт 14р
РЧ ОЗУ (КШЧт) 15р	17	КШЧт 15р
РЧ ОЗУ (КШЧт) 16р	18	КШЧт 16р
РЧ ОЗУ (КШЧт) 17р	19	КШЧт 17р
Признак запуск	20	[illegible] запуск
ИБЧ УВВ	21	ИБЧ
ИКО УВВ	22	ИКО
Запрос Чт УВВ	23	Чт УВВ
Запрос Зп УВВ	24	Зп УВВ
Вр М1	25	Вр М1
Вр М2	26	Вр М2
Сбой	27	Сбой
И Вн Пр1	28	
И Вн Пр2	29	
И Вн Пр3	30	
И Вн Пр4	31	
Предвар отказ	32	Предварит отказ
+27В	33	+27В
+27В	34	+27В
Испр пит ЦВУ	35	Испр питания ЦВУ
Напр выше нормы	36	Напр выше нормы
Напр ниже нормы	37	Напр ниже нормы
Корпус	38	Корпус
Исправн пит ППЗУ	39	Испр пит ППЗУ
$Р_2$ К1	40	$Р_2$ К1 КПА
$Р_2$ К2	41	$Р_2$ К2 КПА
$Р_2$ М	42	$Р_2$ М КПА
Чт УВВ	43	
Зп УВВ	44	Зп КПА
Запрет обращ	45	Запрет обращен
Запрет Врер	46	Запрет Вр.М
Запрет РМ	47	Запрет РМ
Признак П	48	Вход пр."П" УТЛ
Корпус	49	Корпус
Корпус	50	Корпус

2Ш4

Сигнал	К	Цепь
Корпус	1	Корпус
КШ3п УВВ 0р	2	КШ3п 0р
КШ3п УВВ 1р	3	КШ3п 1р
КШ3п УВВ 2р	4	КШ3п 2р
КШ3п УВВ 3р	5	КШ3п 3р
КШ3п УВВ 4р	6	КШ3п 4р
КШ3п УВВ 5р	7	КШ3п 5р
КШ3п УВВ 6р	8	КШ3п 6р
КШ3п УВВ 7р	9	КШ3п 7р
КШ3п УВВ 8р	10	КШ3п 8р
КШ3п УВВ 9р	11	КШ3п 9р
КШ3п УВВ 10р	12	КШ3п 10р
КШ3п УВВ 11р	13	КШ3п 11р
КШ3п УВВ 12р	14	КШ3п 12р
КШ3п УВВ 13р	15	КШ3п 13р
КШ3п УВВ 14р	16	КШ3п 14р
КШ3п УВВ 15р	17	КШ3п 15р
КШ3п УВВ 16р	18	КШ3п 16р
КШ3п УВВ 17р	19	КШ3п 17р
Корпус	20	Корпус
КША УВВ 7р	21	КША - 7р
КША УВВ 8р	22	КША - 8р
КША УВВ 9р	23	КША 9р
КША УВВ 10р	24	КША 10р
КША УВВ 11р	25	КША 11р
КША УВВ 12р	26	КША 12р
КША УВВ 13р	27	КША 13р
КША УВВ 14р	28	КША 14р
КША УВВ 15р	29	КША 15р
Корпус	30	Корпус
Корпус	31	Корпус
+20В	32	+20В
+5В	33	+5В
+5В	34	+5В
+6,3В	35	+6,3В
+10В	36	+10В
+5В	37	+5В
-6,3В	38	-6,3В
-10В	39	-10В
+5В	40	+5В
+5В	41	+5В
24В	42	24В
+5В	43	+5В
Корпус	44	Корпус
Корпус	45	Корпус
+5В	46	+5В
Корпус	47	Корпус
+5В	48	+5В
Корпус	49	Корпус
Корпус	50	Корпус

2Ш4

Адрес	К
3Ш1-1	1
3Ш1-2	2
3Ш1-3	3
3Ш1-4	4
3Ш1-5	5
3Ш1-6	6
3Ш1-7	7
3Ш1-8	8
3Ш1-9	9
3Ш1-10	10
3Ш1-11	11
3Ш1-12	12
3Ш1-13	13
3Ш1-14	14
3Ш1-15	15
3Ш1-16	16
3Ш1-17	17
3Ш1-18	18
3Ш1-19	19
3Ш1-20	20
3Ш1-21	21
3Ш1-22	22
3Ш1-23	23
3Ш1-24	24
3Ш1-25	25
3Ш1-26	26
3Ш1-27	27
3Ш1-28	28
3Ш1-29	29
3Ш1-30	30
3Ш1-31	31
3Ш1-32	32
3Ш1-33	33
3Ш1-34	34
3Ш1-35	35
3Ш1-36	36
3Ш1-37	37
3Ш1-38	38
3Ш1-39	39
3Ш1-40	40
3Ш1-41	41
3Ш1-42	42
3Ш1-43	43
3Ш1-44	44
3Ш1-45	45
3Ш1-46	46
3Ш1-47	47
3Ш1-48	48
3Ш1-49	49
3Ш1-50	50

3Ш1

К	Адрес
1	2Ш4-1
2	2Ш4-2
3	2Ш4-3
4	2Ш4-4
5	2Ш4-5
6	2Ш4-6
7	2Ш4-7
8	2Ш4-8
9	2Ш4-9
10	2Ш4-10
11	2Ш4-11
12	2Ш4-12
13	2Ш4-13
14	2Ш4-14
15	2Ш4-15
16	2Ш4-16
17	2Ш4-17
18	2Ш4-18
19	2Ш4-19
20	2Ш4-20
21	2Ш4-21
22	2Ш4-22
23	2Ш4-23
24	2Ш4-24
25	2Ш4-25
26	2Ш4-26
27	2Ш4-27
28	2Ш4-28
29	2Ш4-29
30	2Ш4-30
31	2Ш4-31
32	2Ш4-32
33	2Ш4-33
34	2Ш4-34
35	2Ш4-35
36	2Ш4-36
37	2Ш4-37
38	2Ш4-38
39	2Ш4-39
40	2Ш4-40
41	2Ш4-41
42	2Ш4-42
43	2Ш4-43
44	2Ш4-44
45	2Ш4-45
46	2Ш4-46
47	2Ш4-47
48	2Ш4-48
49	2Ш4-49
50	2Ш4-50

3Ш1

Цепь	К	Сигнал
Корпус	1	Корпус
КШ3п УВВ 0р	2	КШ3п 0р
КШ3п УВВ 1р	3	КШ3п 1р
КШ3п УВВ 2р	4	КШ3п 2р
КШ3п УВВ 3р	5	КШ3п 3р
КШ3п УВВ 4р	6	КШ3п 4р
КШ3п УВВ 5р	7	КШ3п 5р
КШ3п УВВ 6р	8	КШ3п 6р
КШ3п УВВ 7р	9	КШ3п 7р
КШ3п УВВ 8р	10	КШ3п 8р
КШ3п УВВ 9р	11	КШ3п 9р
КШ3п УВВ 10р	12	КШ3п 10р
КШ3п УВВ 11р	13	КШ3п 11р
КШ3п УВВ 12р	14	КШ3п 12р
КШ3п УВВ 13р	15	КШ3п 13р
КШ3п УВВ 14р	16	КШ3п 14р
КШ3п УВВ 15р	17	КШ3п 15р
КШ3п УВВ 16р	18	КШ3п 16р
КШ3п УВВ 17р	19	КШ3п 17р
Корпус	20	Корпус
КША УВВ 7р	21	КША - 7р
КША УВВ 8р	22	КША - 8р
КША УВВ 9р	23	КША - 9р
КША УВВ 10р	24	КША - 10р
КША УВВ 11р	25	КША - 11р
КША УВВ 12р	26	КША - 12р
КША УВВ 13р	27	КША - 13р
КША УВВ 14р	28	КША - 14р
КША УВВ 15р	29	КША - 15р
Корпус	30	Корпус
Корпус	31	Корпус
+20В	32	+20В
+5В	33	+5В
+5В	34	+5В
+6,3В	35	+6,3В
+10В	36	+10В
+5В	37	+5В
-6,3В	38	-6,3В
-10В	39	-10В
+5В	40	+5В
+5В	41	+5В
24В	42	24В
+5В	43	+5В
Корпус	44	Корпус
Корпус	45	Корпус
+5В	46	+5В
Корпус	47	Корпус
+5В	48	+5В
Корпус	49	Корпус
Корпус	50	Корпус

3Ш4

Цепь	К	Адрес
+27В БС	35	12Ш1-11
Вкл	47	12Ш1-14
Откл	51	12Ш1-17
+27В БС	52	12Ш1-7
+27В БС	53	12Ш1-8
+27В БС	50	12Ш1-9
+27В БС	53	12Ш1-10
+27В БС	54	12Ш1-10

12Ш1

Адрес	К	Цепь
3Ш4-52	7	+27В выход
3Ш4-53	8	+27В выход
3Ш4-50	9	+27В выход
3Ш4-53, 3Ш4-54	10	+27В выход
3Ш4-35	11	+27В выход
3Ш4-47	14	Вкл
3Ш4-51	17	Откл

14/1/1

14/1/2