…ечание

110.23.00
…иложение 1
Стр. 19/20
Янв 20/89

14Р2/1

14Р 2/2

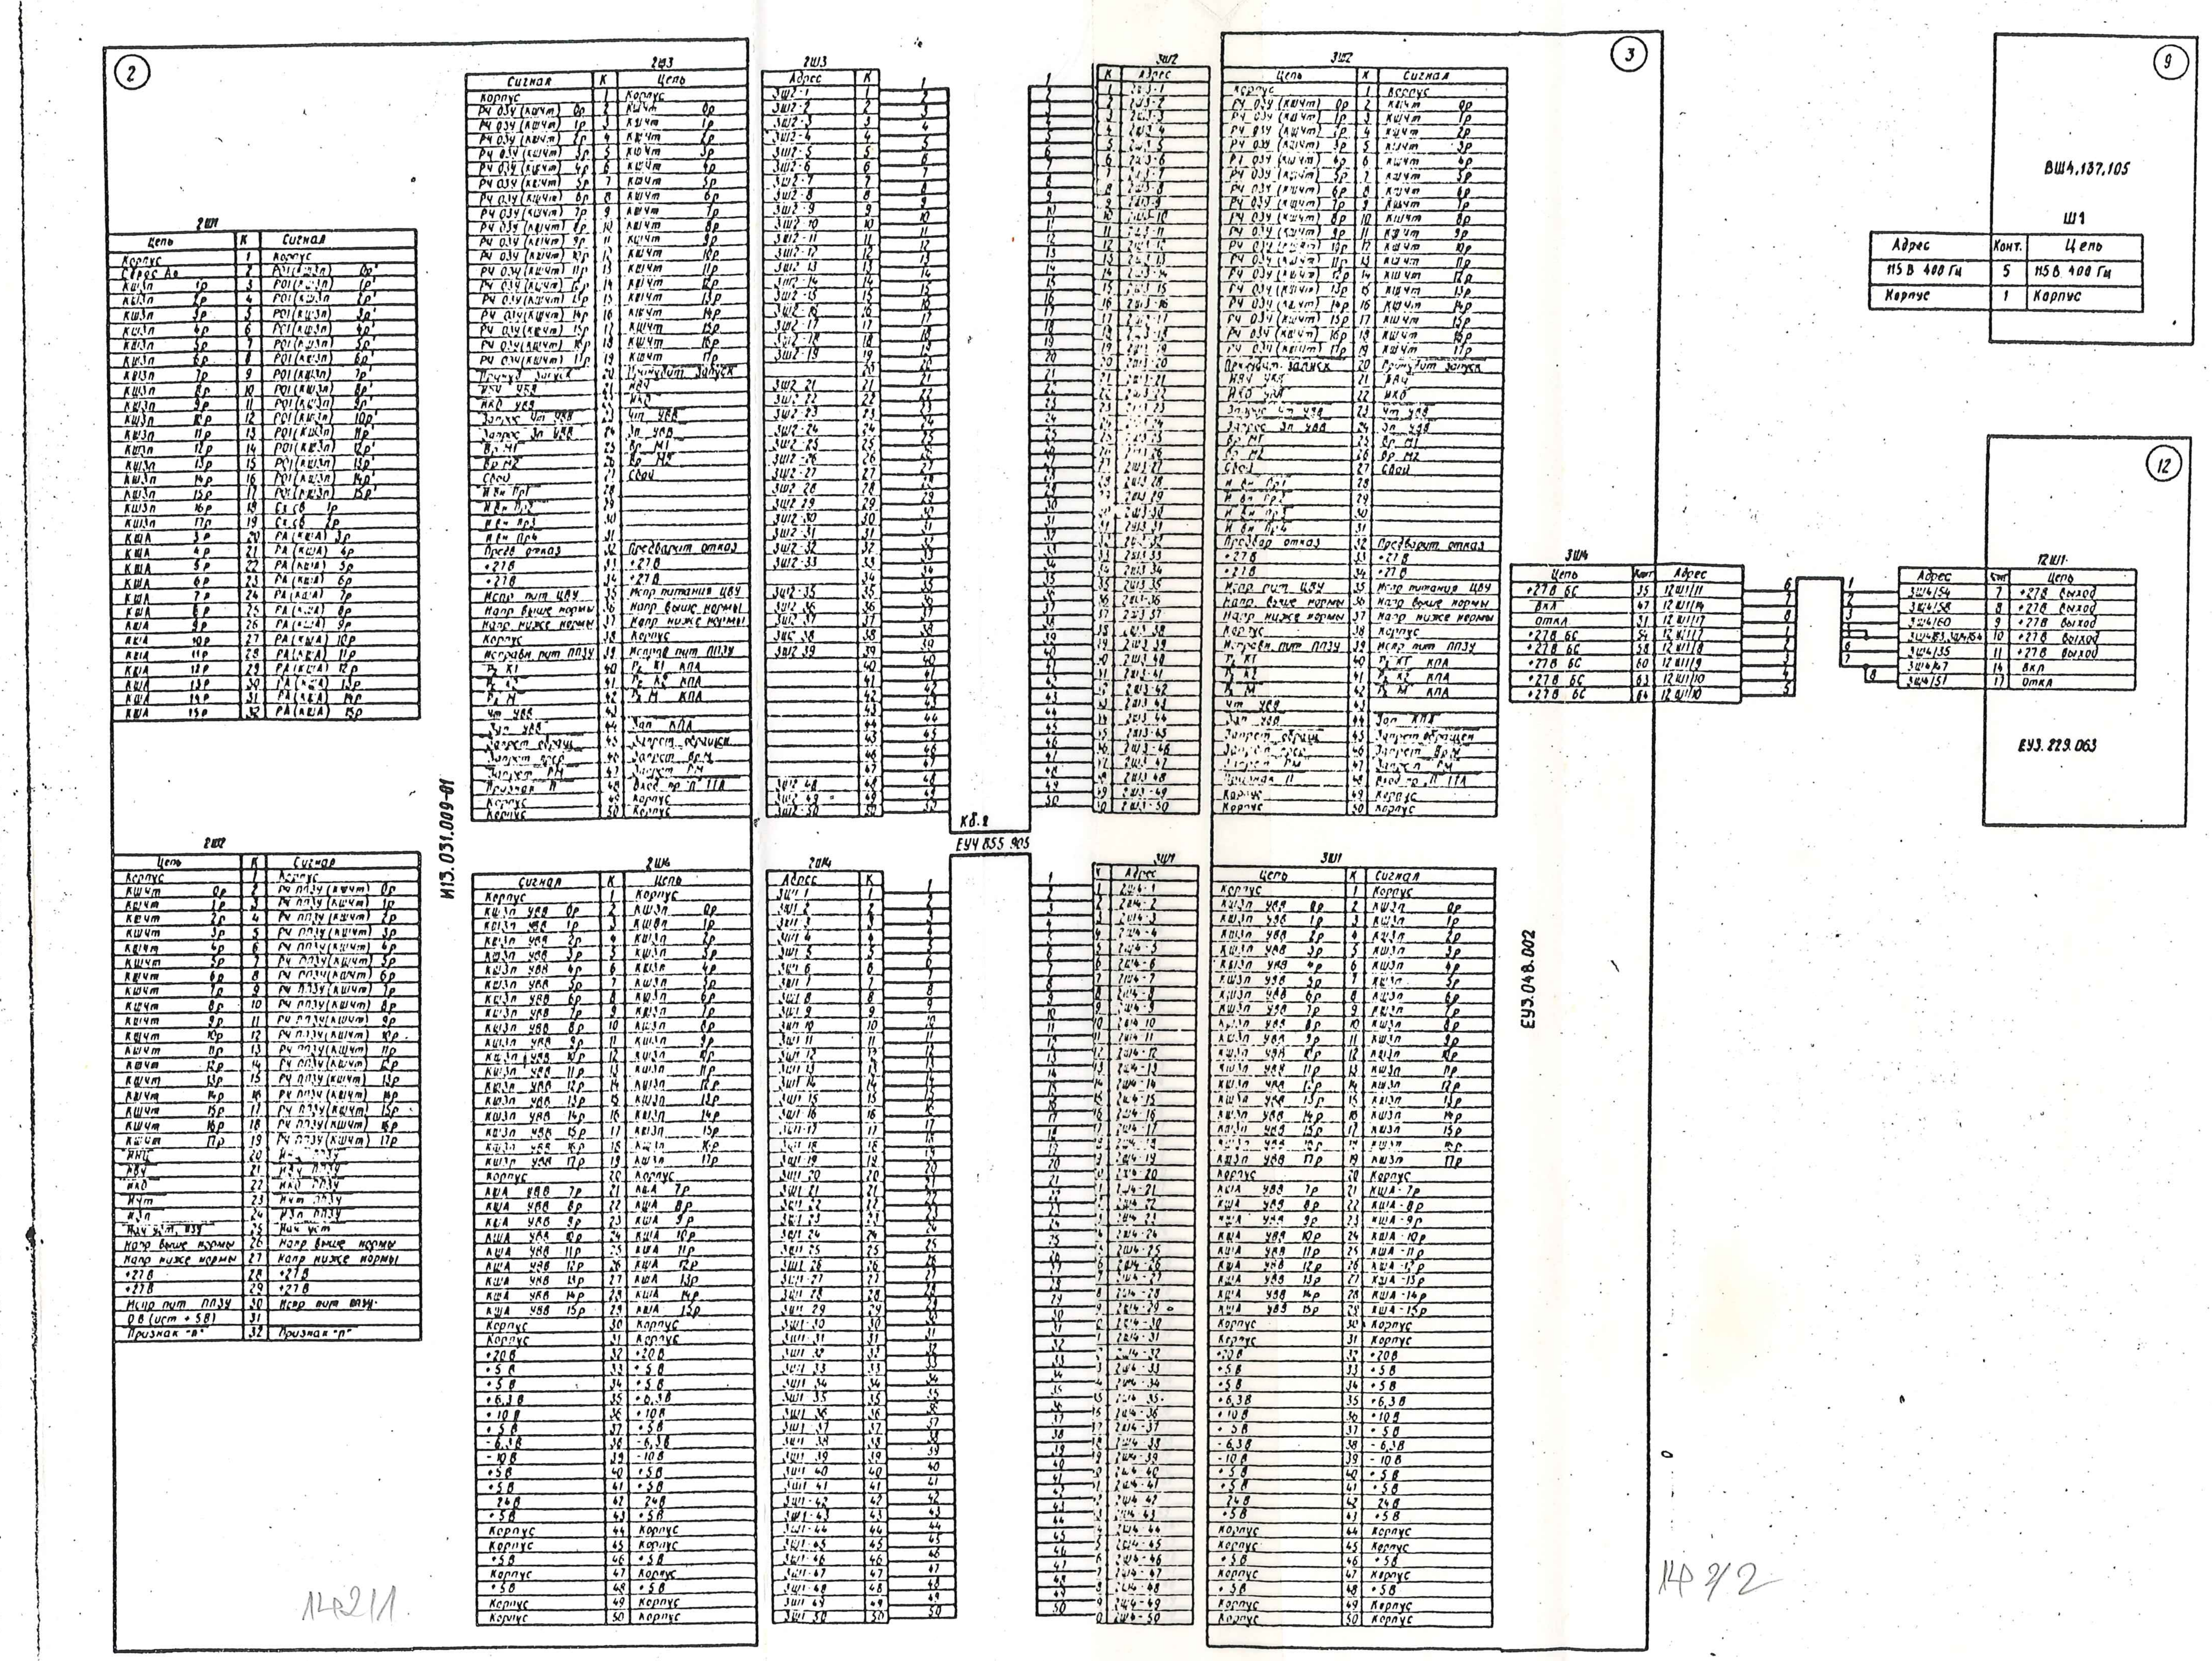

2Ш1

Цепь	К	Сигнал
Корпус	1	Корпус
Сброс Ао	2	РОI(КШЗп) 0р'
КШЗп 1р	3	РОI(КШЗп) 1р'
КШЗп 2р	4	РОI(КШЗп) 2р'
КШЗп 3р	5	РОI(КШЗп) 3р'
КШЗп 4р	6	РОI(КШЗп) 4р'
КШЗп 5р	7	РОI(КШЗп) 5р'
КШЗп 6р	8	РОI(КШЗп) 6р'
КШЗп 7р	9	РОI(КШЗп) 7р'
КШЗп 8р	10	РОI(КШЗп) 8р'
КШЗп 9р	11	РОI(КШЗп) 9р'
КШЗп 10р	12	РОI(КШЗп) 10р'
КШЗп 11р	13	РОI(КШЗп) 11р'
КШЗп 12р	14	РОI(КШЗп) 12р'
КШЗп 13р	15	РОI(КШЗп) 13р'
КШЗп 14р	16	РОI(КШЗп) 14р'
КШЗп 15р	17	РОI(КШЗп) 15р'
КШЗп 16р	18	Сх.сб 1р
КШЗп 17р	19	Сх.сб 2р
КША 3р	20	РА(КША) 3р
КША 4р	21	РА(КША) 4р
КША 5р	22	РА(КША) 5р
КША 6р	23	РА(КША) 6р
КША 7р	24	РА(КША) 7р
КША 8р	25	РА(КША) 8р
КША 9р	26	РА(КША) 9р
КША 10р	27	РА(КША) 10р
КША 11р	28	РА(КША) 11р
КША 12р	29	РА(КША) 12р
КША 13р	30	РА(КША) 13р
КША 14р	31	РА(КША) 14р
КША 15р	32	РА(КША) 15р

2Ш2

Цепь	К	Сигнал
Корпус	1	Корпус
КШЧт 0р	2	РЧ ППЗУ (КШЧт) 0р
КШЧт 1р	3	РЧ ППЗУ (КШЧт) 1р
КШЧт 2р	4	РЧ ППЗУ (КШЧт) 2р
КШЧт 3р	5	РЧ ППЗУ (КШЧт) 3р
КШЧт 4р	6	РЧ ППЗУ (КШЧт) 4р
КШЧт 5р	7	РЧ ППЗУ (КШЧт) 5р
КШЧт 6р	8	РЧ ППЗУ (КШЧт) 6р
КШЧт 7р	9	РЧ ППЗУ (КШЧт) 7р
КШЧт 8р	10	РЧ ППЗУ (КШЧт) 8р
КШЧт 9р	11	РЧ ППЗУ (КШЧт) 9р
КШЧт 10р	12	РЧ ППЗУ (КШЧт) 10р
КШЧт 11р	13	РЧ ППЗУ (КШЧт) 11р
КШЧт 12р	14	РЧ ППЗУ (КШЧт) 12р
КШЧт 13р	15	РЧ ППЗУ (КШЧт) 13р
КШЧт 14р	16	РЧ ППЗУ (КШЧт) 14р
КШЧт 15р	17	РЧ ППЗУ (КШЧт) 15р
КШЧт 16р	18	РЧ ППЗУ (КШЧт) 16р
КШЧт 17р	19	РЧ ППЗУ (КШЧт) 17р
ИНЦ	20	ИНЦ ППЗУ
НВУ	21	НВУ ППЗУ
ИКО	22	ИКО ППЗУ
ИЧт	23	ИЧт ППЗУ
ИЗп	24	ИЗп ППЗУ
Нач уст. ОЗУ	25	Нач уст
Напр выше нормы	26	Напр выше нормы
Напр ниже нормы	27	Напр ниже нормы
+27В	28	+27В
+27В	29	+27В
Испр пит ППЗУ	30	Испр пит ППЗУ
0В (уст + 5В)	31	
Признак "П"	32	Признак "П"

2Ш3

Сигнал	К	Цепь
Корпус	1	Корпус
РЧ ОЗУ (КШЧт) 0р	2	КШЧт 0р
РЧ ОЗУ (КШЧт) 1р	3	КШЧт 1р
РЧ ОЗУ (КШЧт) 2р	4	КШЧт 2р
РЧ ОЗУ (КШЧт) 3р	5	КШЧт 3р
РЧ ОЗУ (КШЧт) 4р	6	КШЧт 4р
РЧ ОЗУ (КШЧт) 5р	7	КШЧт 5р
РЧ ОЗУ (КШЧт) 6р	8	КШЧт 6р
РЧ ОЗУ (КШЧт) 7р	9	КШЧт 7р
РЧ ОЗУ (КШЧт) 8р	10	КШЧт 8р
РЧ ОЗУ (КШЧт) 9р	11	КШЧт 9р
РЧ ОЗУ (КШЧт) 10р	12	КШЧт 10р
РЧ ОЗУ (КШЧт) 11р	13	КШЧт 11р
РЧ ОЗУ (КШЧт) 12р	14	КШЧт 12р
РЧ ОЗУ (КШЧт) 13р	15	КШЧт 13р
РЧ ОЗУ (КШЧт) 14р	16	КШЧт 14р
РЧ ОЗУ (КШЧт) 15р	17	КШЧт 15р
РЧ ОЗУ (КШЧт) 16р	18	КШЧт 16р
РЧ ОЗУ (КШЧт) 17р	19	КШЧт 17р
Принуд. запуск	20	Принудит. запуск
НВУ УВВ	21	НВУ
ИКО УВВ	22	ИКО
Запрос Чт УВВ	23	Чт УВВ
Запрос Зп УВВ	24	Зп УВВ
Вр М1	25	Вр М1
Вр М2	26	Вр М2
Сбой	27	Сбой
И Вн Пр1	28	
И Вн Пр2	29	
И Вн Пр3	30	
И Вн Пр4	31	
Предв отказ	32	Предварит отказ
+27В	33	+27В
+27В	34	+27В
Испр пит ЦВУ	35	Испр питания ЦВУ
Напр выше нормы	36	Напр выше нормы
Напр ниже нормы	37	Напр ниже нормы
Корпус	38	Корпус
Исправн пит ППЗУ	39	Исправ пит ППЗУ
Рг К1	40	Рг К1 КПА
Рг К2	41	Рг К2 КПА
Рг М	42	Рг М КПА
Чт УВВ	43	
Зп УВВ	44	Зап КПА
Запрет обращ	45	Запрет обращен
Запрет врем	46	Запрет Вр.М
Запрет РМ	47	Запрет РМ
Признак П	48	Вход пр "П" ПА
Корпус	49	Корпус
Корпус	50	Корпус

2Ш3

Адрес	К
3Ш2-1	1
3Ш2-2	2
3Ш2-3	3
3Ш2-4	4
3Ш2-5	5
3Ш2-6	6
3Ш2-7	7
3Ш2-8	8
3Ш2-9	9
3Ш2-10	10
3Ш2-11	11
3Ш2-12	12
3Ш2-13	13
3Ш2-14	14
3Ш2-15	15
3Ш2-16	16
3Ш2-17	17
3Ш2-18	18
3Ш2-19	19
	20
3Ш2-21	21
3Ш2-22	22
3Ш2-23	23
3Ш2-24	24
3Ш2-25	25
3Ш2-26	26
3Ш2-27	27
3Ш2-28	28
3Ш2-29	29
3Ш2-30	30
3Ш2-31	31
3Ш2-32	32
3Ш2-33	33
	34
3Ш2-35	35
3Ш2-36	36
3Ш2-37	37
3Ш2-38	38
3Ш2-39	39
	40
	41
	42
	43
	44
	45
	46
	47
3Ш2-48	48
3Ш2-49	49
3Ш2-50	50

2Ш4

Сигнал	К	Цепь
Корпус	1	Корпус
КШЗп УВВ 0р	2	КШЗп 0р
КШЗп УВВ 1р	3	КШЗп 1р
КШЗп УВВ 2р	4	КШЗп 2р
КШЗп УВВ 3р	5	КШЗп 3р
КШЗп УВВ 4р	6	КШЗп 4р
КШЗп УВВ 5р	7	КШЗп 5р
КШЗп УВВ 6р	8	КШЗп 6р
КШЗп УВВ 7р	9	КШЗп 7р
КШЗп УВВ 8р	10	КШЗп 8р
КШЗп УВВ 9р	11	КШЗп 9р
КШЗп УВВ 10р	12	КШЗп 10р
КШЗп УВВ 11р	13	КШЗп 11р
КШЗп УВВ 12р	14	КШЗп 12р
КШЗп УВВ 13р	15	КШЗп 13р
КШЗп УВВ 14р	16	КШЗп 14р
КШЗп УВВ 15р	17	КШЗп 15р
КШЗп УВВ 16р	18	КШЗп 16р
КШЗп УВВ 17р	19	КШЗп 17р
Корпус	20	Корпус
КША УВВ 7р	21	КША 7р
КША УВВ 8р	22	КША 8р
КША УВВ 9р	23	КША 9р
КША УВВ 10р	24	КША 10р
КША УВВ 11р	25	КША 11р
КША УВВ 12р	26	КША 12р
КША УВВ 13р	27	КША 13р
КША УВВ 14р	28	КША 14р
КША УВВ 15р	29	КША 15р
Корпус	30	Корпус
Корпус	31	Корпус
+20В	32	+20В
+5В	33	+5В
+5В	34	+5В
+6,3В	35	+6,3В
+10В	36	+10В
+5В	37	+5В
-6,3В	38	-6,3В
-10В	39	-10В
+5В	40	+5В
+5В	41	+5В
24В	42	24В
+5В	43	+5В
Корпус	44	Корпус
Корпус	45	Корпус
+5В	46	+5В
Корпус	47	Корпус
+5В	48	+5В
Корпус	49	Корпус
Корпус	50	Корпус

2Ш4

Адрес	К
3Ш1-1	1
3Ш1-2	2
3Ш1-3	3
3Ш1-4	4
3Ш1-5	5
3Ш1-6	6
3Ш1-7	7
3Ш1-8	8
3Ш1-9	9
3Ш1-10	10
3Ш1-11	11
3Ш1-12	12
3Ш1-13	13
3Ш1-14	14
3Ш1-15	15
3Ш1-16	16
3Ш1-17	17
3Ш1-18	18
3Ш1-19	19
3Ш1-20	20
3Ш1-21	21
3Ш1-22	22
3Ш1-23	23
3Ш1-24	24
3Ш1-25	25
3Ш1-26	26
3Ш1-27	27
3Ш1-28	28
3Ш1-29	29
3Ш1-30	30
3Ш1-31	31
3Ш1-32	32
3Ш1-33	33
3Ш1-34	34
3Ш1-35	35
3Ш1-36	36
3Ш1-37	37
3Ш1-38	38
3Ш1-39	39
3Ш1-40	40
3Ш1-41	41
3Ш1-42	42
3Ш1-43	43
3Ш1-44	44
3Ш1-45	45
3Ш1-46	46
3Ш1-47	47
3Ш1-48	48
3Ш1-49	49
3Ш1-50	50

3Ш2

К	Адрес
1	2Ш3-1
2	2Ш3-2
3	2Ш3-3
4	2Ш3-4
5	2Ш3-5
6	2Ш3-6
7	2Ш3-7
8	2Ш3-8
9	2Ш3-9
10	2Ш3-10
11	2Ш3-11
12	2Ш3-12
13	2Ш3-13
14	2Ш3-14
15	2Ш3-15
16	2Ш3-16
17	2Ш3-17
18	2Ш3-18
19	2Ш3-19
20	2Ш3-20
21	2Ш3-21
22	2Ш3-22
23	2Ш3-23
24	2Ш3-24
25	2Ш3-25
26	2Ш3-26
27	2Ш3-27
28	2Ш3-28
29	2Ш3-29
30	2Ш3-30
31	2Ш3-31
32	2Ш3-32
33	2Ш3-33
34	2Ш3-34
35	2Ш3-35
36	2Ш3-36
37	2Ш3-37
38	2Ш3-38
39	2Ш3-39
40	2Ш3-40
41	2Ш3-41
42	2Ш3-42
43	2Ш3-43
44	2Ш3-44
45	2Ш3-45
46	2Ш3-46
47	2Ш3-47
48	2Ш3-48
49	2Ш3-49
50	2Ш3-50

3Ш2

Цепь	К	Сигнал
Корпус	1	Корпус
РЧ ОЗУ (КШЧт) 0р	2	КШЧт 0р
РЧ ОЗУ (КШЧт) 1р	3	КШЧт 1р
РЧ ОЗУ (КШЧт) 2р	4	КШЧт 2р
РЧ ОЗУ (КШЧт) 3р	5	КШЧт 3р
РЧ ОЗУ (КШЧт) 4р	6	КШЧт 4р
РЧ ОЗУ (КШЧт) 5р	7	КШЧт 5р
РЧ ОЗУ (КШЧт) 6р	8	КШЧт 6р
РЧ ОЗУ (КШЧт) 7р	9	КШЧт 7р
РЧ ОЗУ (КШЧт) 8р	10	КШЧт 8р
РЧ ОЗУ (КШЧт) 9р	11	КШЧт 9р
РЧ ОЗУ (КШЧт) 10р	12	КШЧт 10р
РЧ ОЗУ (КШЧт) 11р	13	КШЧт 11р
РЧ ОЗУ (КШЧт) 12р	14	КШЧт 12р
РЧ ОЗУ (КШЧт) 13р	15	КШЧт 13р
РЧ ОЗУ (КШЧт) 14р	16	КШЧт 14р
РЧ ОЗУ (КШЧт) 15р	17	КШЧт 15р
РЧ ОЗУ (КШЧт) 16р	18	КШЧт 16р
РЧ ОЗУ (КШЧт) 17р	19	КШЧт 17р
Принудит. запуск	20	Принудит запуск
НВУ УВВ	21	НВУ
ИКО УВВ	22	ИКО
Запрос Чт УВВ	23	Чт УВВ
Запрос Зп УВВ	24	Зп УВВ
Вр М1	25	Вр М1
Вр М2	26	Вр М2
Сбой	27	Сбой
И Вн Пр1	28	
И Вн Пр2	29	
И Вн Пр3	30	
И Вн Пр4	31	
Предвар отказ	32	Предварит. отказ
+27В	33	+27В
+27В	34	+27В
Испр пит ЦВУ	35	Испр питания ЦВУ
Напр. выше нормы	36	Напр выше нормы
Напр ниже нормы	37	Напр ниже нормы
Корпус	38	Корпус
Исправн. пит ППЗУ	39	Испр пит ППЗУ
Рг К1	40	Рг К1 КПА
Рг К2	41	Рг К2 КПА
Рг М	42	Рг М КПА
Чт УВВ	43	
Зп УВВ	44	Зап КПА
Запрет обращ	45	Запрет обращен
Запрет врем	46	Запрет Вр.М
Запрет РМ	47	Запрет РМ
Признак П	48	Вход пр "П" ПА
Корпус	49	Корпус
Корпус	50	Корпус

3Ш1

К	Адрес
1	2Ш4-1
2	2Ш4-2
3	2Ш4-3
4	2Ш4-4
5	2Ш4-5
6	2Ш4-6
7	2Ш4-7
8	2Ш4-8
9	2Ш4-9
10	2Ш4-10
11	2Ш4-11
12	2Ш4-12
13	2Ш4-13
14	2Ш4-14
15	2Ш4-15
16	2Ш4-16
17	2Ш4-17
18	2Ш4-18
19	2Ш4-19
20	2Ш4-20
21	2Ш4-21
22	2Ш4-22
23	2Ш4-23
24	2Ш4-24
25	2Ш4-25
26	2Ш4-26
27	2Ш4-27
28	2Ш4-28
29	2Ш4-29
30	2Ш4-30
31	2Ш4-31
32	2Ш4-32
33	2Ш4-33
34	2Ш4-34
35	2Ш4-35
36	2Ш4-36
37	2Ш4-37
38	2Ш4-38
39	2Ш4-39
40	2Ш4-40
41	2Ш4-41
42	2Ш4-42
43	2Ш4-43
44	2Ш4-44
45	2Ш4-45
46	2Ш4-46
47	2Ш4-47
48	2Ш4-48
49	2Ш4-49
50	2Ш4-50

3Ш1

Цепь	К	Сигнал
Корпус	1	Корпус
КШЗп УВВ 0р	2	КШЗп 0р
КШЗп УВВ 1р	3	КШЗп 1р
КШЗп УВВ 2р	4	КШЗп 2р
КШЗп УВВ 3р	5	КШЗп 3р
КШЗп УВВ 4р	6	КШЗп 4р
КШЗп УВВ 5р	7	КШЗп 5р
КШЗп УВВ 6р	8	КШЗп 6р
КШЗп УВВ 7р	9	КШЗп 7р
КШЗп УВВ 8р	10	КШЗп 8р
КШЗп УВВ 9р	11	КШЗп 9р
КШЗп УВВ 10р	12	КШЗп 10р
КШЗп УВВ 11р	13	КШЗп 11р
КШЗп УВВ 12р	14	КШЗп 12р
КШЗп УВВ 13р	15	КШЗп 13р
КШЗп УВВ 14р	16	КШЗп 14р
КШЗп УВВ 15р	17	КШЗп 15р
КШЗп УВВ 16р	18	КШЗп 16р
КШЗп УВВ 17р	19	КШЗп 17р
Корпус	20	Корпус
КША УВВ 7р	21	КША-7р
КША УВВ 8р	22	КША-8р
КША УВВ 9р	23	КША-9р
КША УВВ 10р	24	КША-10р
КША УВВ 11р	25	КША-11р
КША УВВ 12р	26	КША-12р
КША УВВ 13р	27	КША-13р
КША УВВ 14р	28	КША-14р
КША УВВ 15р	29	КША-15р
Корпус	30	Корпус
Корпус	31	Корпус
+20В	32	+20В
+5В	33	+5В
+5В	34	+5В
+6,3В	35	+6,3В
+10В	36	+10В
+5В	37	+5В
-6,3В	38	-6,3В
-10В	39	-10В
+5В	40	+5В
+5В	41	+5В
24В	42	24В
+5В	43	+5В
Корпус	44	Корпус
Корпус	45	Корпус
+5В	46	+5В
Корпус	47	Корпус
+5В	48	+5В
Корпус	49	Корпус
Корпус	50	Корпус

3Ш4

Цепь	Конт	Адрес
+27В БС	35	12Ш1/11
Вкл	47	12Ш1/14
Откл	51	12Ш1/17
+27В БС	54	12Ш1/7
+27В БС	58	12Ш1/8
+27В БС	60	12Ш1/9
+27В БС	63	12Ш1/10
+27В БС	64	12Ш1/10

12Ш1

Адрес	Конт	Цепь
3Ш4/54	7	+27В выход
3Ш4/58	8	+27В выход
3Ш4/60	9	+27В выход
3Ш4/63, 3Ш4/64	10	+27В выход
3Ш4/35	11	+27В выход
3Ш4/47	14	Вкл
3Ш4/51	17	Откл

Ш1

Адрес	Конт.	Цепь
115В 400 Гц	5	115В 400 Гц
Корпус	1	Корпус