101/192

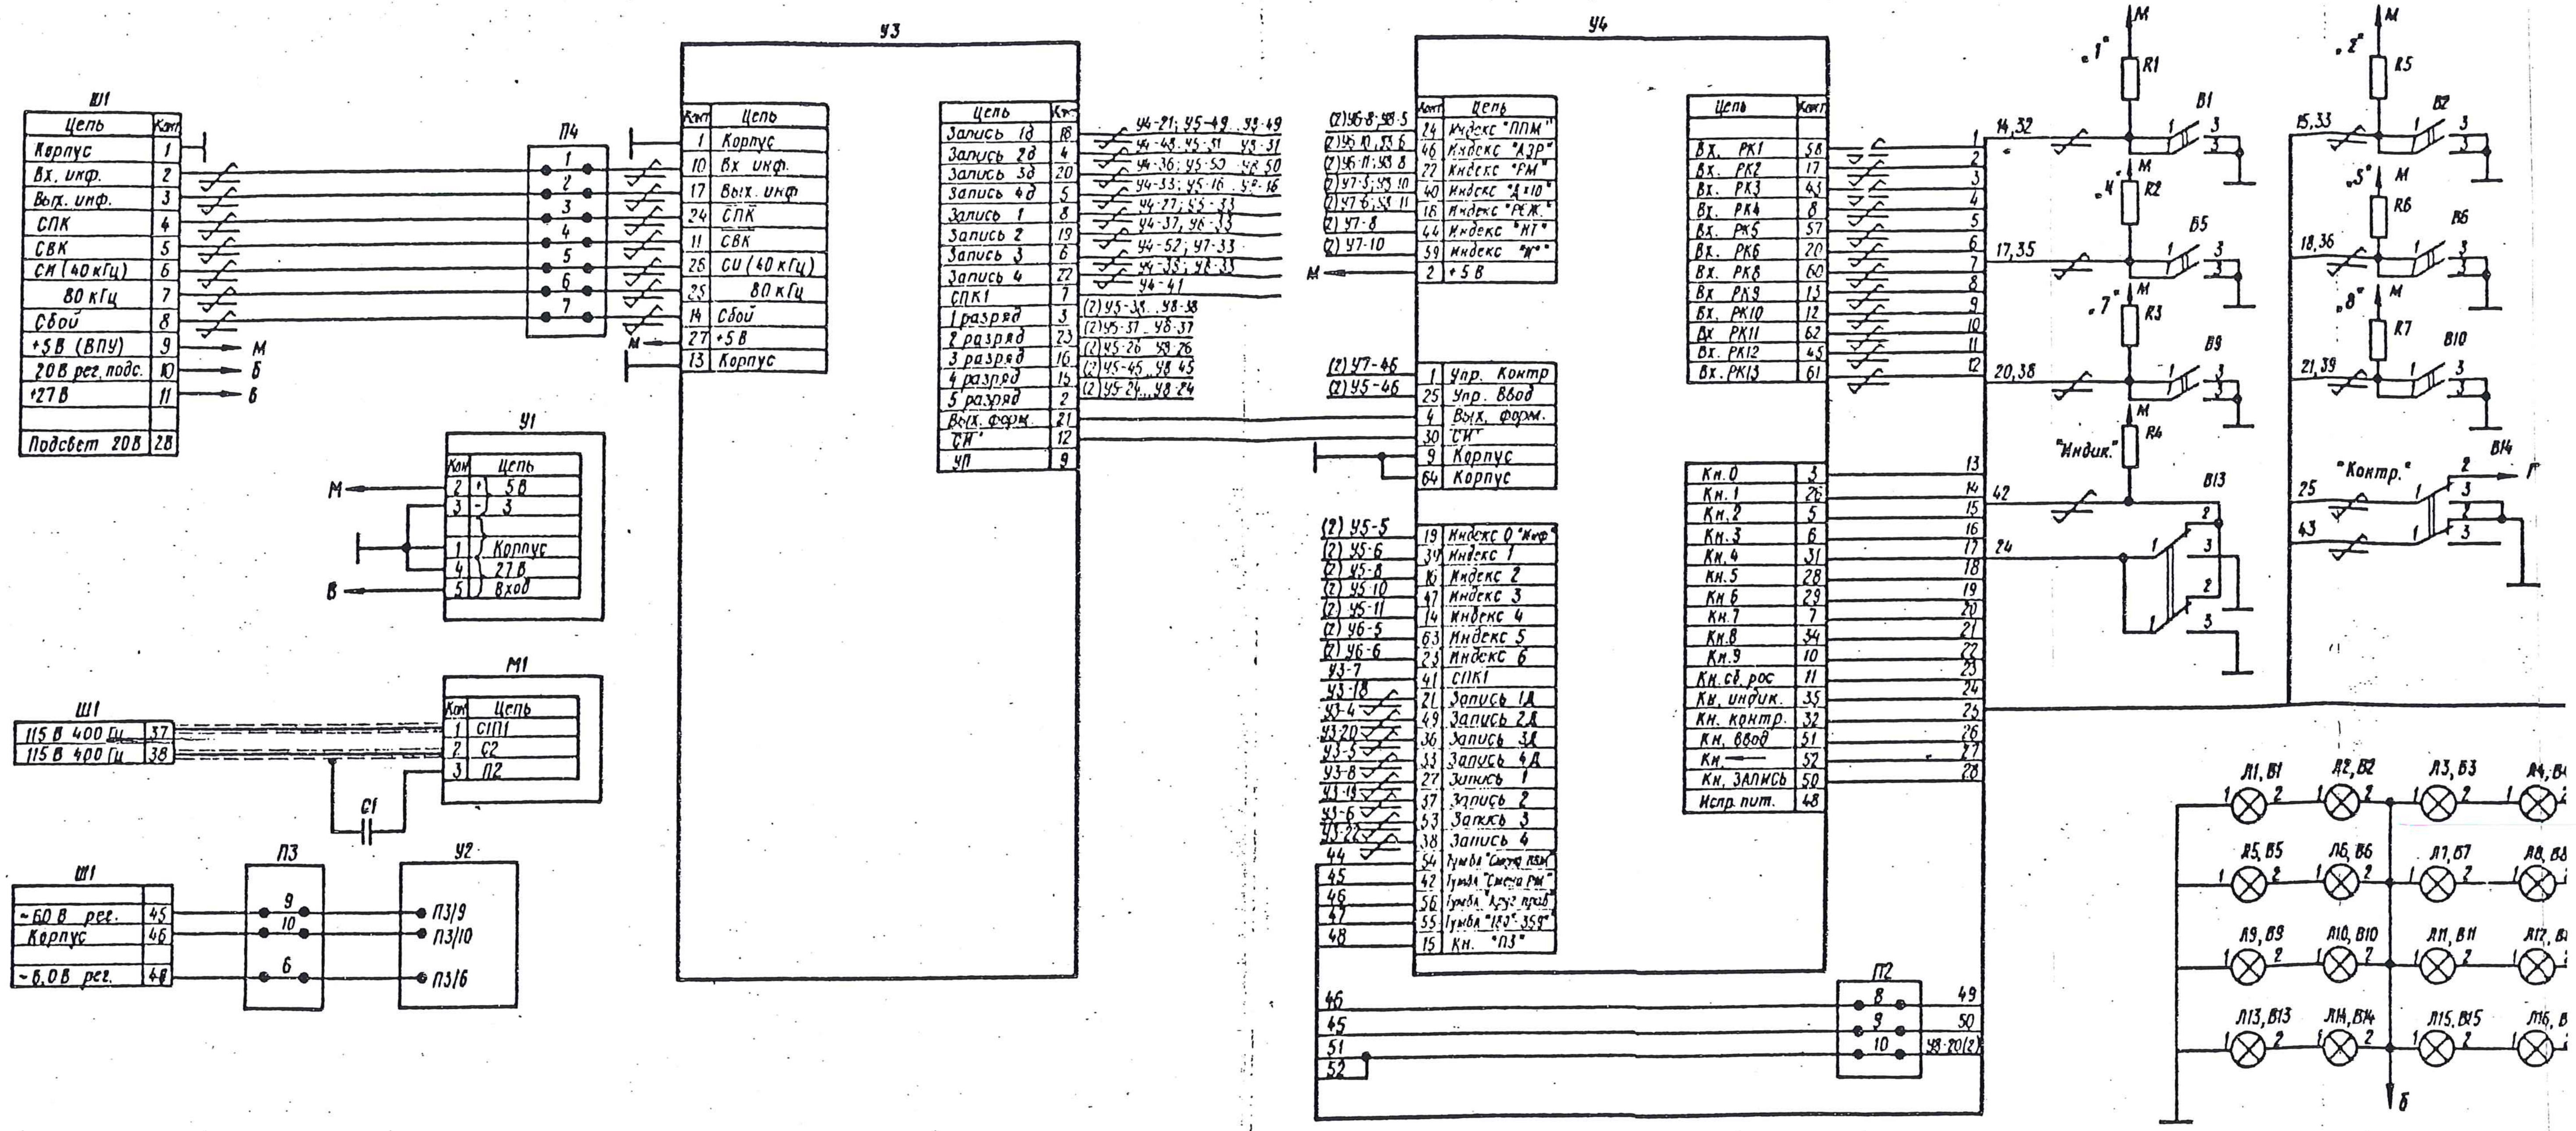

БЛОК А-313-6. СХЕМА ЭЛЕКТРИЧЕСКАЯ ПРИНЦИПИАЛЬНАЯ ЕУ3.624.414 Э3

Рис. 7

(лист 1 из 2)

143

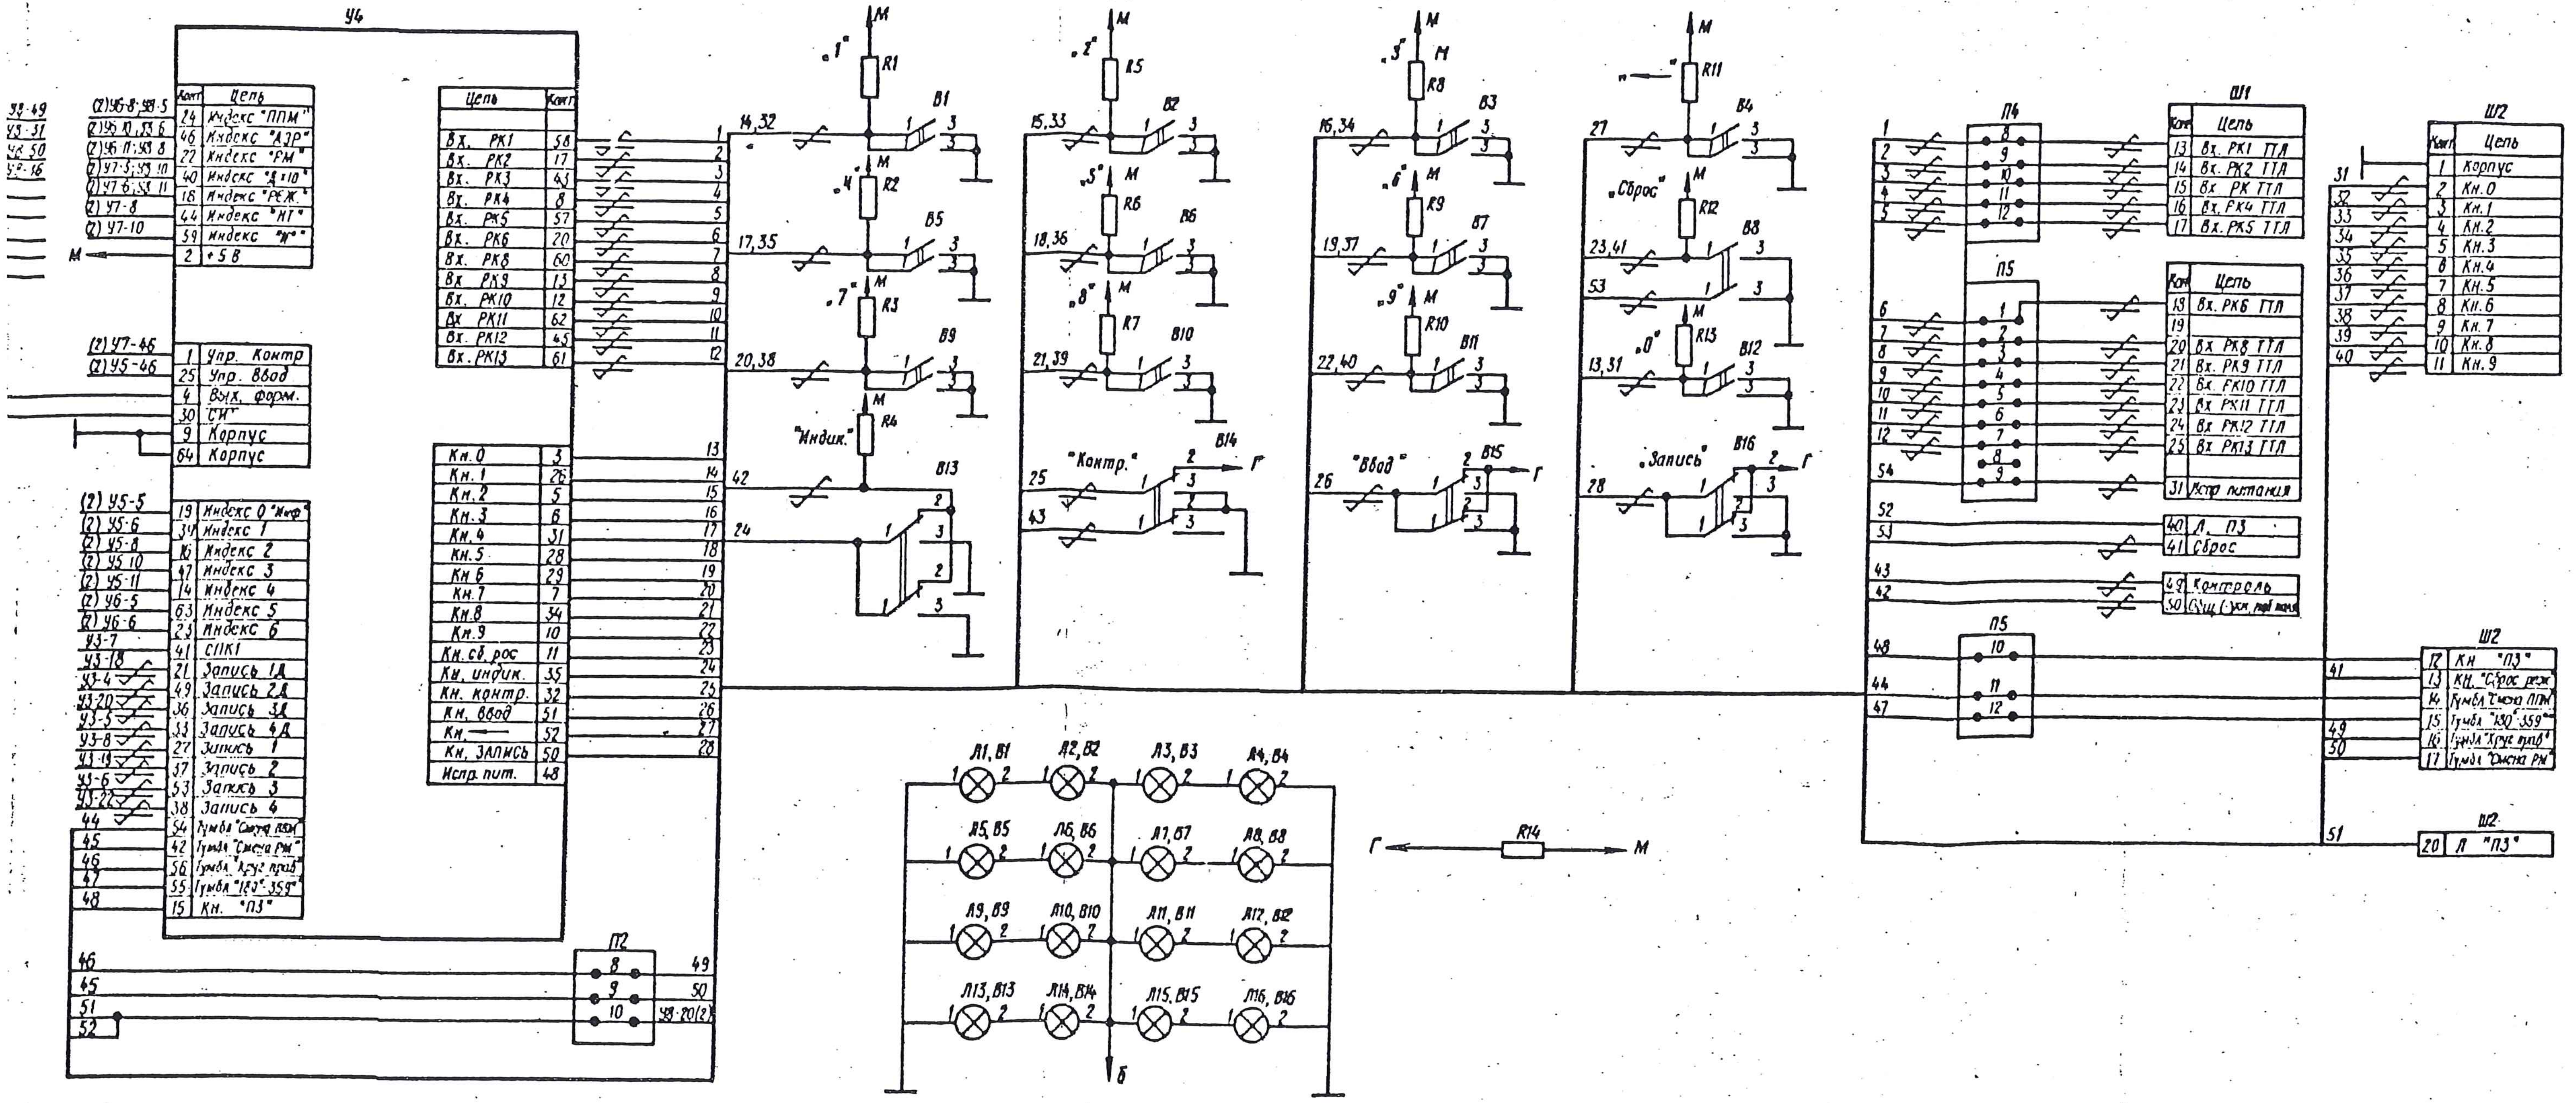
У4
Конт | Цепь
24 Индекс "ППМ"
46 Индекс "АЗР"
22 Индекс "РМ"
40 Индекс "Δ×10"
18 Индекс "РЕЖ."
44 Индекс "НТ"
59 Индекс "ψ"
2 +5 В
(2) У6-8; У8-5
(2) У6-10; У8-6
(2) У6-11; У8-8
(2) У7-5; У8-10
(2) У7-6; У8-11
(2) У7-8
(2) У7-10
У8-49
У8-31
У8-50
У8-16
М
1 Упр. Контр
25 Упр. Ввод
4 Вых. форм.
30 СИ
9 Корпус
64 Корпус
(2) У7-46
(2) У5-46
19 Индекс 0 "Инф"
34 Индекс 1
16 Индекс 2
47 Индекс 3
14 Индекс 4
63 Индекс 5
23 Индекс 6
41 СПКI
21 Запись 1Д
49 Запись 2Д
36 Запись 3Д
33 Запись 4Д
27 Запись 1
37 Запись 2
53 Запись 3
38 Запись 4
54 Тумбл "Смена ППМ"
42 Тумбл "Смена РМ"
56 Тумбл "Круг проб"
55 Тумбл "180°-359°"
15 Кн. "ПЗ"
(2) У5-5
(2) У5-6
(2) У5-8
(2) У5-10
(2) У5-11
(2) У6-5
(2) У6-6
У3-7
У3-18
У3-4
У3-20
У3-5
У3-8
У3-19
У3-6
У3-22
44
45
46
47
48
Цепь | Конт
Вх. РК1 58
Вх. РК2 17
Вх. РК3 43
Вх. РК4 8
Вх. РК5 57
Вх. РК6 20
Вх. РК8 60
Вх. РК9 13
Вх. РК10 12
Вх. РК11 62
Вх. РК12 45
Вх. РК13 61
Кн. 0 3
Кн. 1 26
Кн. 2 5
Кн. 3 6
Кн. 4 31
Кн. 5 28
Кн. 6 29
Кн. 7 7
Кн. 8 34
Кн. 9 10
Кн. сброс 11
Кн. индик. 35
Кн. контр. 32
Кн. ввод 51
Кн. ← 52
Кн. ЗАПИСЬ 50
Испр. пит. 48
П2
8
9
10
46
45
51
52
49
50
У8-20 (2)
"1" R1 В1
"2" R5 В2
"3" R8 В3
"←" R11 В4
"4" R2 В5
"5" R6 В6
"6" R9 В7
"Сброс" R12 В8
"7" R3 В9
"8" R7 В10
"9" R10 В11
"0" R13 В12
"Индик." R4 В13
"Контр." В14
"Ввод" В15
"Запись" В16
14,32
17,35
20,38
15,33
18,36
21,39
16,34
19,37
22,40
27
23,41
53
13,31
42
24
25
43
26
28
М
Г
Л1, В1
Л2, В2
Л3, В3
Л4, В4
Л5, В5
Л6, В6
Л7, В7
Л8, В8
Л9, В9
Л10, В10
Л11, В11
Л12, В12
Л13, В13
Л14, В14
Л15, В15
Л16, В16
Б
Г R14 М
П4
П5
Ш1
Конт | Цепь
13 Вх. РК1 ТТЛ
14 Вх. РК2 ТТЛ
15 Вх. РК ТТЛ
16 Вх. РК4 ТТЛ
17 Вх. РК5 ТТЛ
18 Вх. РК6 ТТЛ
19
20 Вх. РК8 ТТЛ
21 Вх. РК9 ТТЛ
22 Вх. РК10 ТТЛ
23 Вх. РК11 ТТЛ
24 Вх. РК12 ТТЛ
25 Вх. РК13 ТТЛ
31 Испр питания
40 Л. ПЗ
41 Сброс
49 Контроль
50 Сущ (-)уст. питания
Ш2
Конт | Цепь
1 Корпус
2 Кн. 0
3 Кн. 1
4 Кн. 2
5 Кн. 3
6 Кн. 4
7 Кн. 5
8 Кн. 6
9 Кн. 7
10 Кн. 8
11 Кн. 9
12 Кн "ПЗ"
13 Кн. "Сброс реж"
14 Тумбл "Смена ППМ"
15 Тумбл "180°-359°"
16 Тумбл "Круг проб"
17 Тумбл "Смена РМ"
20 Л "ПЗ"

149/2