
И ЭКСПЛУАТАЦИИ

	Кол.	Примечание
	1	
	2	
	4	
	10	
	2	
	12	
	5	
	1	
ТУ	1	
ТУ	1	

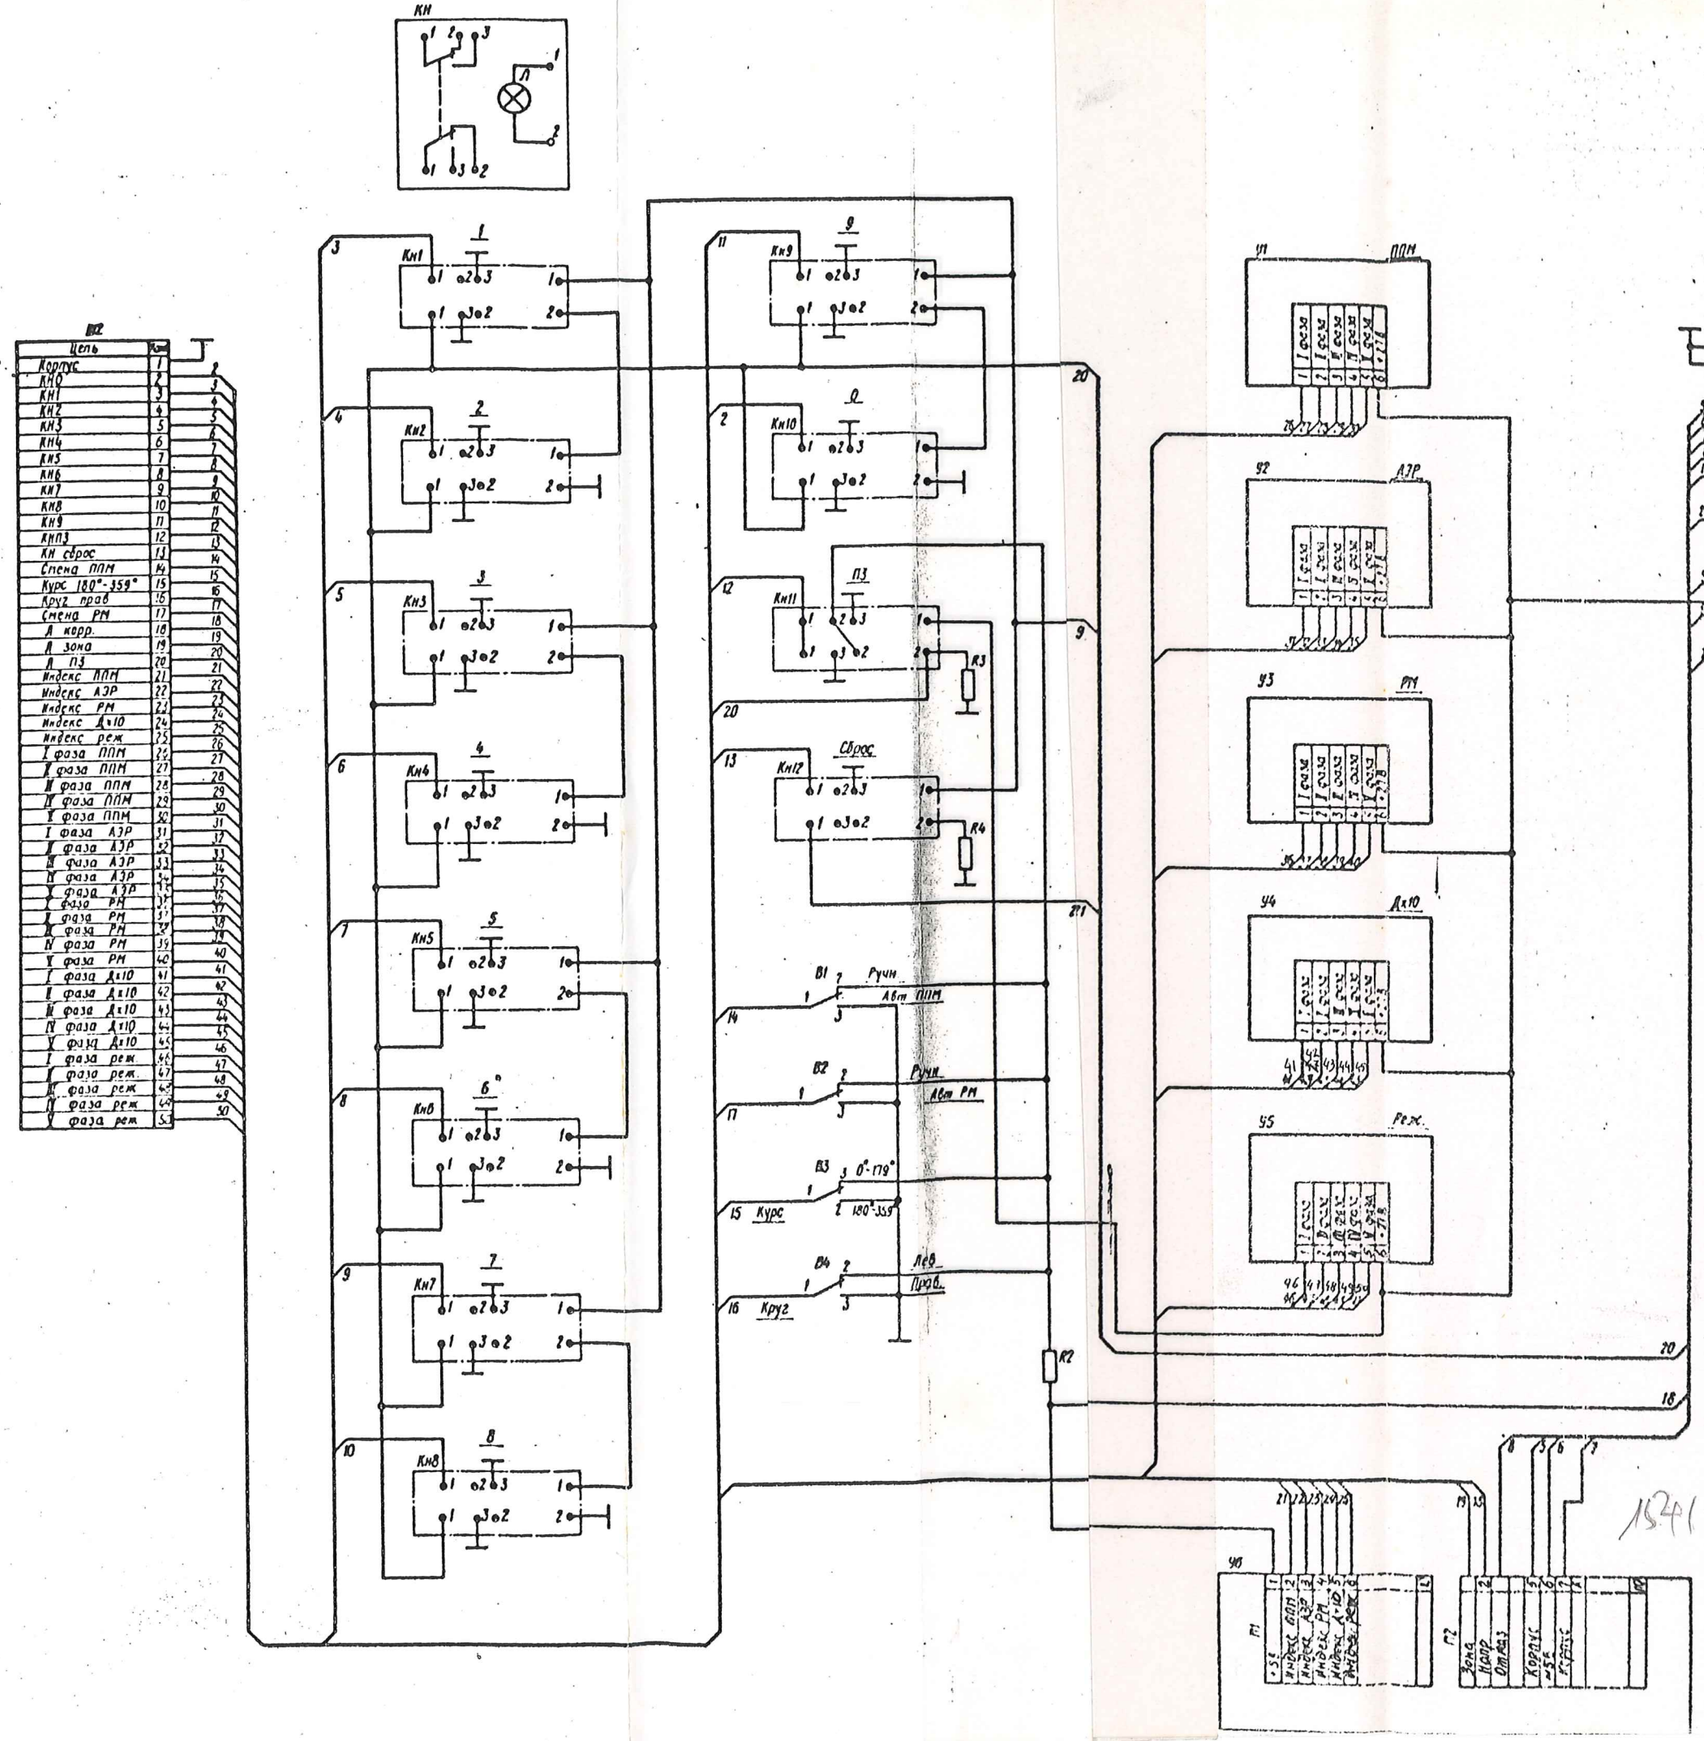

15411