
А-313
РУКОВОДСТВО ПО ТЕХНИЧЕСКОЙ ЭКСПЛУАТАЦИИ

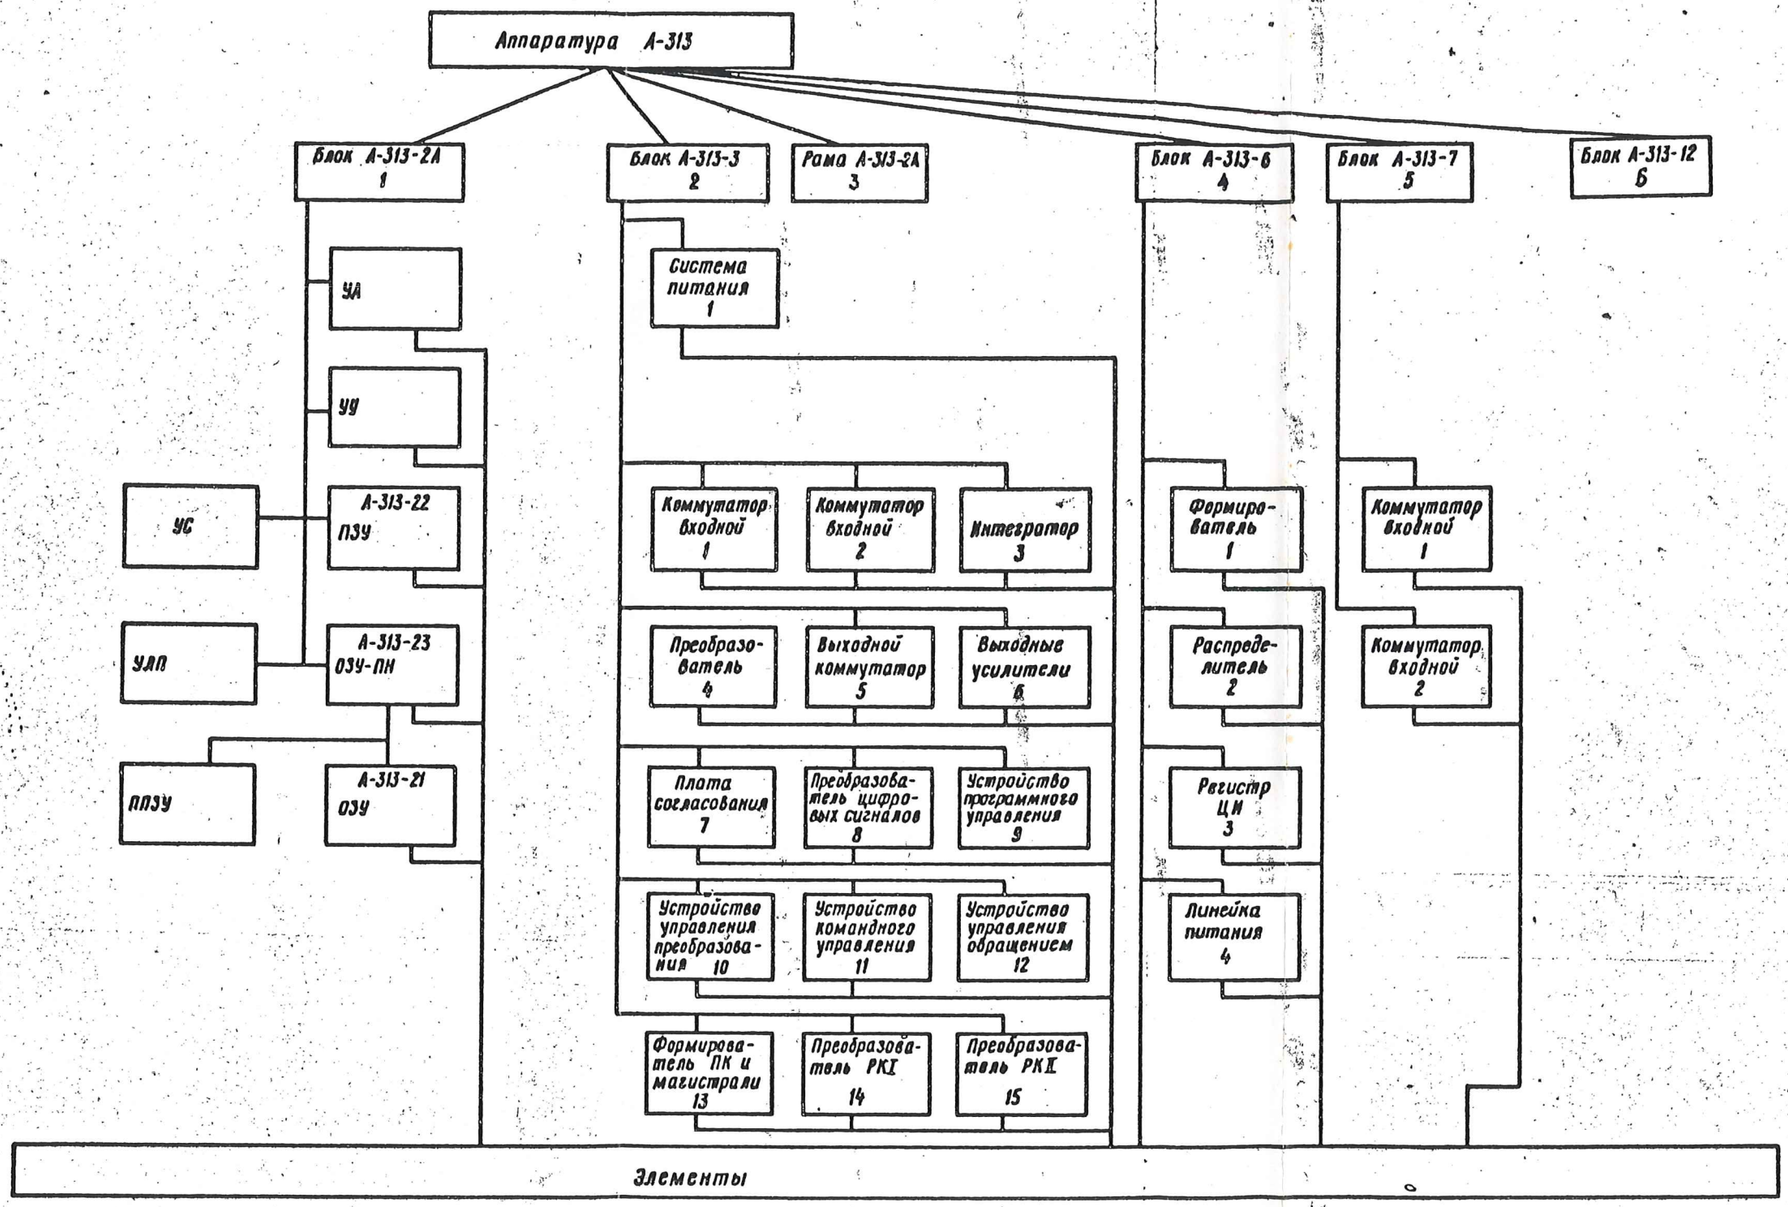

СТРУКТУРНОЕ ПОСТРОЕНИЕ КОМПЛЕКТАЦИИ
ЕУ1.247.199-09

Рис. 4

24