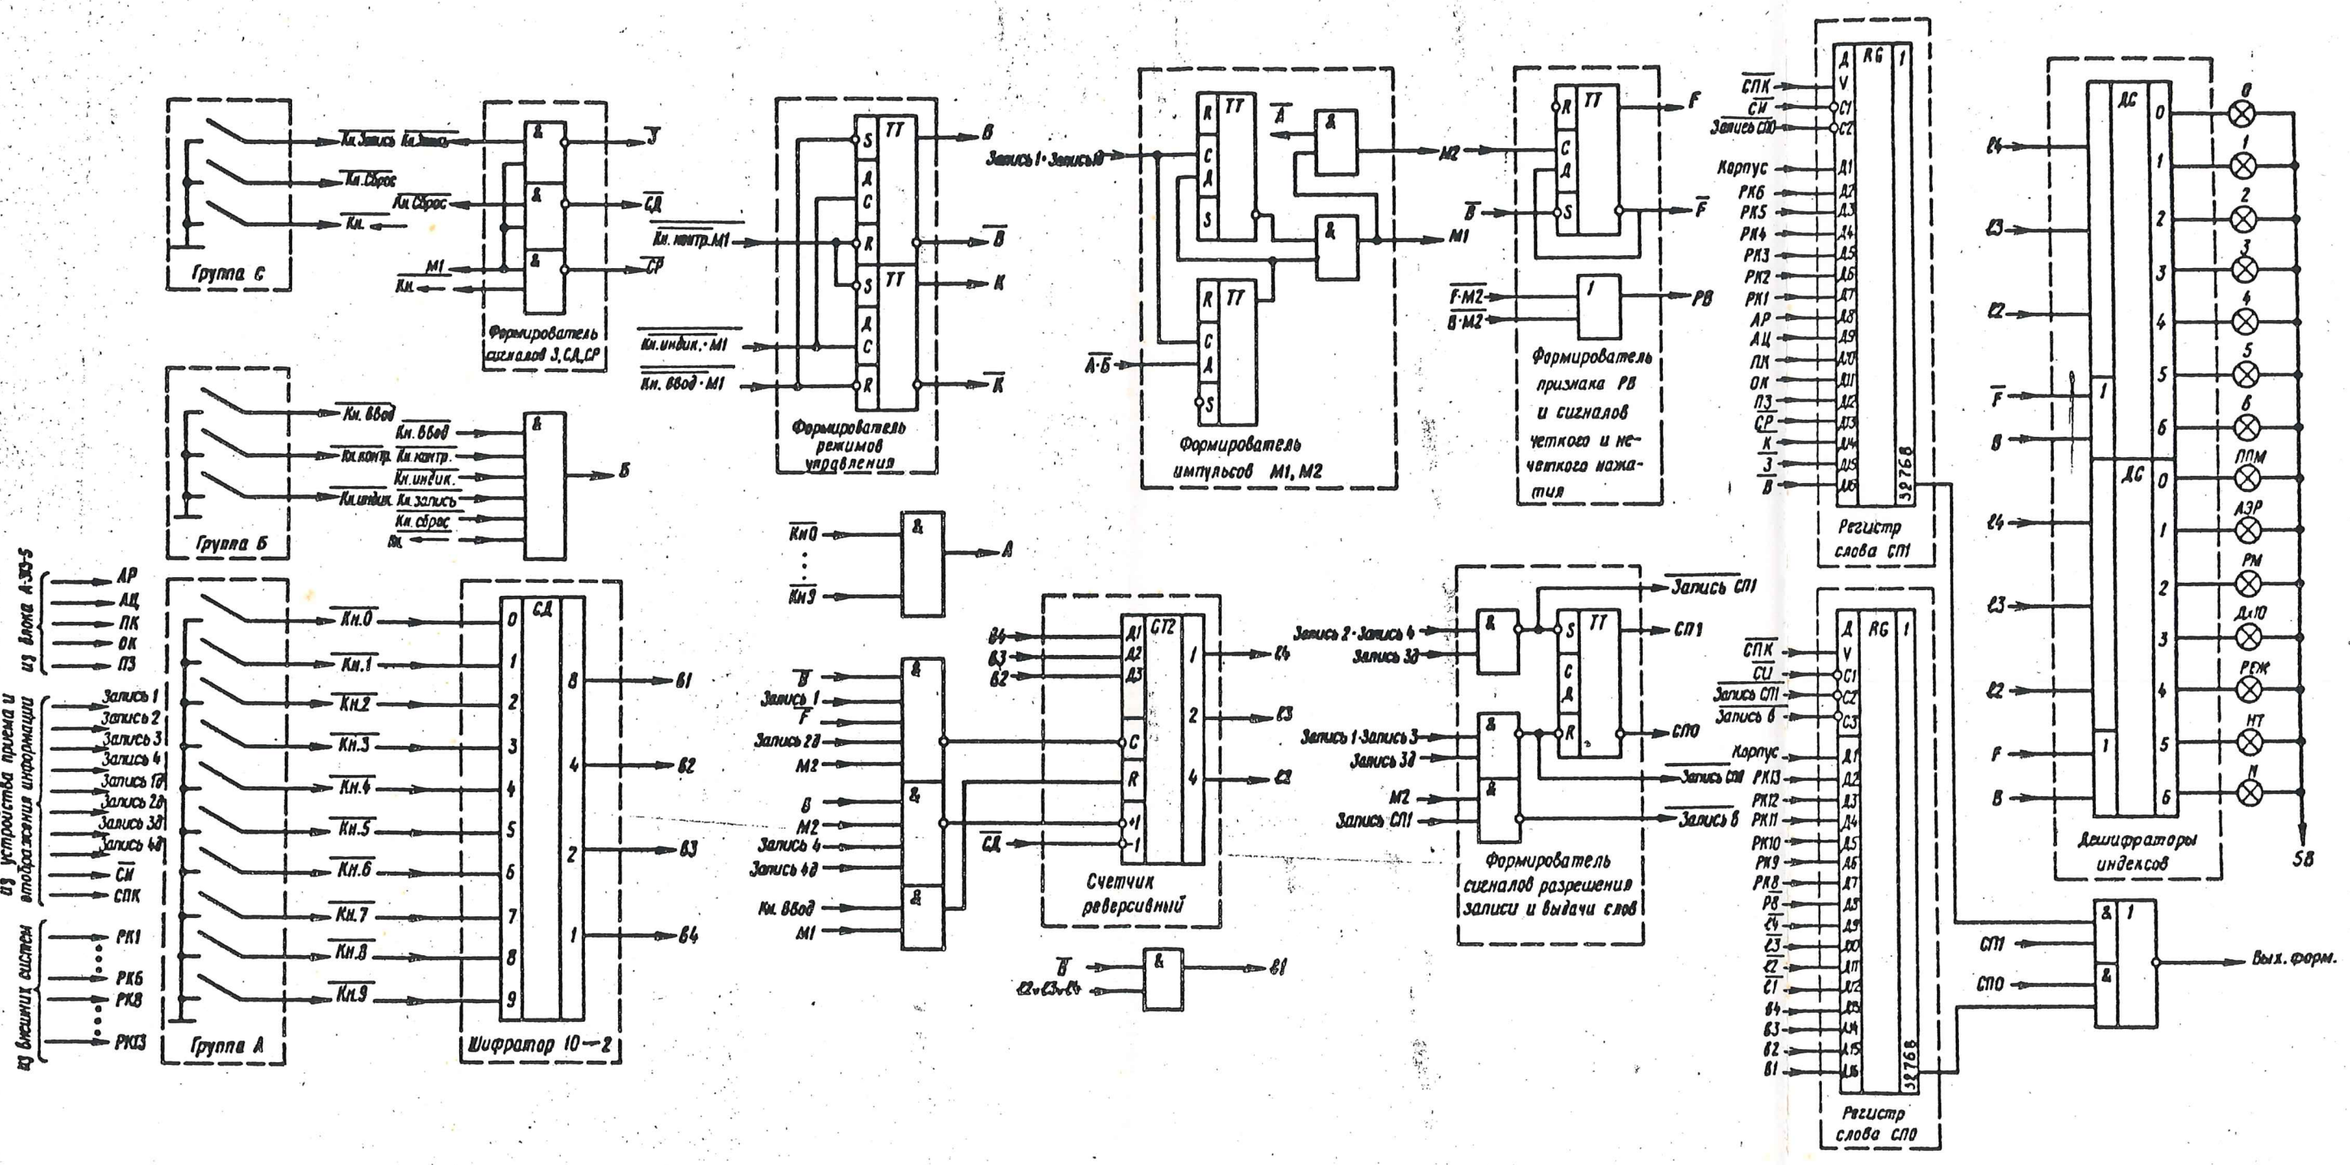


УСТРОЙСТВО ФОРМИРОВАНИЯ И ВЫДАЧИ ИНФОРМАЦИИ.
СХЕМА ЭЛЕКТРИЧЕСКАЯ ФУНКЦИОНАЛЬНАЯ

Рис. 15