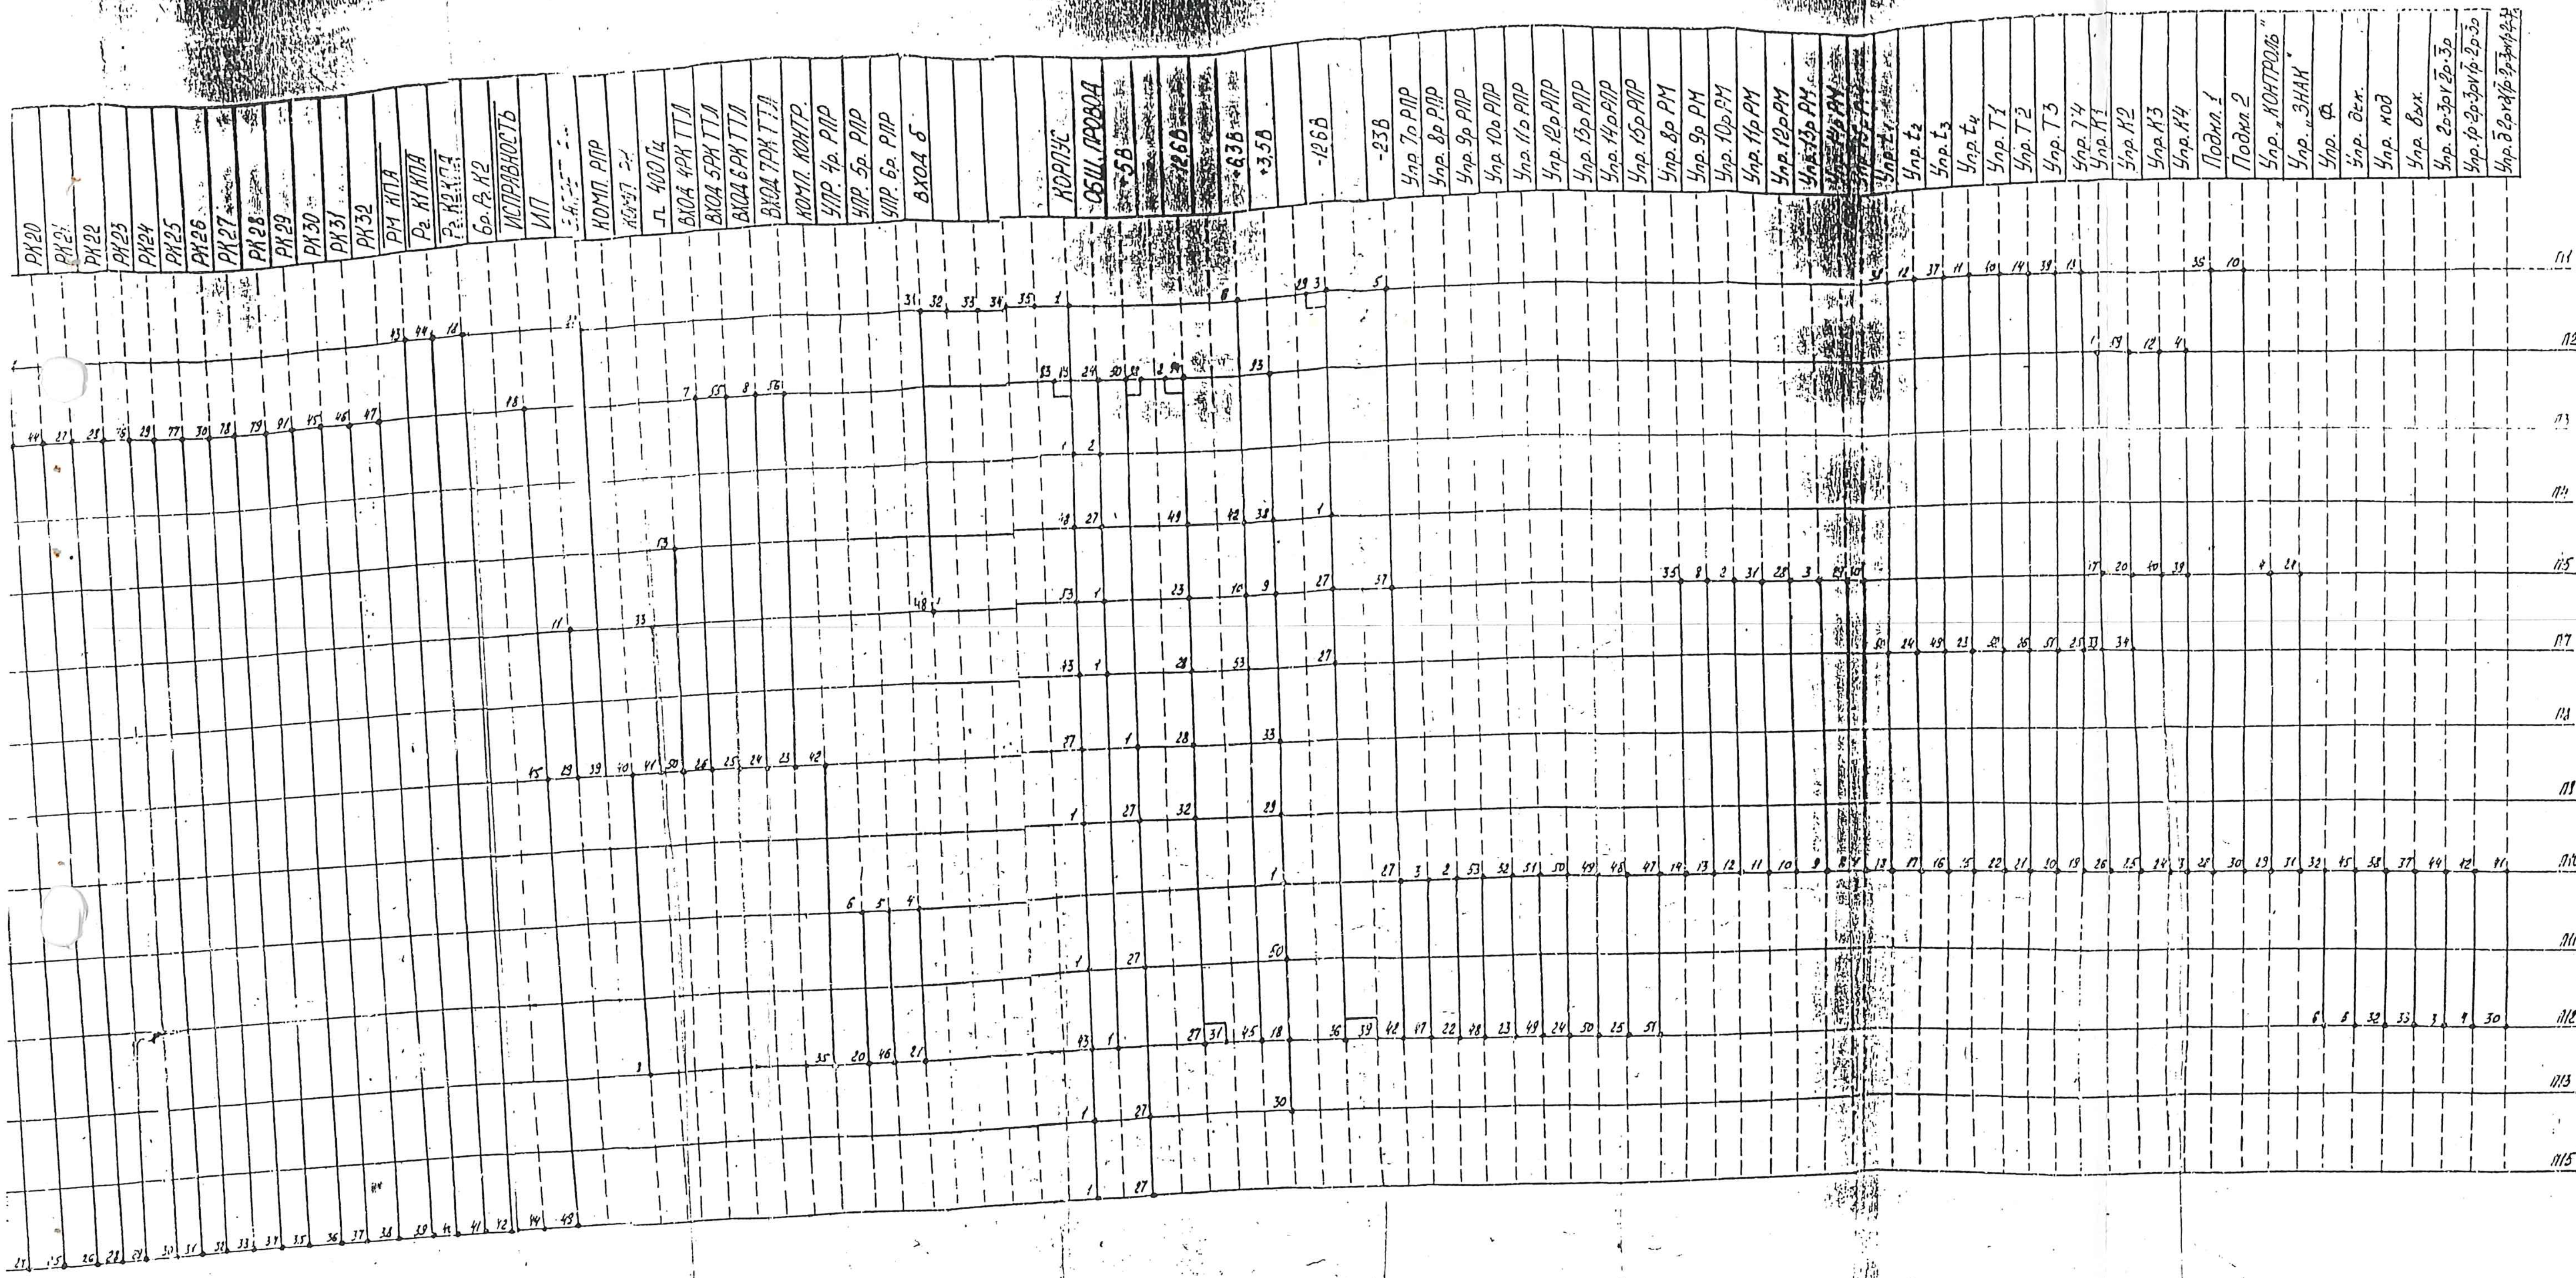

РК20
РК21
РК22
РК23
РК24
РК25
РК26
РК27
РК28
РК29
РК30
РК31
РК32
РМ КПА
Р2 К1 КПА
Р2 К2 КПА
Бр. Р2 К2
ИСПРАВНОСТЬ
ИП
КОМП. РПР
КОМП. РМ
⊓ 400Гц
ВХОД 4РК ТТЛ
ВХОД 5РК ТТЛ
ВХОД 6РК ТТЛ
ВХОД 7РК ТТЛ
КОМП. КОНТР.
УПР. 4р. РПР
УПР. 5р. РПР
УПР. 6р. РПР
ВХОД б
КОРПУС
ОБЩ. ПРОВОД
+5В
+12,6В
+6,3В
+3,5В
-12,6В
-23В
Упр. 7р РПР
Упр. 8р РПР
Упр. 9р РПР
Упр. 10р РПР
Упр. 11р РПР
Упр. 12р РПР
Упр. 13р РПР
Упр. 14р РПР
Упр. 15р РПР
Упр. 8р РМ
Упр. 9р РМ
Упр. 10р РМ
Упр. 11р РМ
Упр. 12р РМ
Упр. 13р РМ
Упр. 14р РМ
Упр. 15р РМ
Упр. t1
Упр. t2
Упр. t3
Упр. t4
Упр. Т1
Упр. Т2
Упр. Т3
Упр. Т4
Упр. К1
Упр. К2
Упр. К3
Упр. К4
Подкл. 1
Подкл. 2
Упр. „КОНТРОЛЬ"
Упр. „ЗНАК"
Упр. Ф
Упр. вых.
Упр. код
Упр. вых.
Упр. 2р·3р∨2р·3р
Упр. 1р·2р·3р∨1р·2р·3р
Упр. 2р∨2р(1р·2р·3р∨1р·2р·3р)
П1
П2
П3
П4
П5
П7
П8
П9
П10
П11
П12
П13
П15

(Продолжение см на листе 3)

10

23.0
ожени
.1?/2
.22/8