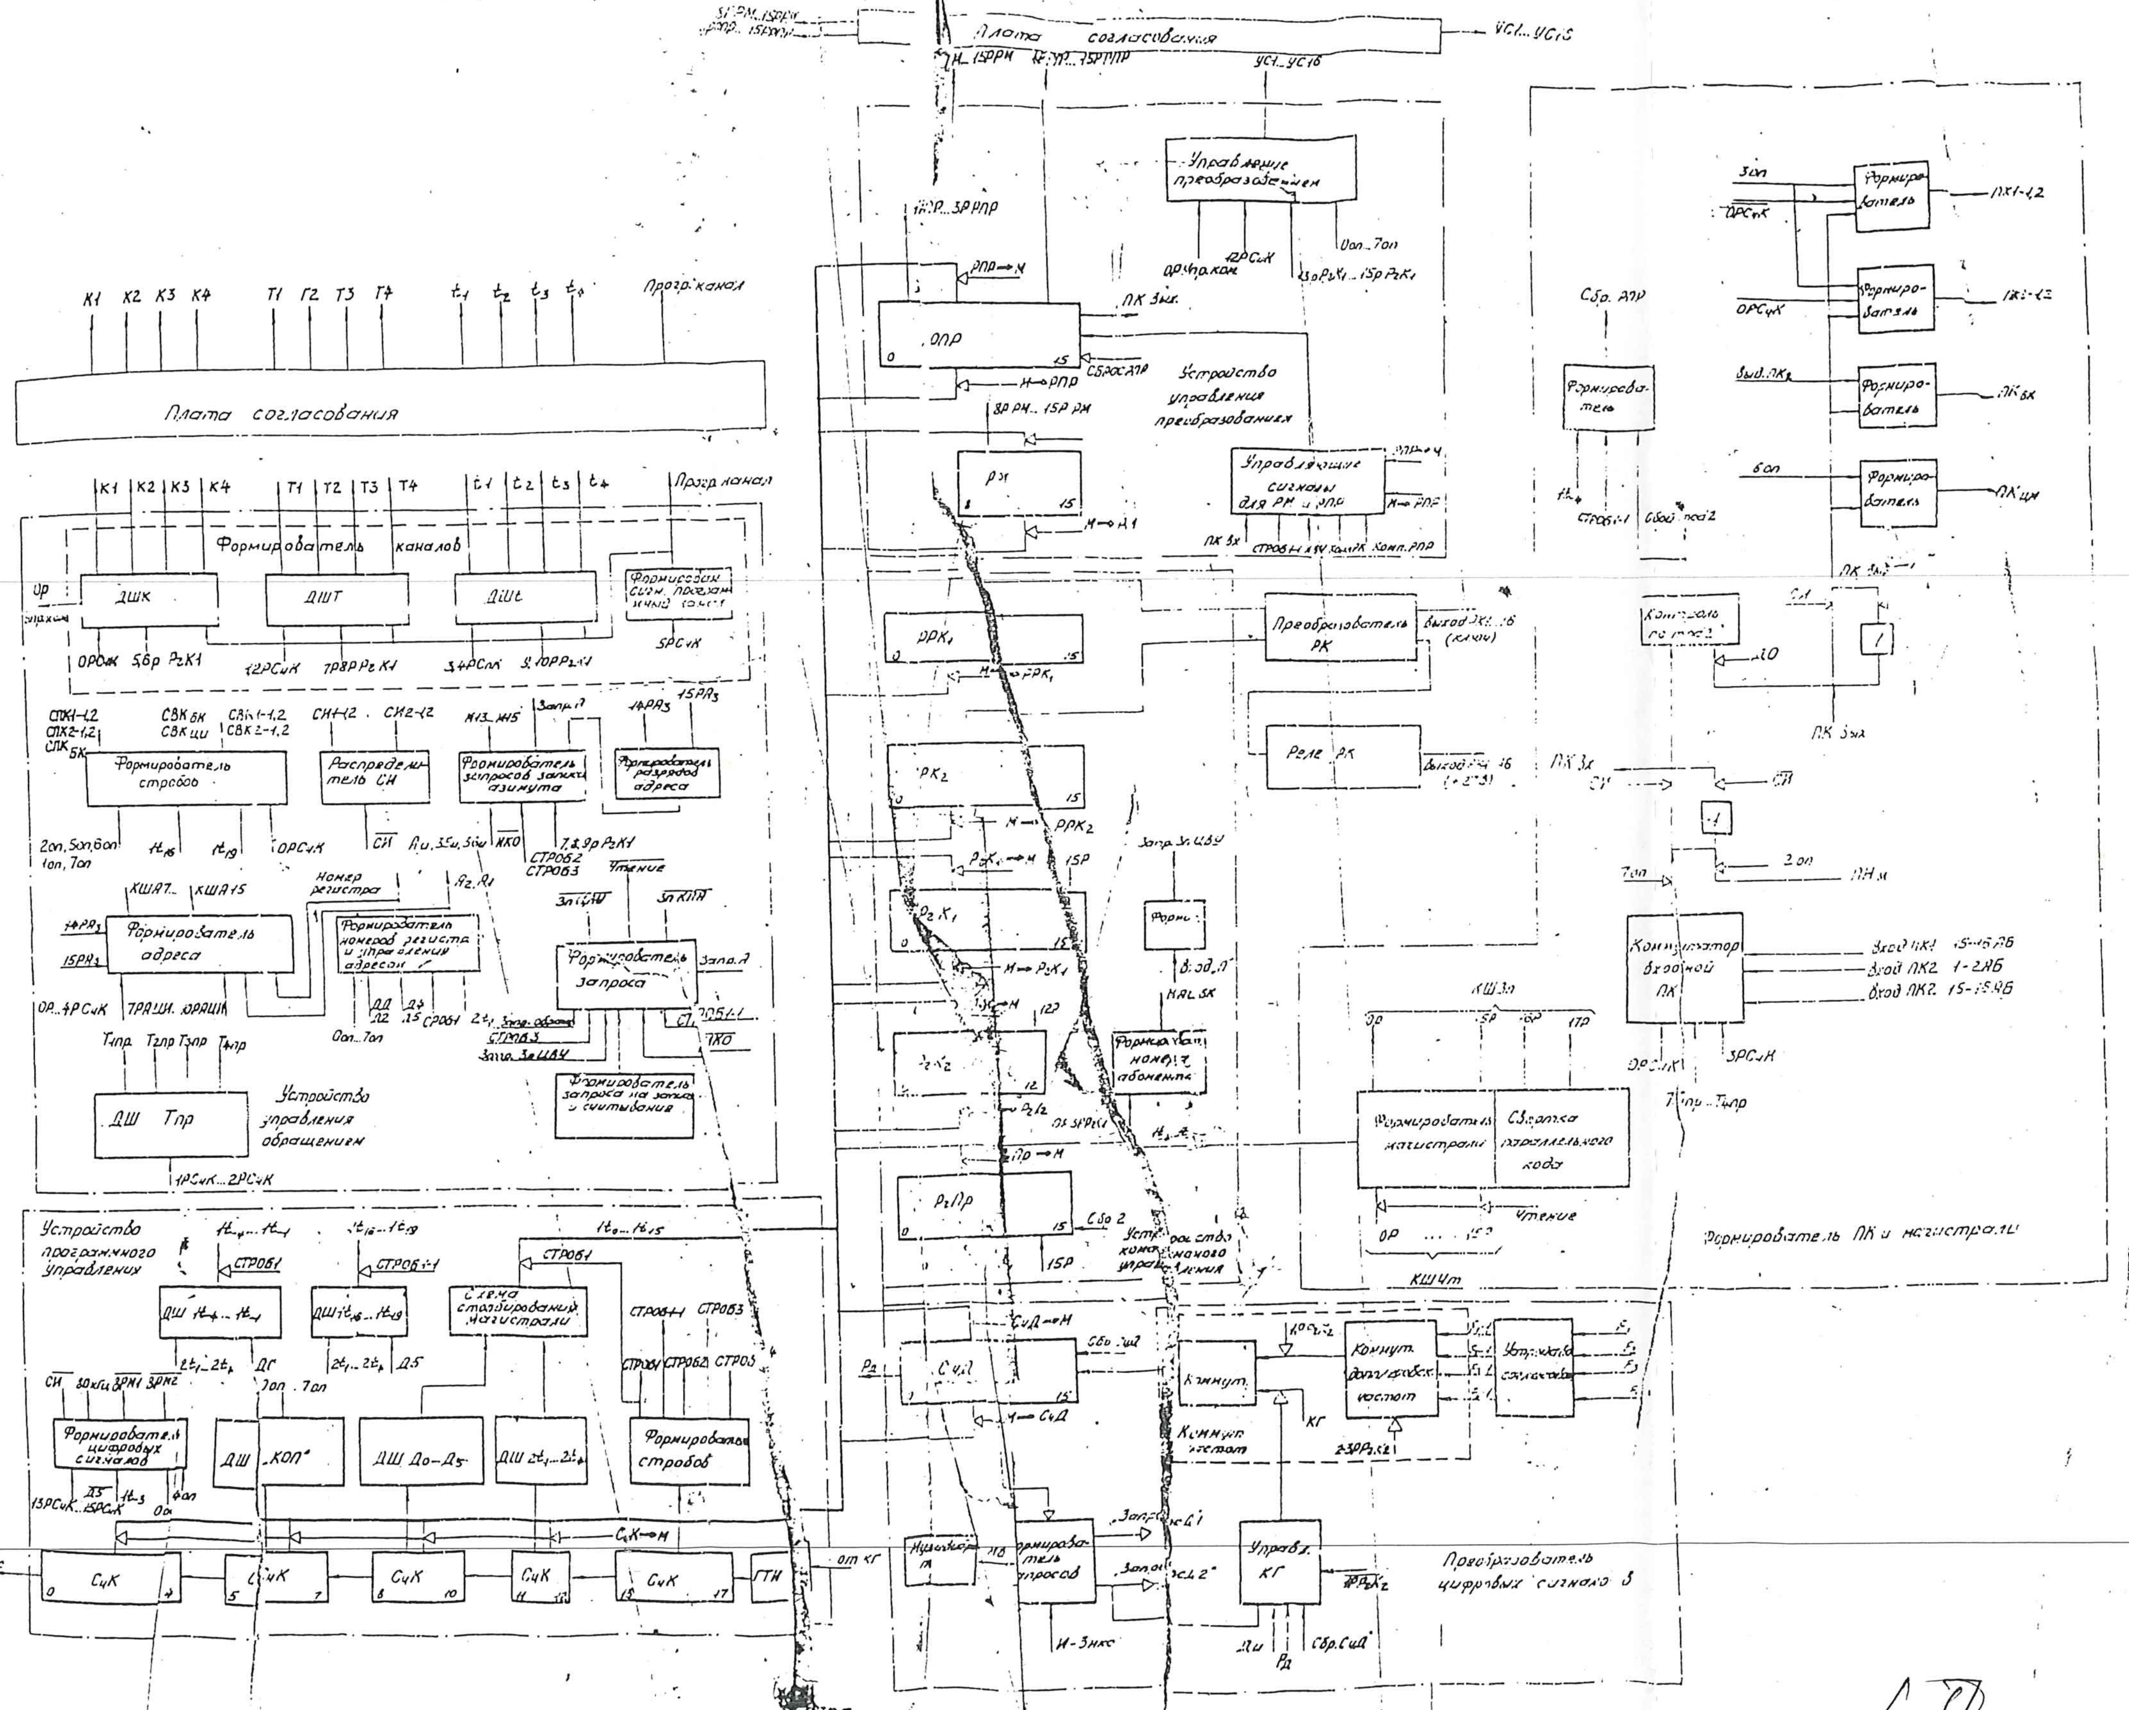
К1 К2 К3 К4
Т1 Т2 Т3 Т4
t1 t2 t3 t4
Прогр. канал
Плата согласования
Формирователь каналов
ДШК
ДШТ
ДШt
Формирователь стробов
Распределитель СИ
Формирователь запросов записи азимута
Формирователь разрядов адреса
Формирователь адреса
Формирователь номеров регистра и управление адресом
Формирователь запроса
Формирователь запроса на запись и считывание
ДШ Тпр
Устройство управления обращением
Устройство программного управления
Схема стробирования магистрали
Формирователь цифровых сигналов
ДШ КОП
ДШ Д0–Д5
Формирователь стробов
СчК
ГТИ
Плата согласования
Управление преобразователей
ОПР
Устройство управления преобразованием
РН
Управляющие сигналы для РН и ОПР
РРК1
Преобразователь РК
РРК2
Реле РК
Р2К1
Р2К2
Р2Пр
Формирователь номера абонента
Устройство командного управления
СчД
Коммутатор
Коммутатор достоверности
Устройство согласования
Формирователь запросов
Управл. КГ
Преобразователь цифровых сигналов
Формирователь
Контроль
Коммутатор входной ЛК
Формирователь магистрали
Сборка параллельного кода
Формирователь ЛК и магистрали
ЛК1-1,2
ЛК2-1,2
ЛК бк
ЛК ци
Вход ЛК1 15-16 РБ
Вход ЛК2 1-2 РБ
Вход ЛК2 15-16 РБ
КШЗп
КШЧт
Чтение

Схема электрическая функциональная

Рис.I

68

68

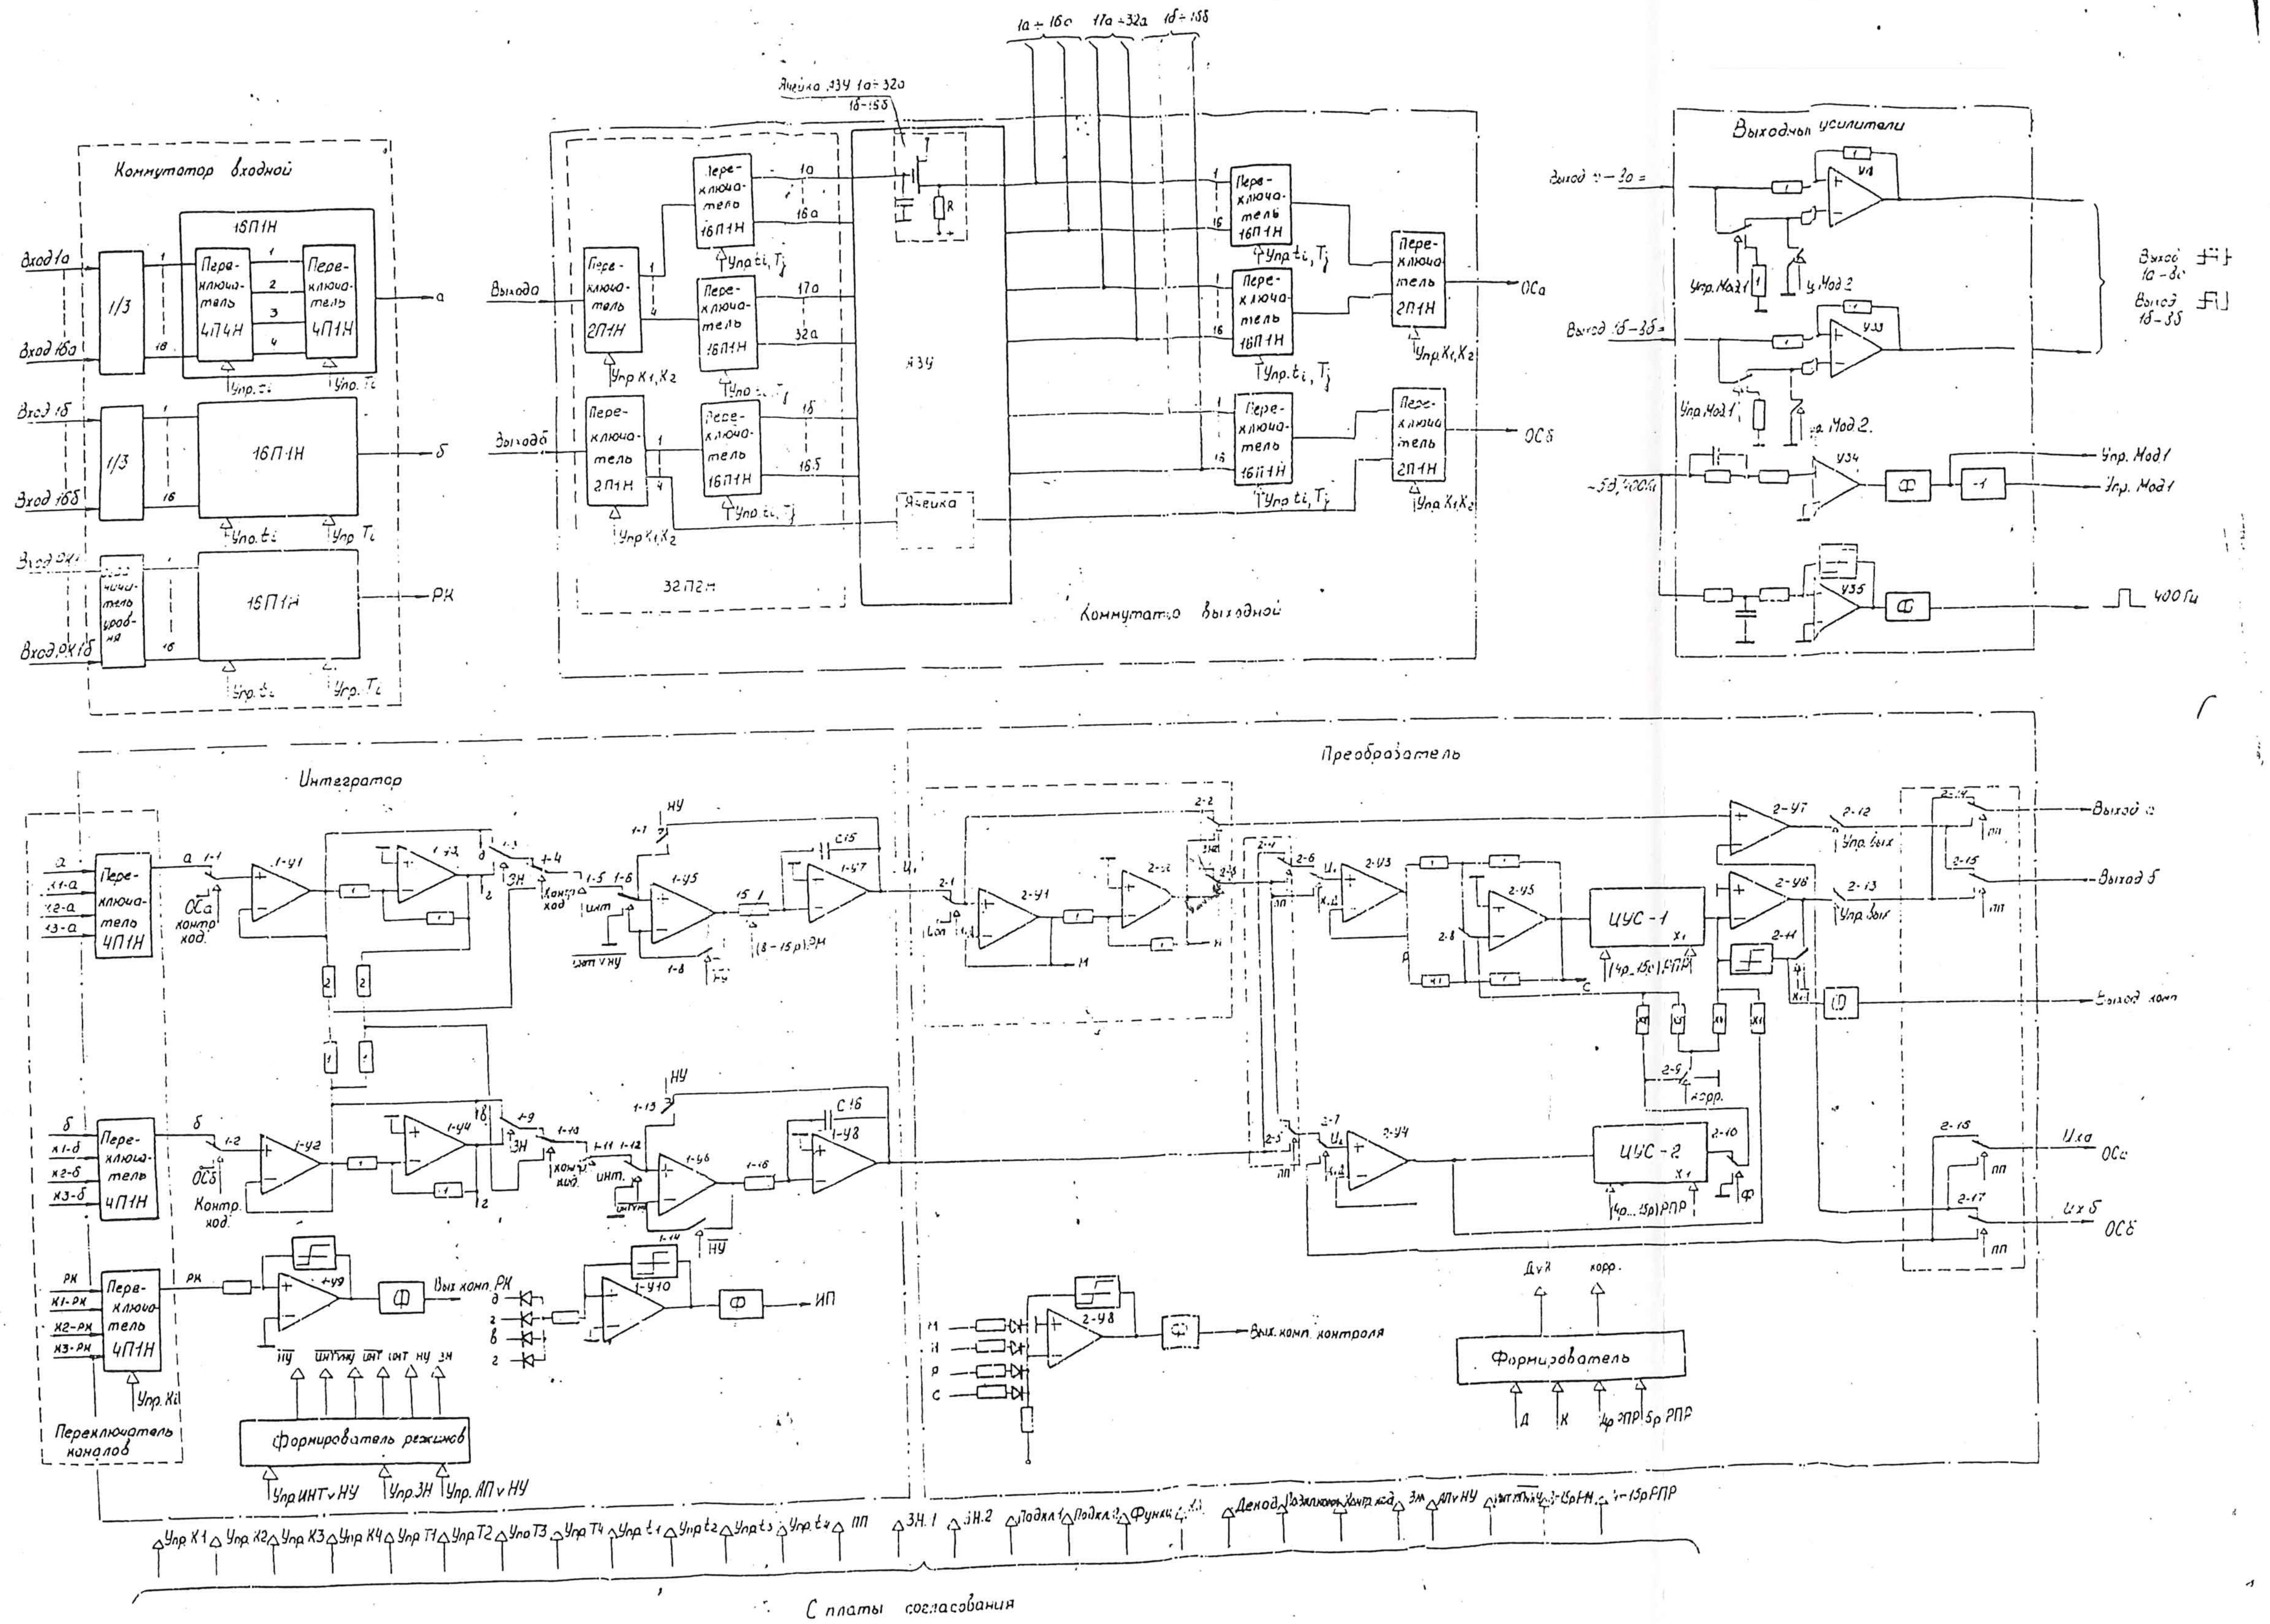
Коммутатор входной
Вход 1а
Вход 16а
Вход 1б
Вход 16б
Вход РК
Вход РК16
1/3
Переключатель 4П4Н
Переключатель 4П1Н
16П1Н
Упр. Ti
Упр. ti
а
б
РК
Выход а
Выход б
Переключатель 2П1Н
Переключатель 16П1Н
Упр K1, K2
Упр ti, Tj
Ячейка 334 1а÷32а 1б÷15б
334
Ячейка
32П2Н
1а ÷ 16а
17а ÷ 32а
1б ÷ 15б
Коммутатор выходной
ОСа
ОСб
Выходные усилители
Выход 1а ÷ 32а
Выход 1б ÷ 35б
У1
У33
У34
У35
Упр. Мод 1
Упр. Мод 2
Выход 1а-32а
Выход 1б-35б
–5В, 400Гц
Ф
400 Гц
Интегратор
Преобразователь
Переключатель 4П1Н
ОСа
ОСб
Контр. ход
1-У1
1-У2
1-У3
1-У4
1-У5
1-У6
1-У7
1-У8
1-У9
1-У10
НУ
ЗН
Инт
С15
С16
Вых конт. РК
ИП
Формирователь режимов
Упр ИНТ v НУ
Упр ЗН
Упр. ЯП v НУ
Переключатель каналов
Упр. Ki
2-У1
2-У2
2-У3
2-У4
2-У5
2-У6
2-У7
2-У8
ЦУС-1
ЦУС-2
Выход а
Выход б
Выход конт
Uвх а
Uвх б
ОСа
ОСб
Вых. конт. контроля
Формирователь
Дуя
корр.
С платы согласования
Упр К1
Упр К2
Упр К3
Упр К4
Упр Т1
Упр Т2
Упр Т3
Упр Т4
Упр t1
Упр t2
Упр t3
Упр t4
ПП
ЗН.1
ЗН.2
Подкл.1
Подкл.2
Функц.
Декод.
Контр. код
ЯП v НУ

Устройства цифро-аналоговых преобразований
Схема электрическая функциональная
Рис.2

2

68

68

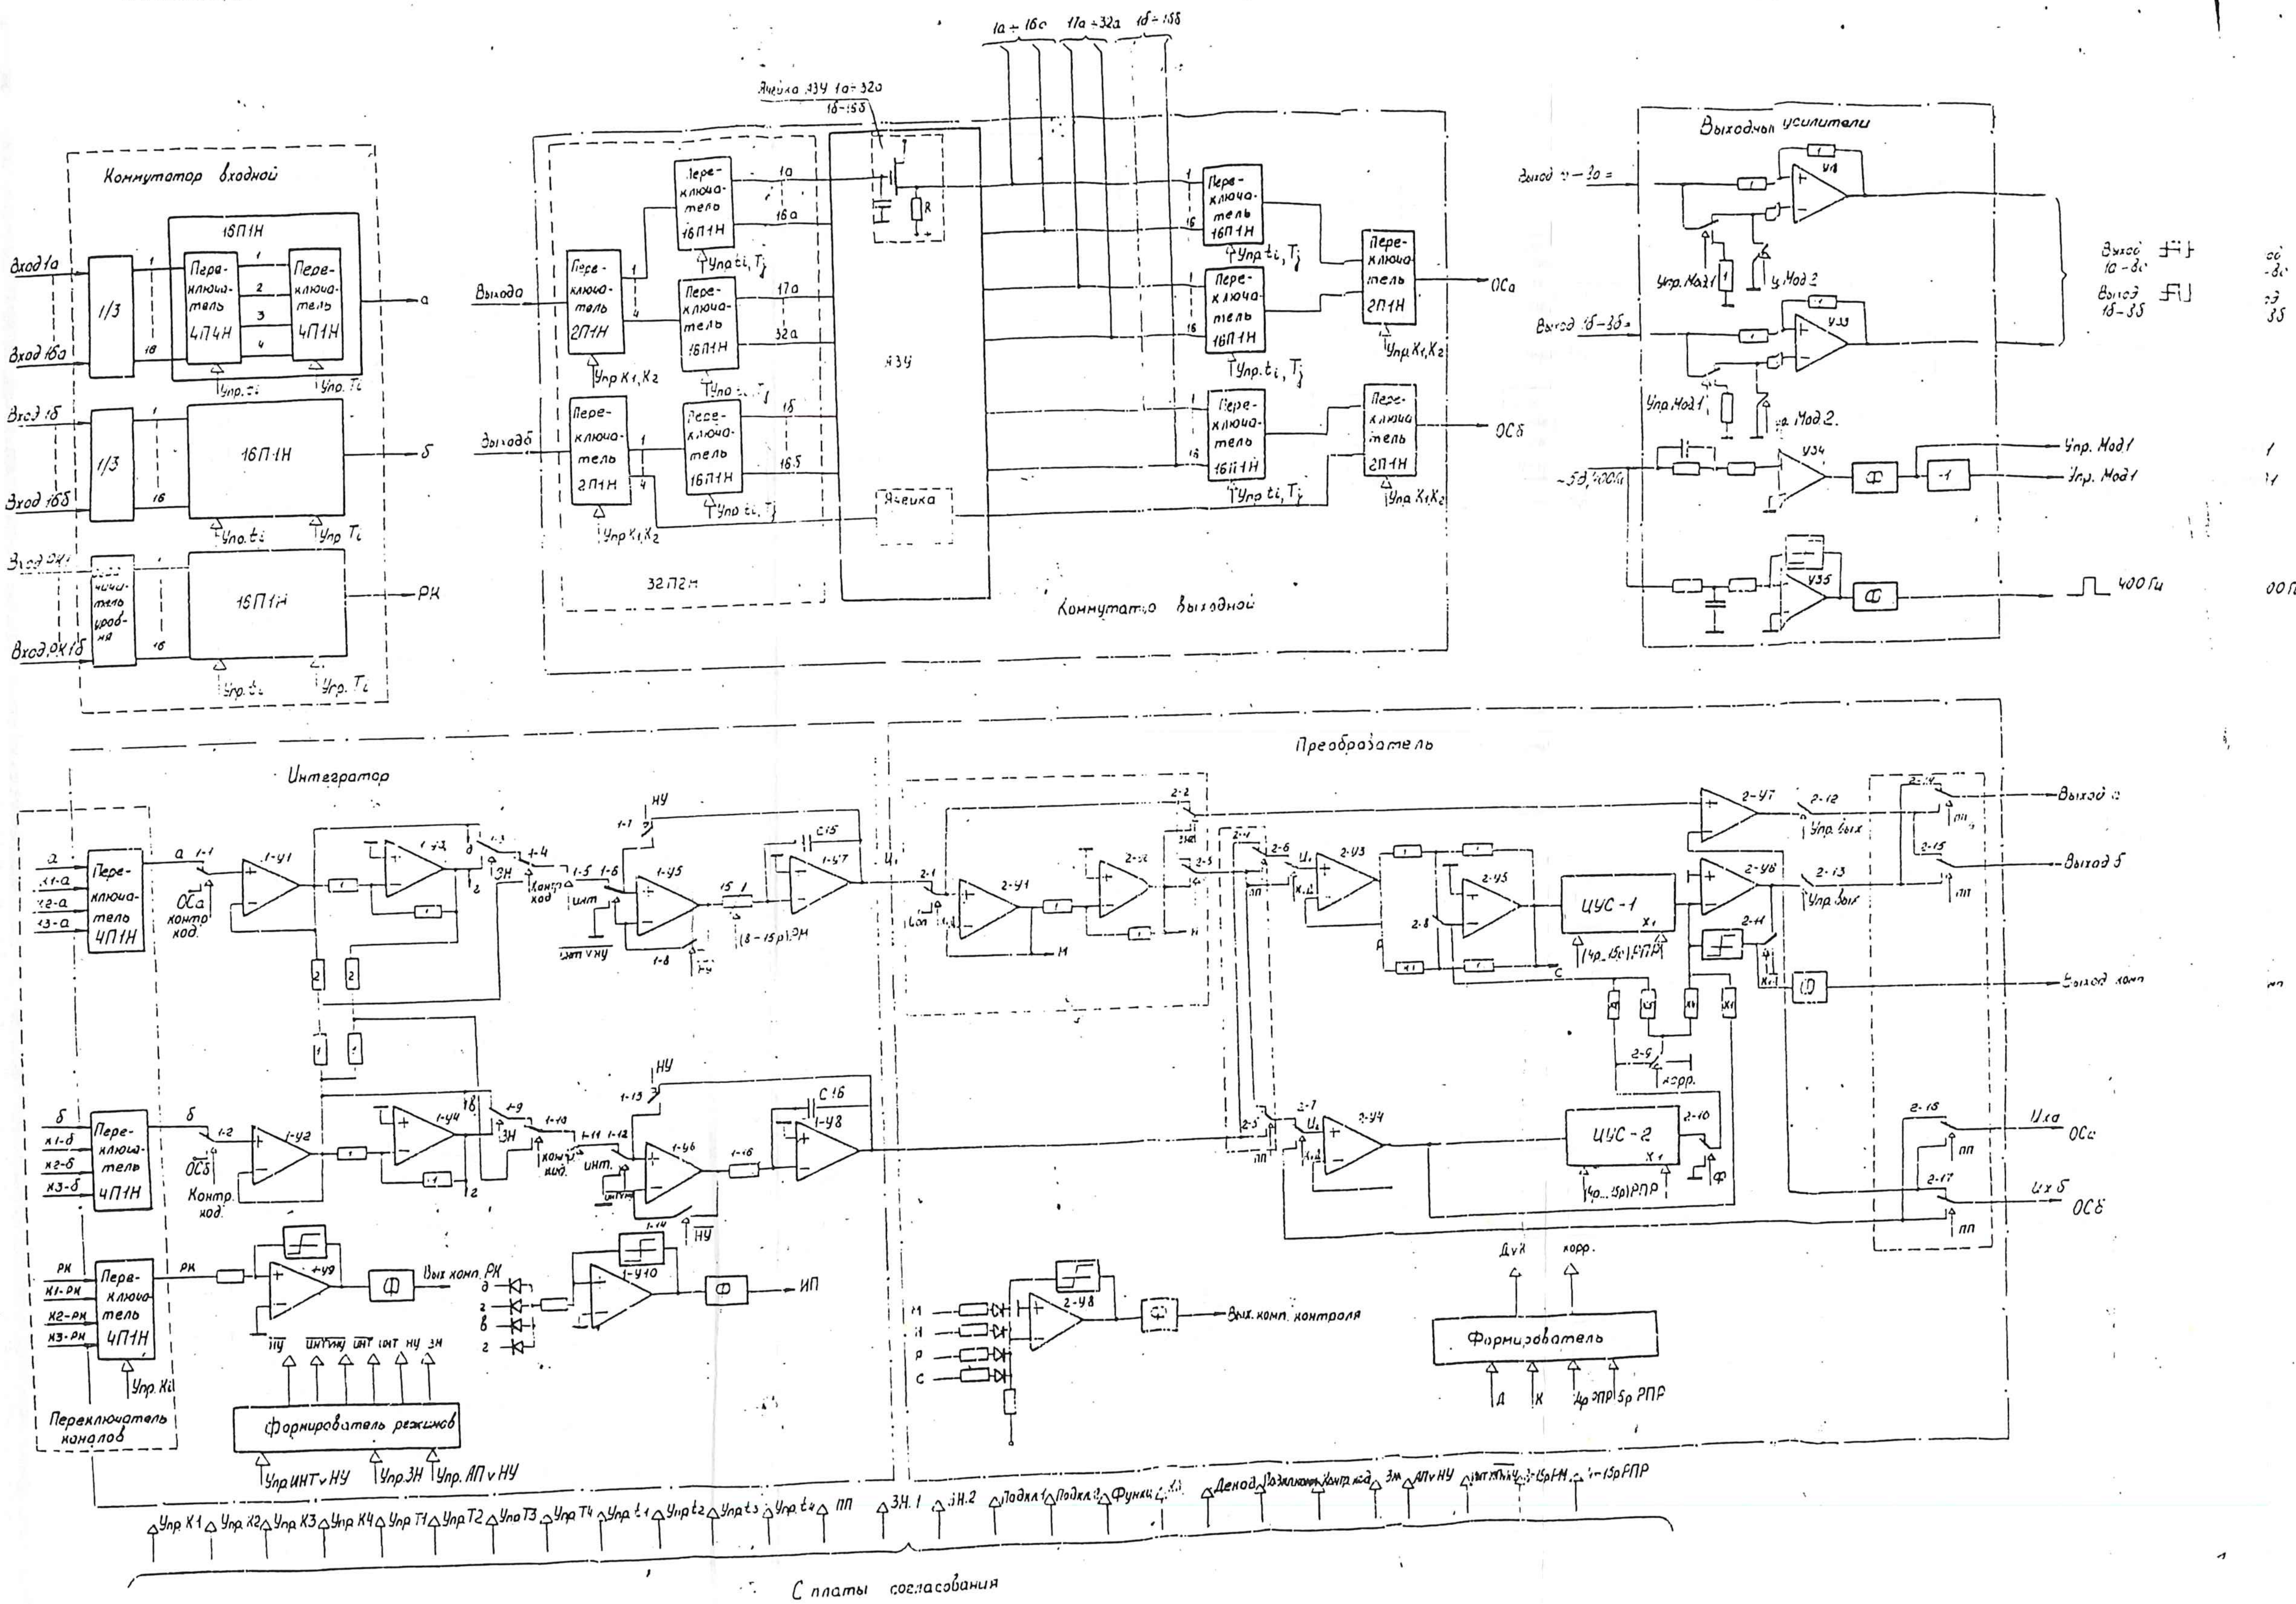
Коммутатор входной
Вход 1а
Вход 16а
Вход 1б
Вход 16б
Вход 1РК
Вход РК16
1/3
Переключатель 4П4Н
Переключатель 4П1Н
16П1Н
Упр. Т1
Упр. t1
Делитель кодов
РК
Ячейка АЗУ 1а-32а
1б-16б
Выход а
Выход б
Переключатель 2П1Н
Переключатель 16П1Н
Упр. К1, К2
Упр. ti, Tj
32П2Н
АЗУ
Ячейка
Коммутатор выходной
1а-16а
17а-32а
1б-16б
ОСа
ОСб
Выходные усилители
Выход 1а-32а
Выход 1б-16б
У1
У33
У34
У35
Упр. Мод 1
Упр. Мод 2
~5В, 400Гц
Ф
400 Гц
Интегратор
Преобразователь
Переключатель 4П1Н
Контр. код
ЗН
ИНТ
НУ
1-У1
1-У2
1-У3
1-У4
1-У5
1-У6
1-У7
1-У8
1-У9
1-У10
С15
С16
(1б-15р)РН
Вых. комп. РК
ИП
Формирователь режимов
Упр. ИНТ v НУ
Упр. ЗН
Упр. АП v НУ
Переключатель каналов
Упр. Кi
2-У1
2-У2
2-У3
2-У4
2-У5
2-У6
2-У7
2-У8
ЦУС-1
ЦУС-2
(Чр...15р)РПР
корр.
Выход а
Выход б
Выход комп.
Uх а ОСа
Uх б ОСб
ПП
Вых. комп. контроля
Формирователь
Дчл
корр.
Д
К
Чр РПР
5р РПР
Упр К1
Упр К2
Упр К3
Упр К4
Упр Т1
Упр Т2
Упр Т3
Упр Т4
Упр t1
Упр t2
Упр t3
Упр t4
ПП
ЗН.1
ЗН.2
Подкл.1
Подкл.2
Функц.
Декод.
Контр. код
АП v НУ
С платы согласования

Устройства цифро-аналоговых преобразований
Схема электрическая функциональная
Рис.2

2

68

69

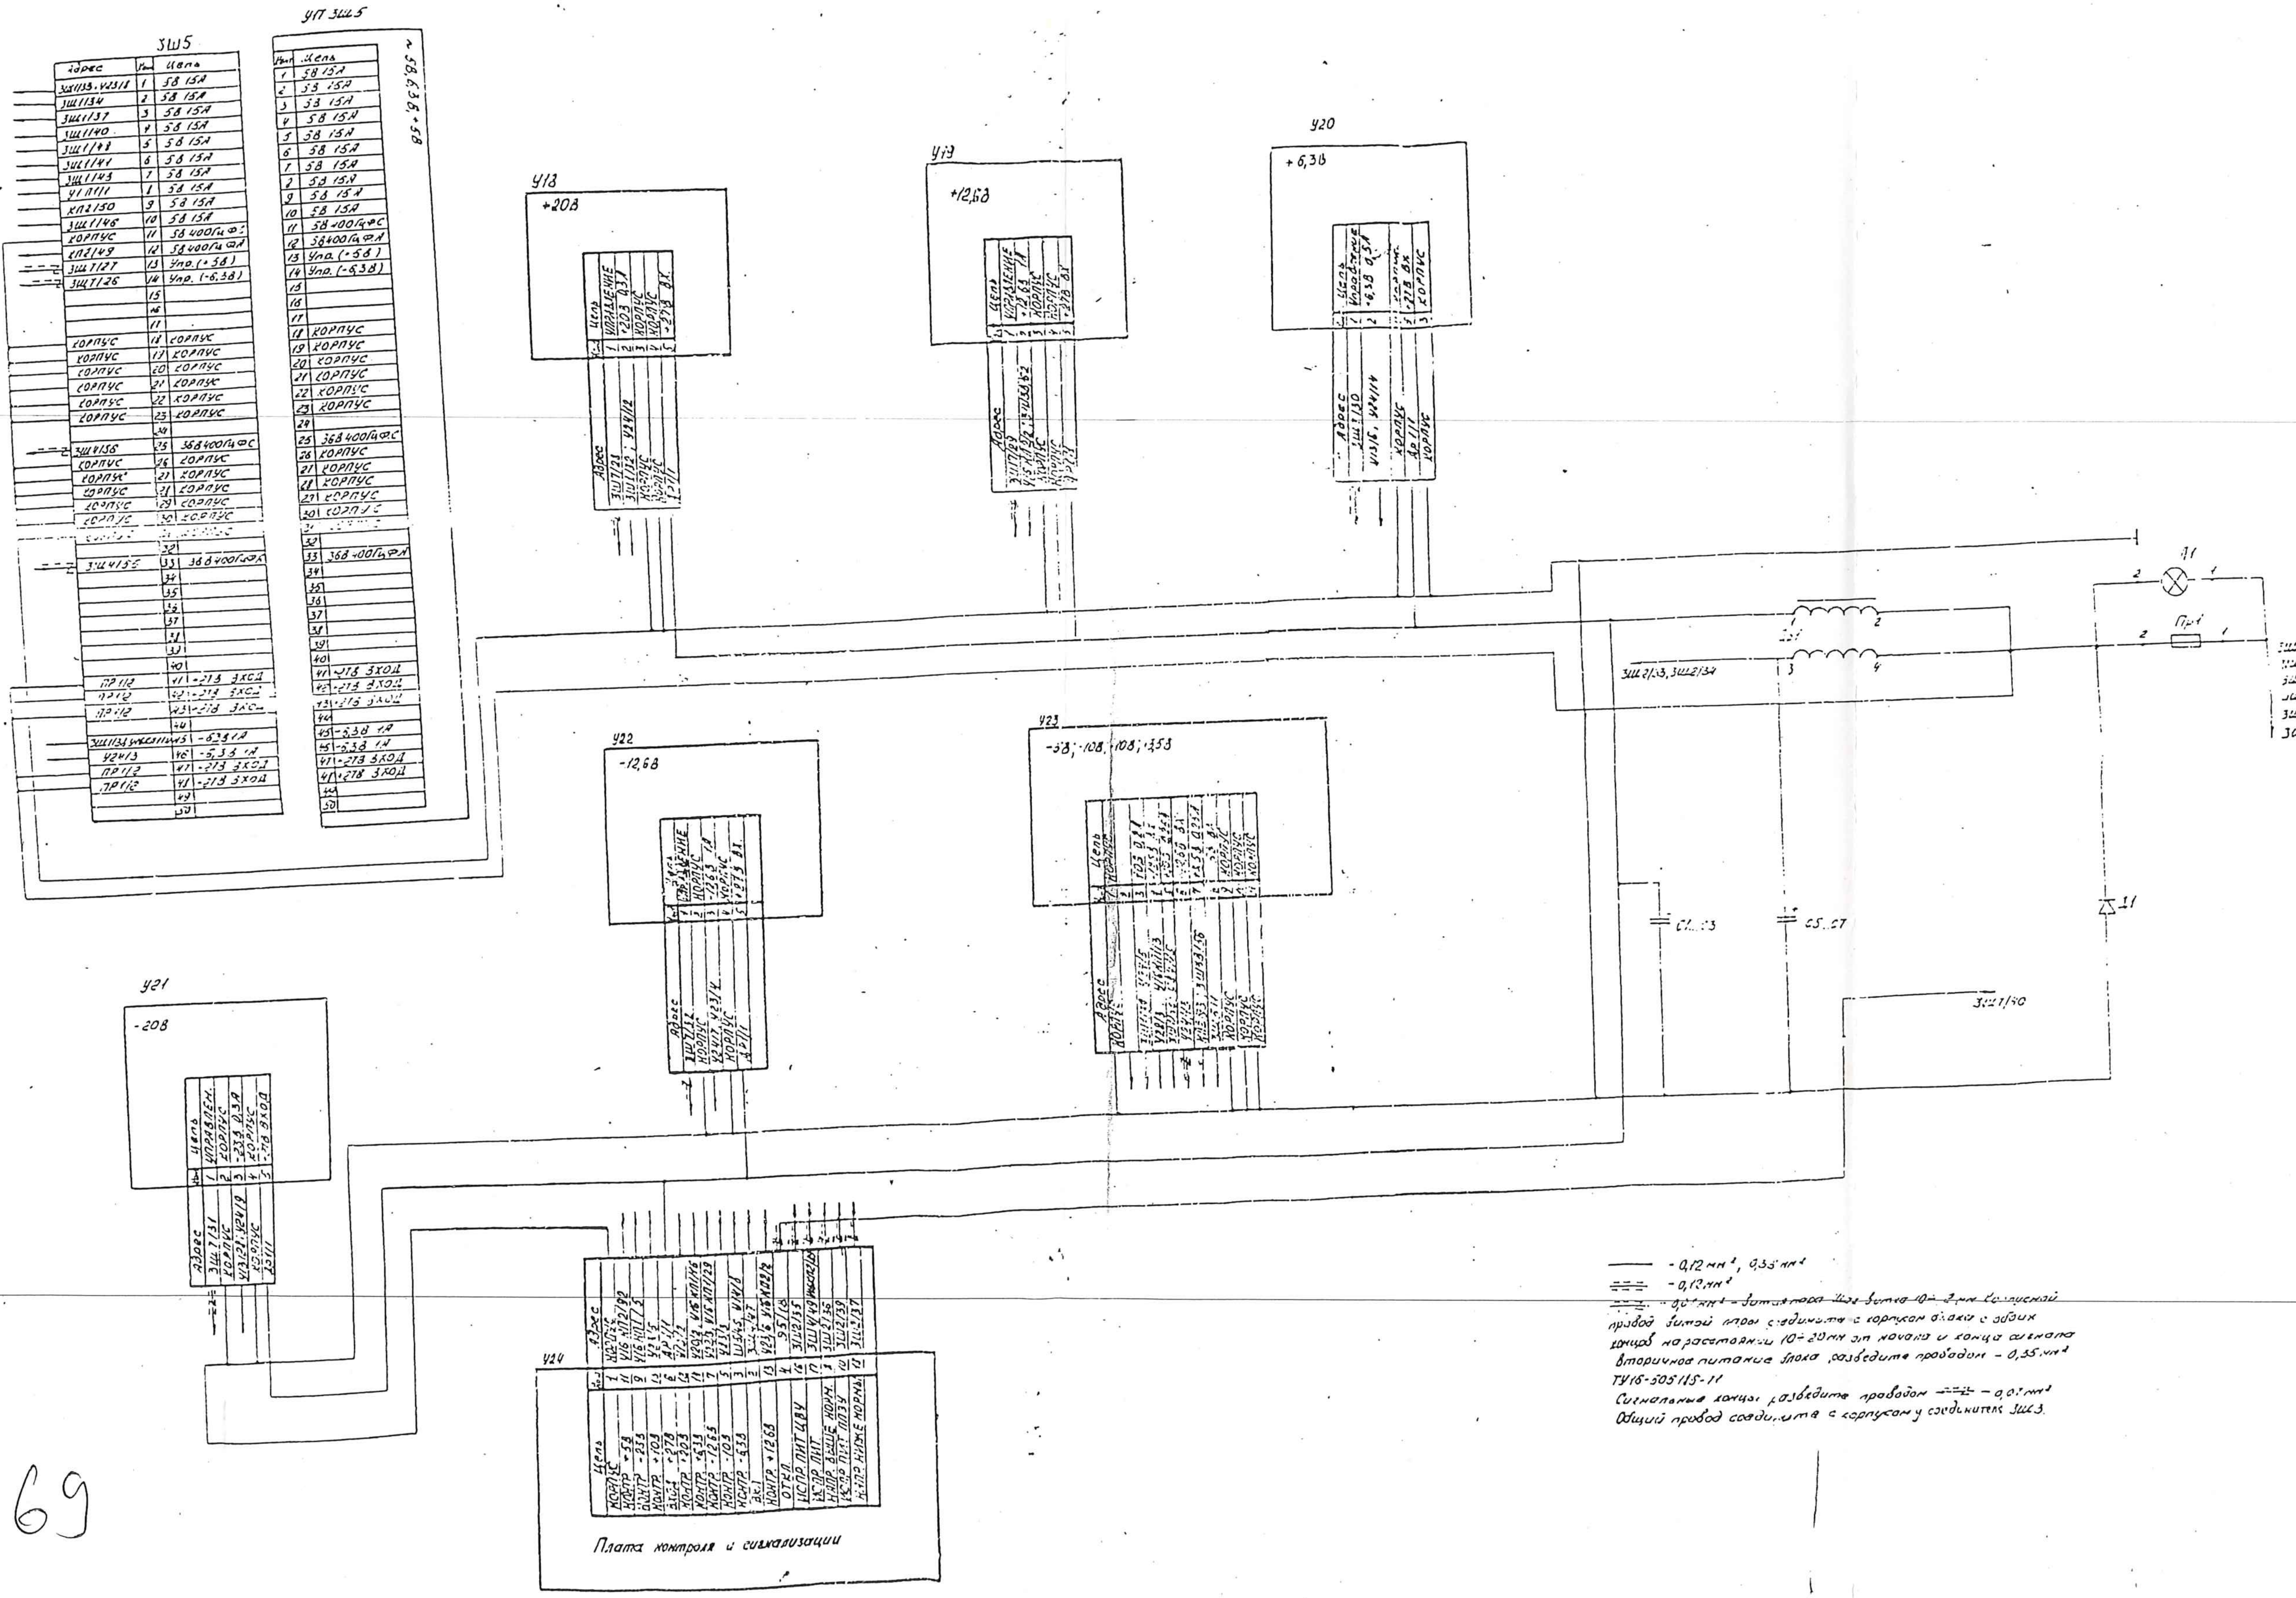
ЗШ5
УП ЗШ5
~ 5В, 6,3В, +5В
У18
+20В
У19
+12,6В
У20
+6,3В
У22
-12,6В
У23
-5В, -10В, +10В, -6,3В
У21
-20В
У24
Адрес
Цепь
КОРПУС
КОНТР. +5В
КОНТР. -23В
КОНТР. +10В
КОНТР. +27В
КОНТР. +20В
КОНТР. +6,3В
КОНТР. -12,6В
КОНТР. -10В
КОНТР. -6,3В
Вкл
КОНТР. +12,6В
ОТКЛ.
ИСПР. ПИТ ЦВУ
ИСПР. ПИТ.
НАПР. ВЫШЕ НОРМ.
ИСПР. ПИТ ПЛЗУ
НАПР. НИЖЕ НОРМЫ
Плата контроля и сигнализации
Л1
1
2
Пр1
1
2
Др1
1
2
3
4
ЗШ2/33, ЗШ2/34
ЗШ4/35
ЗШ4/54
ЗШ4/58
ЗШ4/60
ЗШ4/63
ЗШ4/64
С1...С3
С5...С7
Д1
ЗШ1/40

ЗШ5

Адрес	Конт	Цепь
ЗШ1/33, У23/1	1	5В 15А
ЗШ1/34	2	5В 15А
ЗШ1/37	3	5В 15А
ЗШ1/40	4	5В 15А
ЗШ1/48	5	5В 15А
ЗШ1/41	6	5В 15А
ЗШ1/43	7	5В 15А
У1П1/1	8	5В 15А
КП2/50	9	5В 15А
ЗШ1/46	10	5В 15А
КОРПУС	11	5В 400Гц ФС
КП2/49	12	5В 400Гц ФА
ЗШ7/27	13	Упр. (+5В)
ЗШ7/26	14	Упр. (-6,3В)
	15	
	16	
	17	
КОРПУС	18	КОРПУС
КОРПУС	19	КОРПУС
КОРПУС	20	КОРПУС
КОРПУС	21	КОРПУС
КОРПУС	22	КОРПУС
КОРПУС	23	КОРПУС
	24	
ЗШ4/56	25	36В 400Гц ФС
КОРПУС	26	КОРПУС
КОРПУС	27	КОРПУС
КОРПУС	28	КОРПУС
КОРПУС	29	КОРПУС
КОРПУС	30	КОРПУС
[illegible]	31	[illegible]
	32	
ЗШ4/55	33	36В 400Гц ФА
	34	
	35	
	36	
	37	
	38	
	39	
	40	
ПР1/2	41	-27В ВХОД
ПР1/2	42	-27В ВХОД
ПР1/2	43	-27В ВХОД
	44	
ЗШ1/34, [illegible]	45	-6,3В 1А
У24/3	46	-6,3В 1А
ПР1/2	47	-27В ВХОД
ПР1/2	48	-27В ВХОД
	49	
	50	

УП ЗШ5

Конт	Цепь
1	5В 15А
2	5В 15А
3	5В 15А
4	5В 15А
5	5В 15А
6	5В 15А
7	5В 15А
8	5В 15А
9	5В 15А
10	5В 15А
11	5В 400Гц ФС
12	5В 400Гц ФА
13	Упр. (+5В)
14	Упр. (-6,3В)
15	
16	
17	
18	КОРПУС
19	КОРПУС
20	КОРПУС
21	КОРПУС
22	КОРПУС
23	КОРПУС
24	
25	36В 400Гц ФС
26	КОРПУС
27	КОРПУС
28	КОРПУС
29	КОРПУС
30	КОРПУС
31	[illegible]
32	
33	36В 400Гц ФА
34	
35	
36	
37	
38	
39	
40	
41	+27В ВХОД
42	+27В ВХОД
43	+27В ВХОД
44	
45	-6,3В 1А
46	-6,3В 1А
47	+27В ВХОД
48	+27В ВХОД
49	
50	

——— - 0,12 мм², 0,35 мм²
═══ - 0,12 мм²
═══ - 0,07 мм² - Витая пара шаг витка 10÷2 мм Корпусной провод витой пары соединить с корпусом блока с обоих концов на расстоянии 10÷20 мм от начала и конца сигнала

Вторичное питание блока, разведите проводом - 0,35 мм² ТУ16-505.115-11

Сигнальные концы разведите проводом ═══ - 0,07 мм²

Общий провод соединить с корпусом у соединителя ЗШ3.

(Продолжение см. на листе 2)