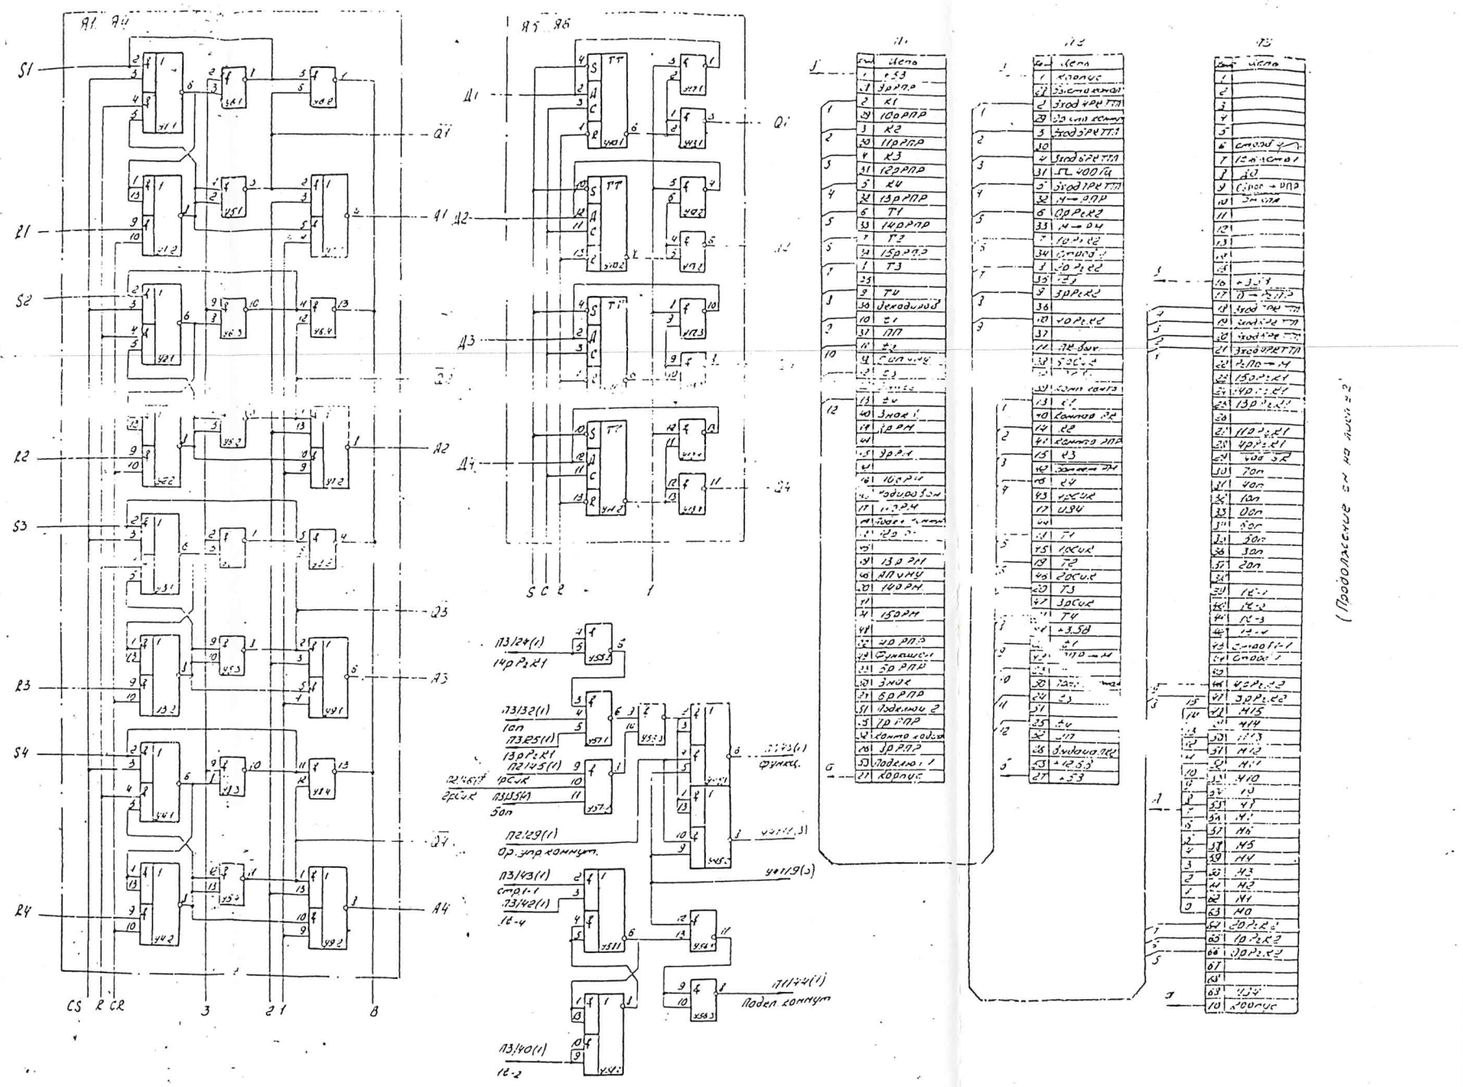


Устройство управления преобразованием
Схема электрическая принципиальная ЕУ3.057.I40 33
Рис.7 (Лист I из 3)