ации

Кол.	Примечание
2	
1	
3	
2	
3	
2	
1	
1	
1	
2	
1	

Ячейка 1...13

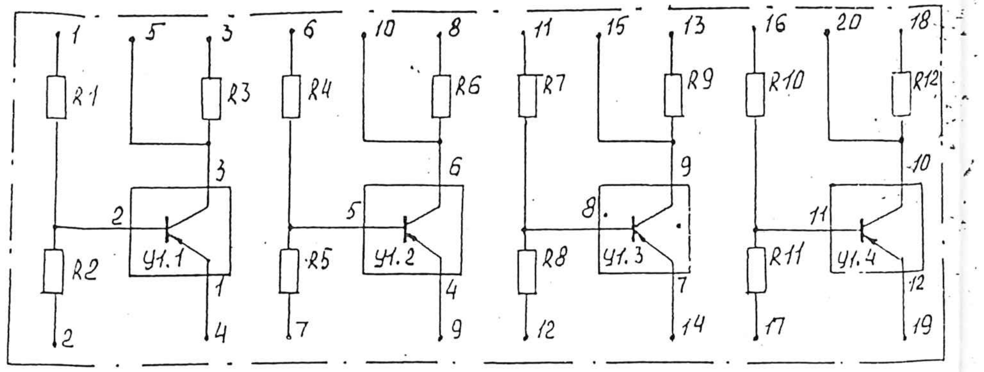
1
5
3
6
10
8
11
15
13
16
20
18
R1
R2
R3
R4
R5
R6
R7
R8
R9
R10
R11
R12
У1.1
У1.2
У1.3
У1.4
2
4
7
9
12
14
17
19

П1

Конт	Цепь
27	-23В
1	+3,5В
26	Вых.1
25	Вых.2
24	Вых.3
23	Вых.4
22	Вых.5
21	Вых.6
20	Вых.7
19	Вых.8
18	Вых.9
17	Вых.10
16	Вых.11
15	Вых.12
14	Вых.13
13	Вых.14
12	Вых.15
11	Вых.16
10	Вых.17
9	Вых.18
8	Вых.19
7	Вых.20
6	Вых.21
5	Вых.22
4	Вых.23
3	Вых.24
2	Вых.25
53	Вых.26
52	Вых.27
51	Вых.28
50	Вых.29
49	Вых.30
48	Вых.31
47	Вых.32
46	Вых.33
45	Вых.34
[illegible]	[illegible]
43	Вых.36
42	Вых.37
41	Вых.38
40	Вых.39
39	Вых.40
38	Вых.41
37	Вых.42
36	Вых.43
35	Вых.44
34	Вых.45
33	Вых.46
32	Вых.47
31	Вых.48
30	Вых.49
29	Вых.50
28	Вых.51

П2

Конт	Цепь
27	+5В
26	Вх.1
25	Вх.2
24	Вх.3
23	Вх.4
22	Вх.5
21	Вх.6
20	Вх.7
19	Вх.8
18	Вх.9
17	Вх.10
16	Вх.11
15	Вх.12
14	Вх.13
13	Вх.14
12	Вх.15
11	Вх.16
10	Вх.17
9	Вх.18
8	Вх.19
7	Вх.20
6	Вх.21
5	Вх.22
4	Вх.23
3	Вх.24
2	Вх.25
53	Вх.26
52	Вх.27
51	Вх.28
50	Вх.29
49	Вх.30
48	Вх.31
47	Вх.32
46	Вх.33
45	Вх.34
44	Вх.35
[illegible]	[illegible]
42	Вх.37
41	Вх.38
40	Вх.39
39	Вх.40
38	Вх.41
37	Вх.42
36	Вх.43
35	Вх.44
34	Вх.45
33	Вх.46
32	Вх.47
31	Вх.48
30	Вх.49
29	Вх.50
28	Вх.51
1	Корпус

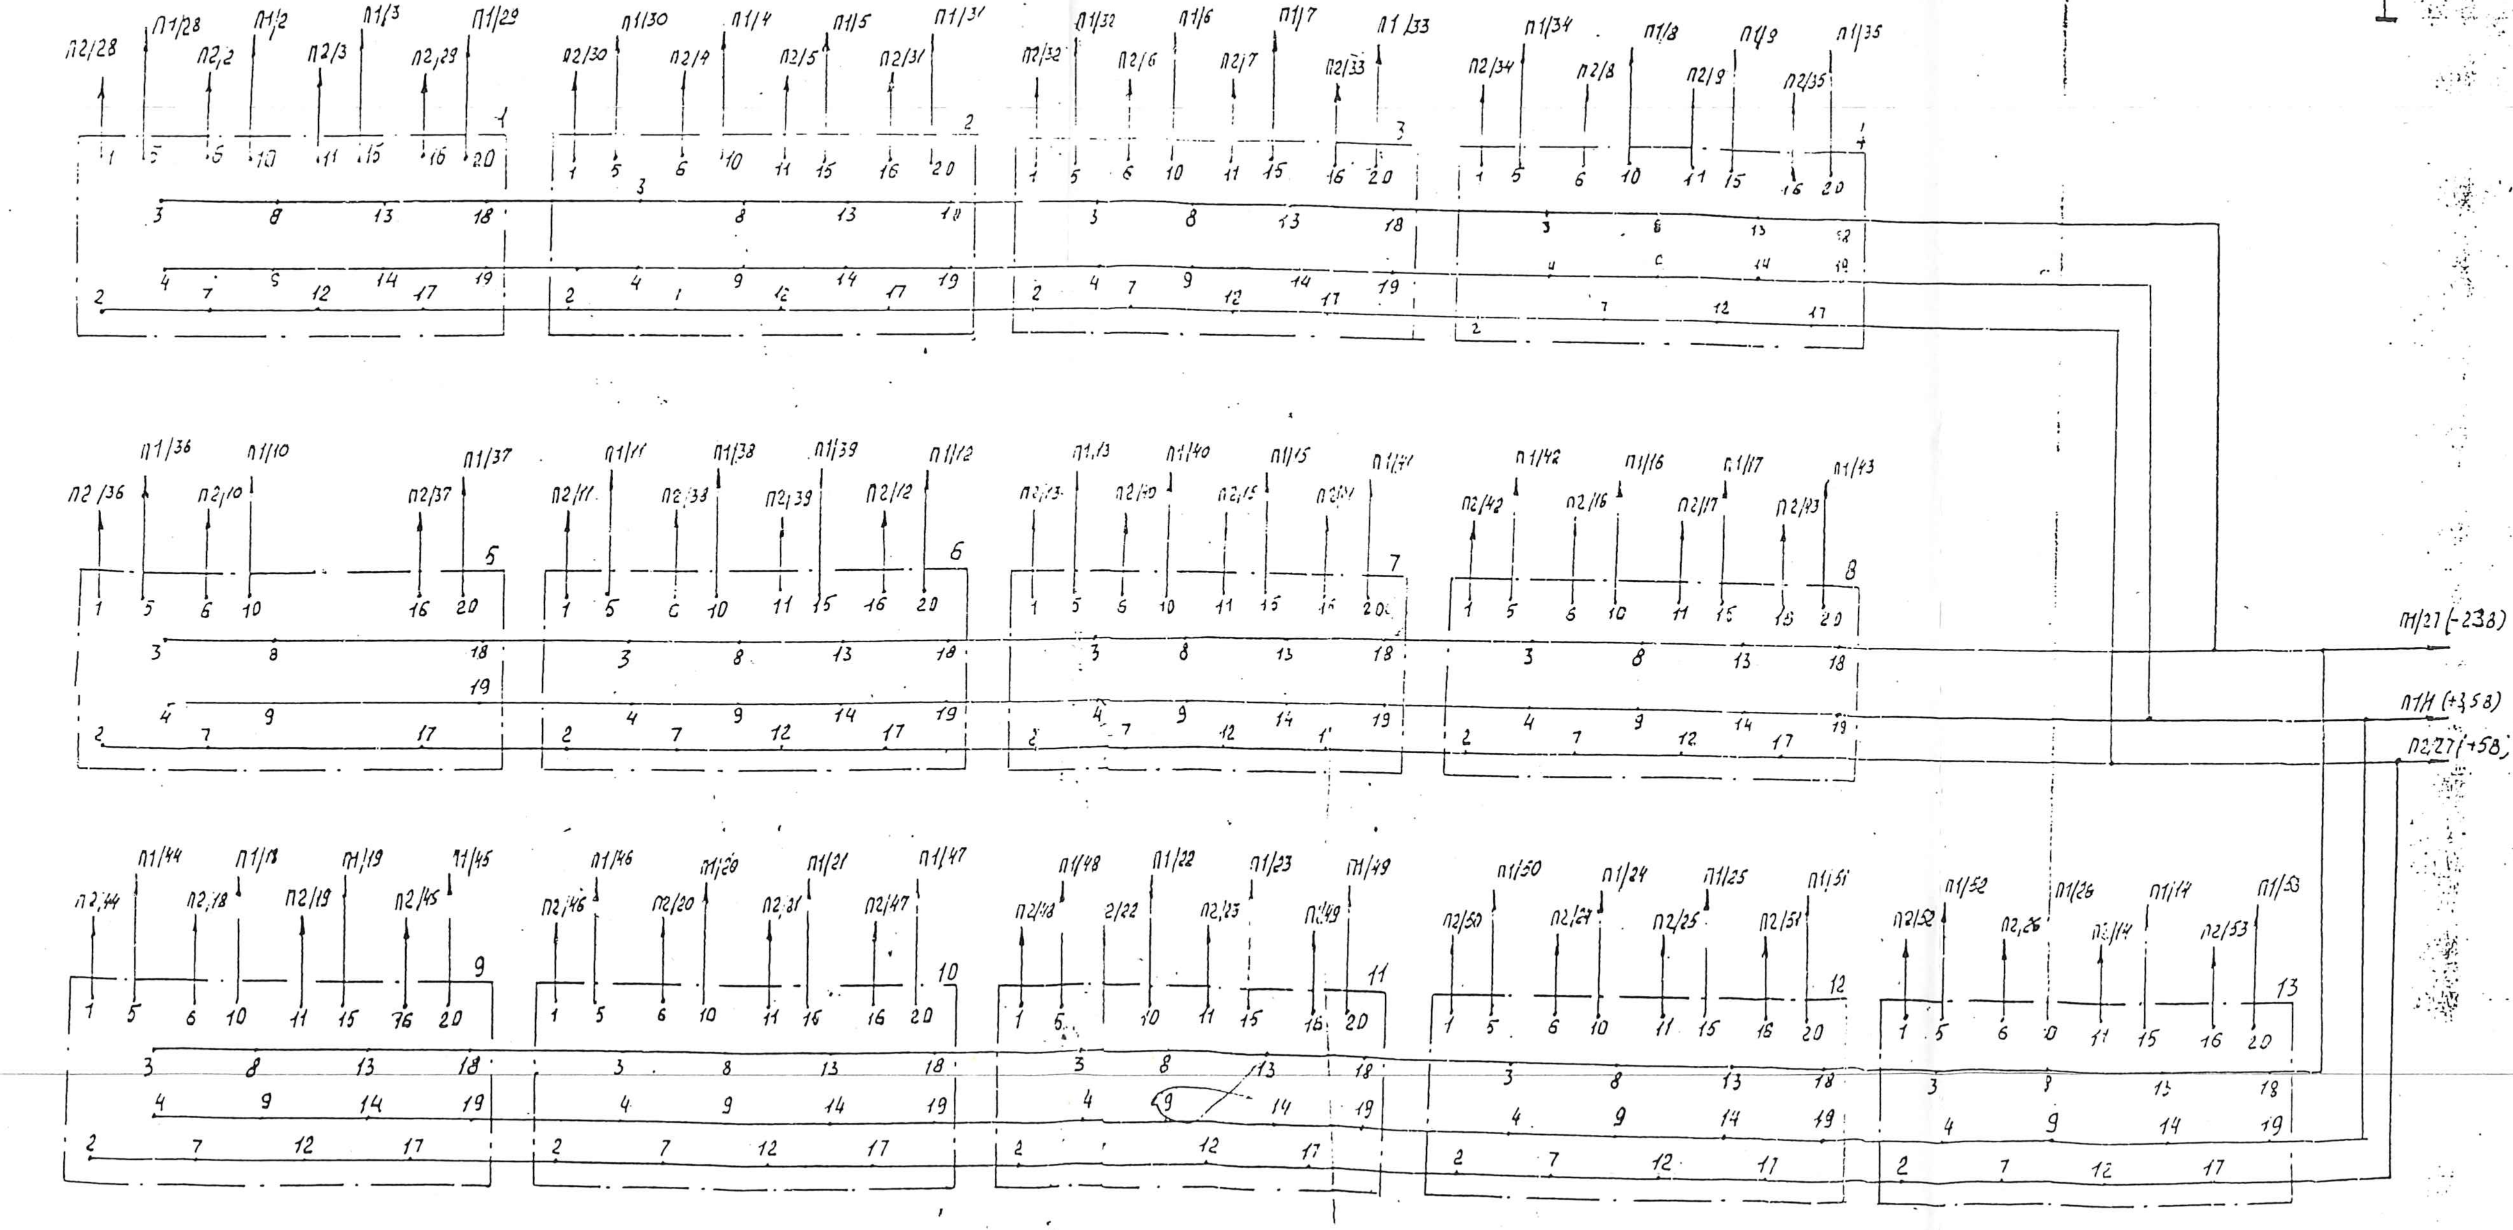
П2/28
П1/28
П2/2
П1/2
П2/3
П1/3
П2/29
П1/29
П2/30
П1/30
П2/4
П1/4
П2/5
П1/5
П2/31
П1/31
П2/32
П1/32
П2/6
П1/6
П2/7
П1/7
П2/33
П1/33
П2/34
П1/34
П2/8
П1/8
П2/9
П1/9
П2/35
П1/35
П2/36
П1/36
П2/10
П1/10
П2/37
П1/37
П2/11
П1/11
П2/38
П1/38
П2/39
П1/39
П2/12
П1/12
П2/13
П1/13
П2/40
П1/40
П2/15
П1/15
П2/41
П1/41
П2/42
П1/42
П2/16
П1/16
П2/17
П1/17
П2/43
П1/43
П2/44
П1/44
П2/18
П1/18
П2/19
П1/19
П2/45
П1/45
П2/46
П1/46
П2/20
П1/20
П2/21
П1/21
П2/47
П1/47
П2/48
П1/48
П2/22
П1/22
П2/23
П1/23
П2/49
П1/49
П2/50
П1/50
П2/24
П1/24
П2/25
П1/25
П2/51
П1/51
П2/52
П1/52
П2/26
П1/26
П2/14
П1/14
П2/53
П1/53
1
2
3
4
5
6
7
8
9
10
11
12
13
1 5 6 10 11 15 16 20
3 8 13 18
4 9 14 19
2 7 12 17
П1/27 (-23В)
П1/1 (+3,5В)
П2/27 (+5В)

30

Плата согласования
Схема электрическая принципиальная ВШ3.031.020 Э3
Рис.II

99

99

10.23.03
иложение
тр.63,64
кт 22/84